


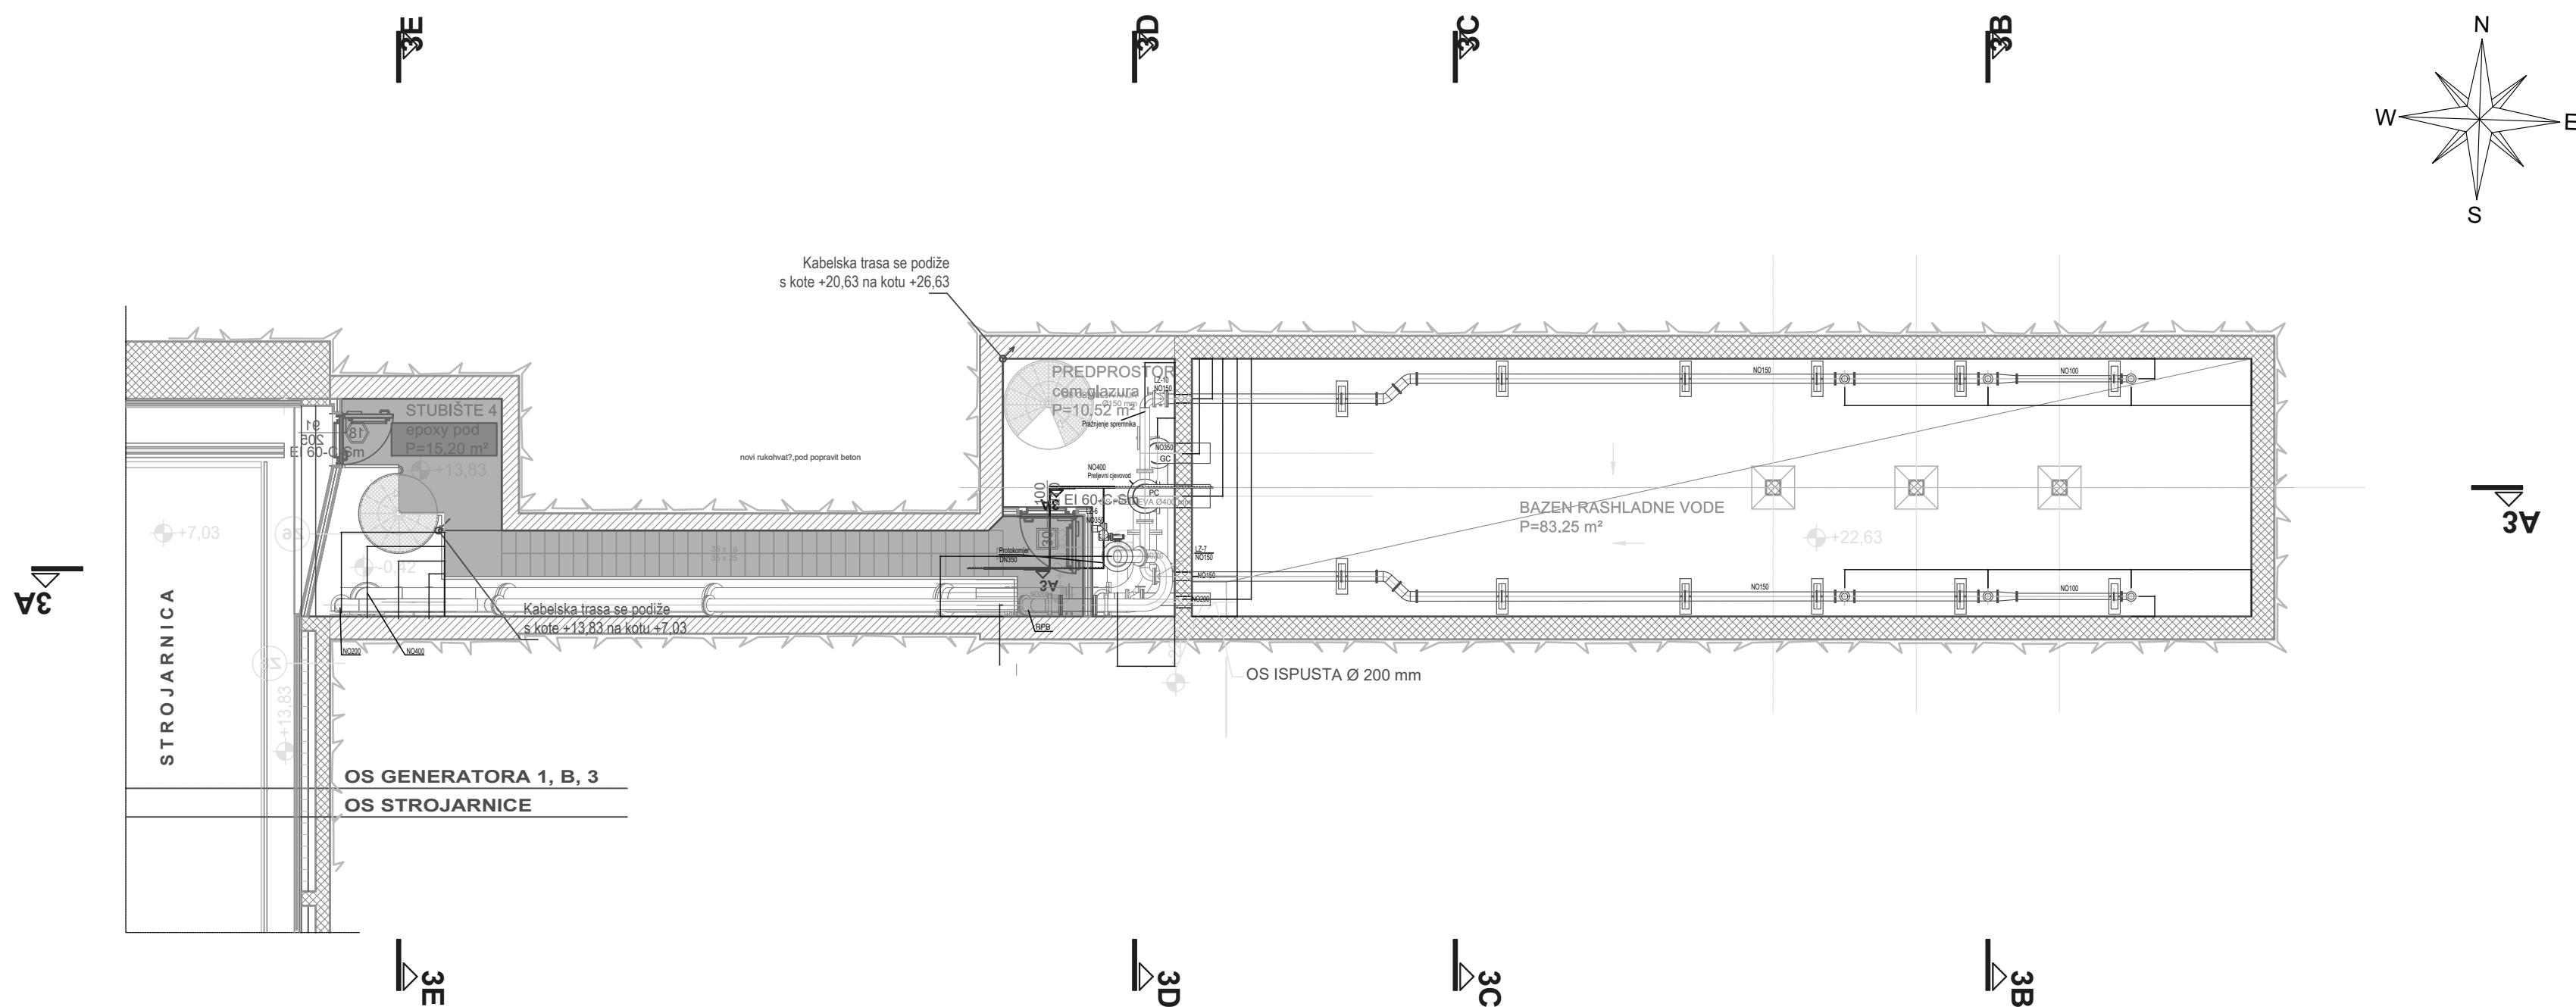

00	Radna verzija	2026-07-31	Luka Božićević
REV.	NAPOMENA	DATUM	IZRADIO
Rev.	Note	Date	Drawn

SINTAKSA A Volth Company		Sintaksa d.o.o. Ulica Domovinskog rata 104C, 21 000 Split T: +385 1 2310 271 info@sintaksa.hr www.sintaksa.hr		POSLOJ Project / job name		REKONSTRUKCIJA HE SENJ - FAZA I	
PROJEKTANT: Design engineer		Patrik Kovač, mag.ing.el.techn.inf.		INVESTITOR / POČIOSTELU / ZAHTEJEVA: Investor		HRVATSKA ELEKTROPRIVREDA d.o.o. Ulica grada Vukovara 37, 10000 Zagreb, OIB: 28921978587	
IZRADIO: Drawn		Luka Božićević, mag.ing.el.		PROJEKTIRANI DIO: Scope of design		ELEKTROTEHNIČKI PROJEKT	
KONTROLIRAO: Checked		Patrik Kovač, mag.ing.el.techn.inf.		RAZINA-STRIKA: Design type		IZVEDBENI PROJEKT	
GLAVNI PROJEKTANT: Design manager		Natko Vučković, dipl.ing.el.		SADRŽAJ: Content		DISPOZICIJA ELEKTRO OPREME SUSTAVA RASHLADE - KOTA +13.83	
MUJESTO I DATUM: Place and date		Zagreb, 2026-07-31		ZOP Comment or des.		PROJEKT Project	MAPA Folder
OZNAKA NACRTA Drawing designation		FORMAT Paper size		MJERILO Scale		PRILOG Drawing	REVIZIJA Revisor
26015-DD-EE-01-201				1:100		LIST Page	
SEN.1273 - 26015-DD -		EE-01		201		00	1/1