


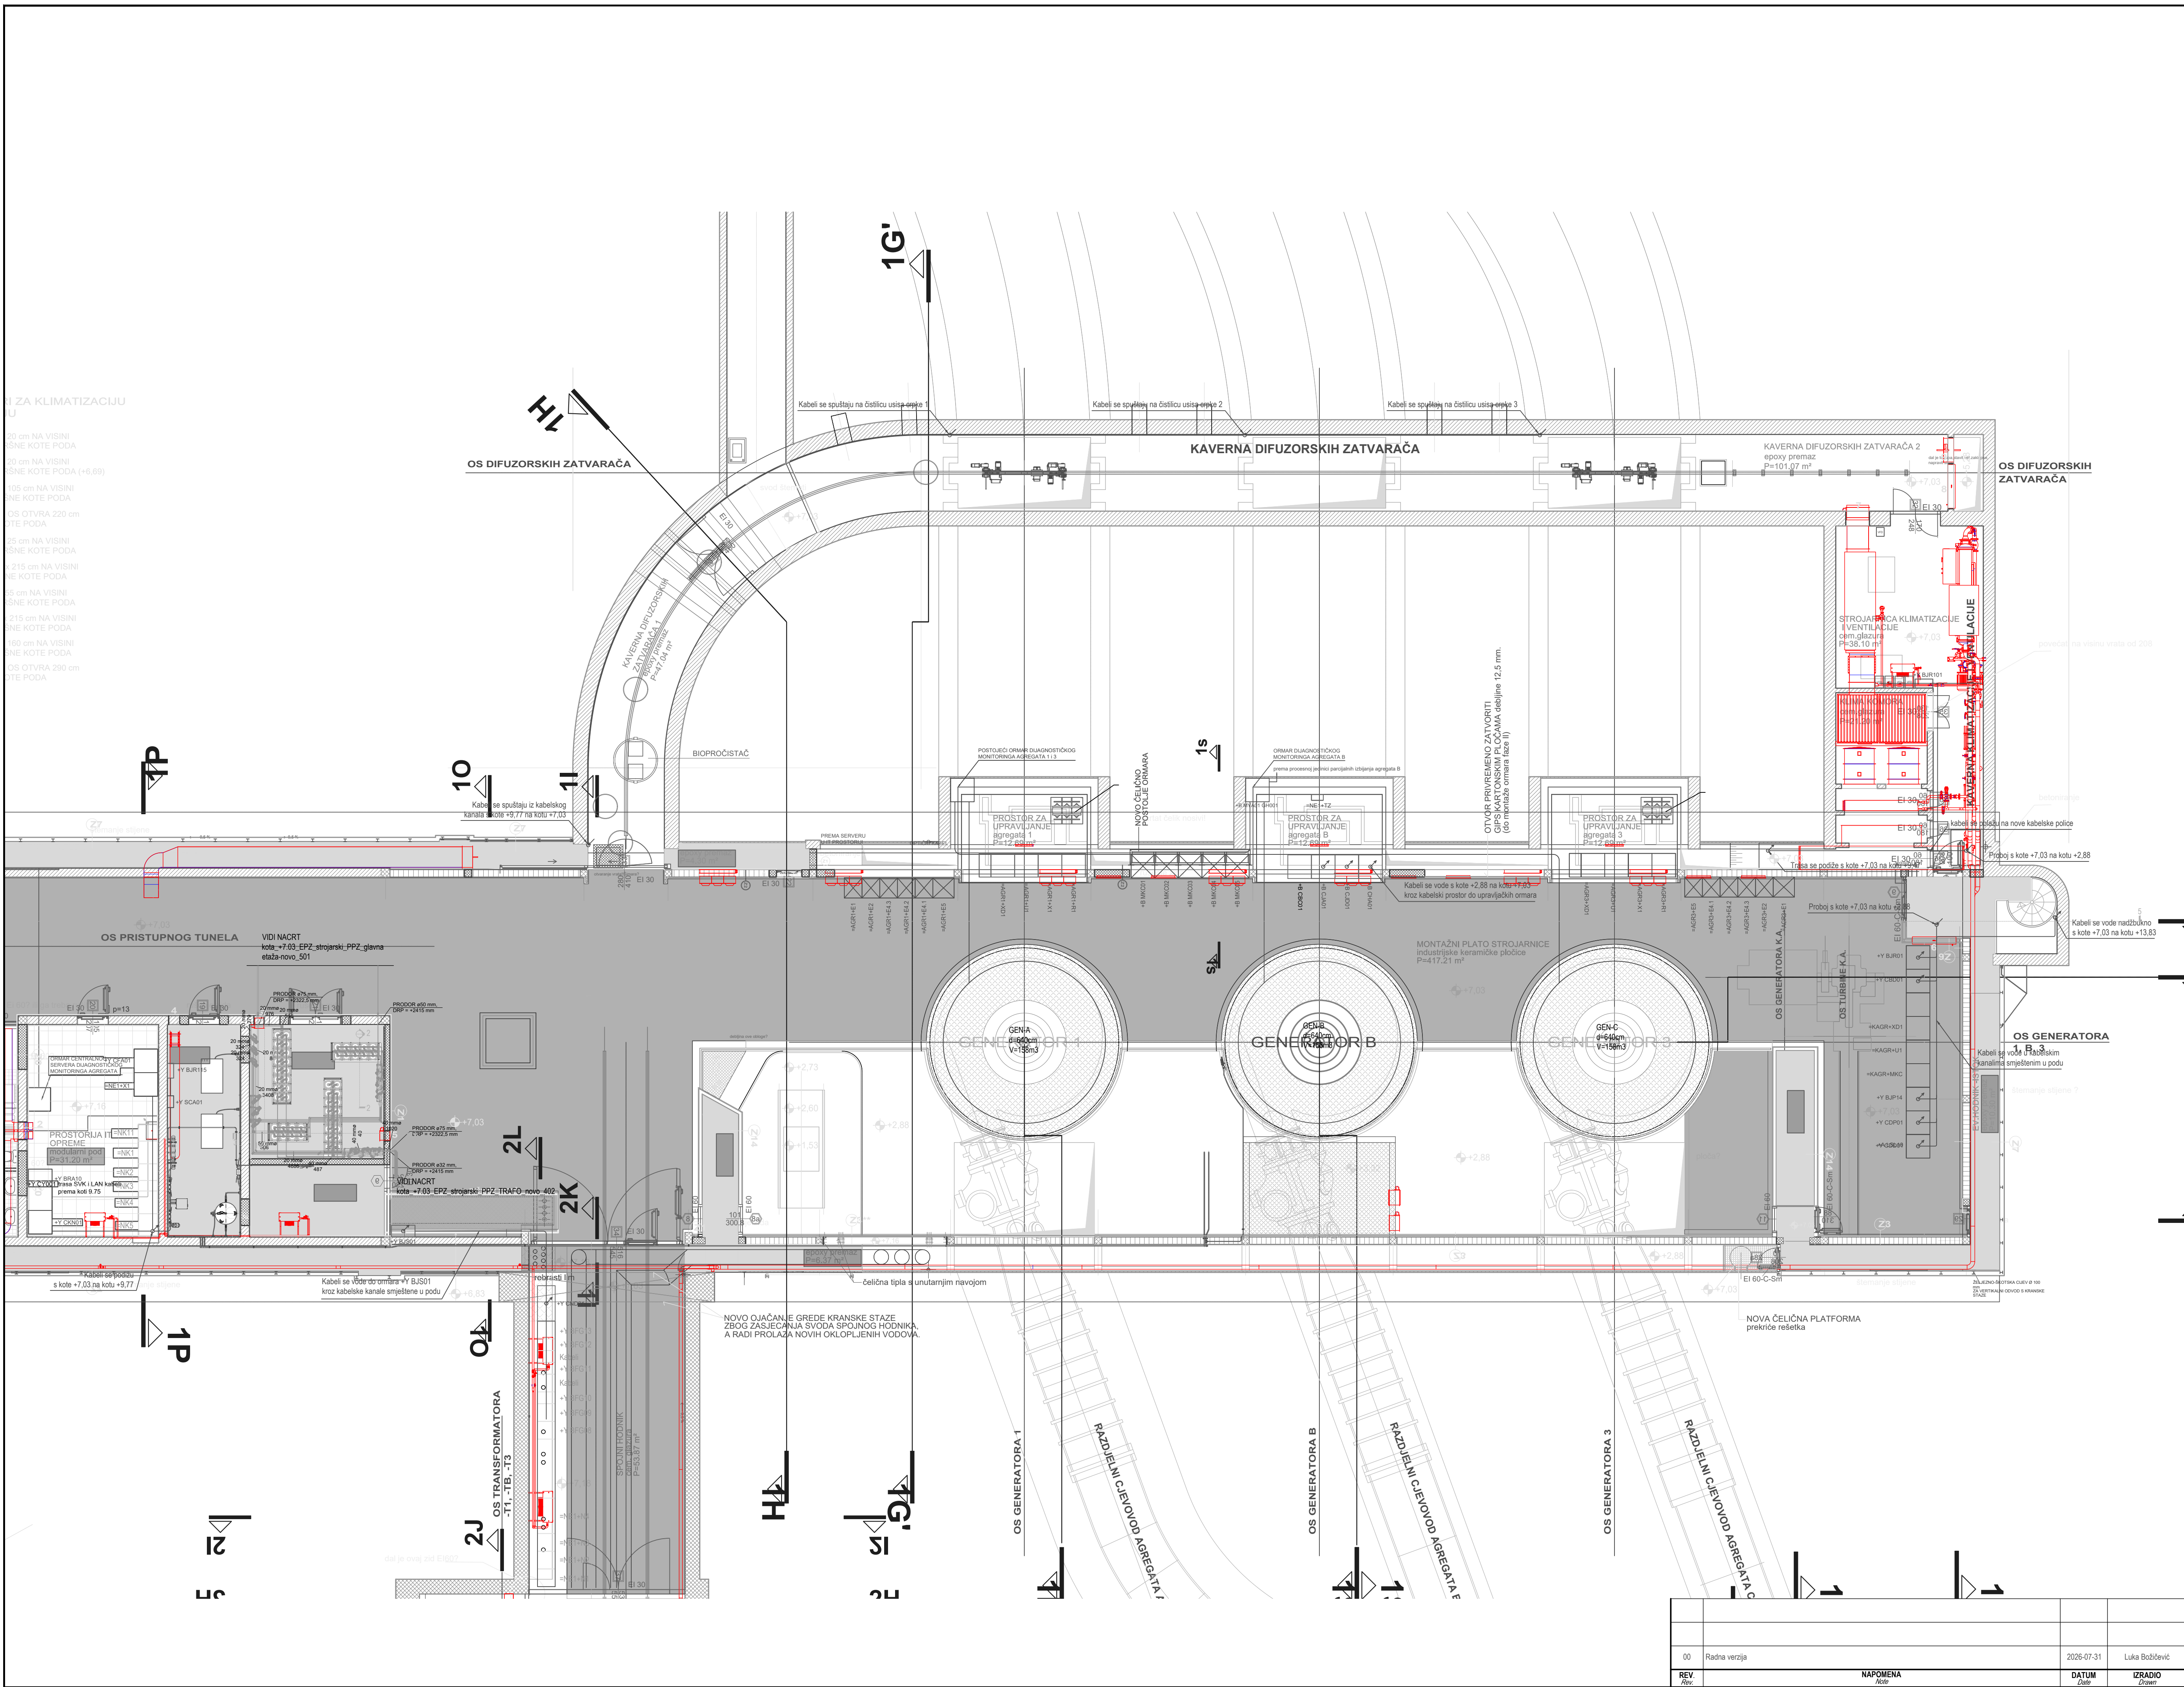

Naziv	Opis
Omari koji se ugrađuju u fazi I	
=B CHA01	Omari relejne zaštite agregata B
=B CJA01	Omari upravljanja agregata B
=B CJD01	Omari procesne stanice agregata B
=B MKC01...6	Omari uzbuđe agregata B
=Y BUR01	Omari klimatizacije i ventilacije
=Y BUR101	Omari klimatizacije i ventilacije
=Y BUR213	Omari odmišljavanja stubišta 3
=Y CBD01	Omari LPJ sustava klimatizacije i ventilacije
=Y BLP14	Omari filtera i ventila sustava rashlade
=Y CDP01	Omari LPJ sustava opskrbe rashladnom vodom
=Y CDD01	Omari LPJ sustava drenaže
=Y CFA01	Omari kontrolnih mjerenja
=Y CKN01	Omari računalne opreme
=Y BJS01	Omari zajedničkih uređaja elektrane
=Y SCA01	Omari upravljanja kompresorima
=Y BRA10	Omari besprekidnog napajanja 230V, 50Hz
Postojeći omari	
=AGR1+E1 *	Omari digitalnog regulatora agregata 1
=AGR1+E2 *	Omari upravljanja agregata 1
=AGR1+E3 *	Omari prekidača razbuđe agregata 1
=AGR1+E4.1 *	Omari tristrorskog usmjerivača agregata 1
=AGR1+E4.2 *	Omari tristrorskog usmjerivača agregata 1
=AGR1+E4.3 *	Omari tristrorskog usmjerivača agregata 1
=AGR1+E5 *	Omari izmjeničnih prekidača agregata 1
=AGR1+XD1	Omari turbinskog usmjerivača agregata 1
=AGR1+U1	Upravljački omari agregata 1
=AGR1+R1	Omari zaštite agregata 1
=AGR1+X1	Omari procesne stanice agregata 1
=AGR3+E1	Omari digitalnog regulatora agregata 3
=AGR3+E2	Omari upravljanja agregata 3
=AGR3+E3	Omari prekidača razbuđe agregata 3
=AGR3+E4.1	Omari tristrorskog usmjerivača agregata 3
=AGR3+E4.2	Omari tristrorskog usmjerivača agregata 3
=AGR3+E4.3	Omari tristrorskog usmjerivača agregata 3
=AGR3+E5	Omari izmjeničnih prekidača agregata 3
=AGR3+XD1	Omari turbinskog regulatora agregata 3
=AGR3+U1	Upravljački omari agregata 3
=AGR3+R1	Omari zaštite agregata 3
=AGR3+X1	Omari procesne stanice agregata 3
=KAGR+XD1	Omari turbinske regulacije kućnog agregata
=KAGR+U1	Omari relejne zaštite, upravljanja i nadzora kuć. agr.
=KAGR+MKC	Omari uzbuđe kućnog agregata
=NE1+TZ	Omari tablastog zatvarača Himtine

NAPOMENA: postojeći omari označeni * se izmjenjaju prije početka faze I

LEGENDA:
● Vertikalna kabelska trasa - kabeli se spuštaju na nižu kotu
○ Vertikalna kabelska trasa - kabeli se podižu na višu kotu
— Postojeće kabelske trase
- - - Nove kabelske trase

SINTAKSA A Voith Company Sintaksa d.o.o. Ulica Domovinskog rata 100C, 10100 Šibenik T: +385 1 2300 710 F: +385 1 2300 711 info@sintaksa.hr www.sintaksa.hr		NAZIV PROJEKTA / POSLA HE SENJ / Projekt / posla INVESTICIJER / ZAPOSLEN HRVATSKA ELEKTROPRIVREDA d.o.o. Ulica grada Vukovara 37, 10000 Zagreb OIB: 29821978587							
PROJEKTANT: Design engineer	Patik Kovač, mag.ing.el.techn.inf.	GRADJEVINA I ARHITEKTURA I PROSTORNI DIZAJN HE SENJ	PROJEKTIRANI DIO: Scope of design	ELEKTROTEHNIČKI PROJEKT					
IZRAĐIO: Drazen	Luka Božićević, mag.ing.el.	RAZINA STRUKA: Drazen tipa	IZVODENI PROJEKT						
KONTROLIRAO: Član	Patik Kovač, mag.ing.el.techn.inf.	SADRŽAJ: Članak	DISPOZICIJA ELEKTRO OPREME SUSTAVA RASHLADNE - KOTA +7.03						
GLAVNI PROJEKTANT: Design manager	Natko Vučković, dipl.ing.el.								
MJESTO I DATUM: Place and date	Zagreb, 2026-07-31								
OZNAKA NACRTA Drawing designation	26015-DD-EE-01-201	FORMAT Paper size	MJERILO Scale	ZOP Common part of	PROJEKT Project	MAPA Map	PRILOG Drawing	REVIZIJA Revision	LIST Page
			1:100	Common part of	SEN 1273 - 26015-DD - EE-01	-	201 - 00 -	00 -	1/1