


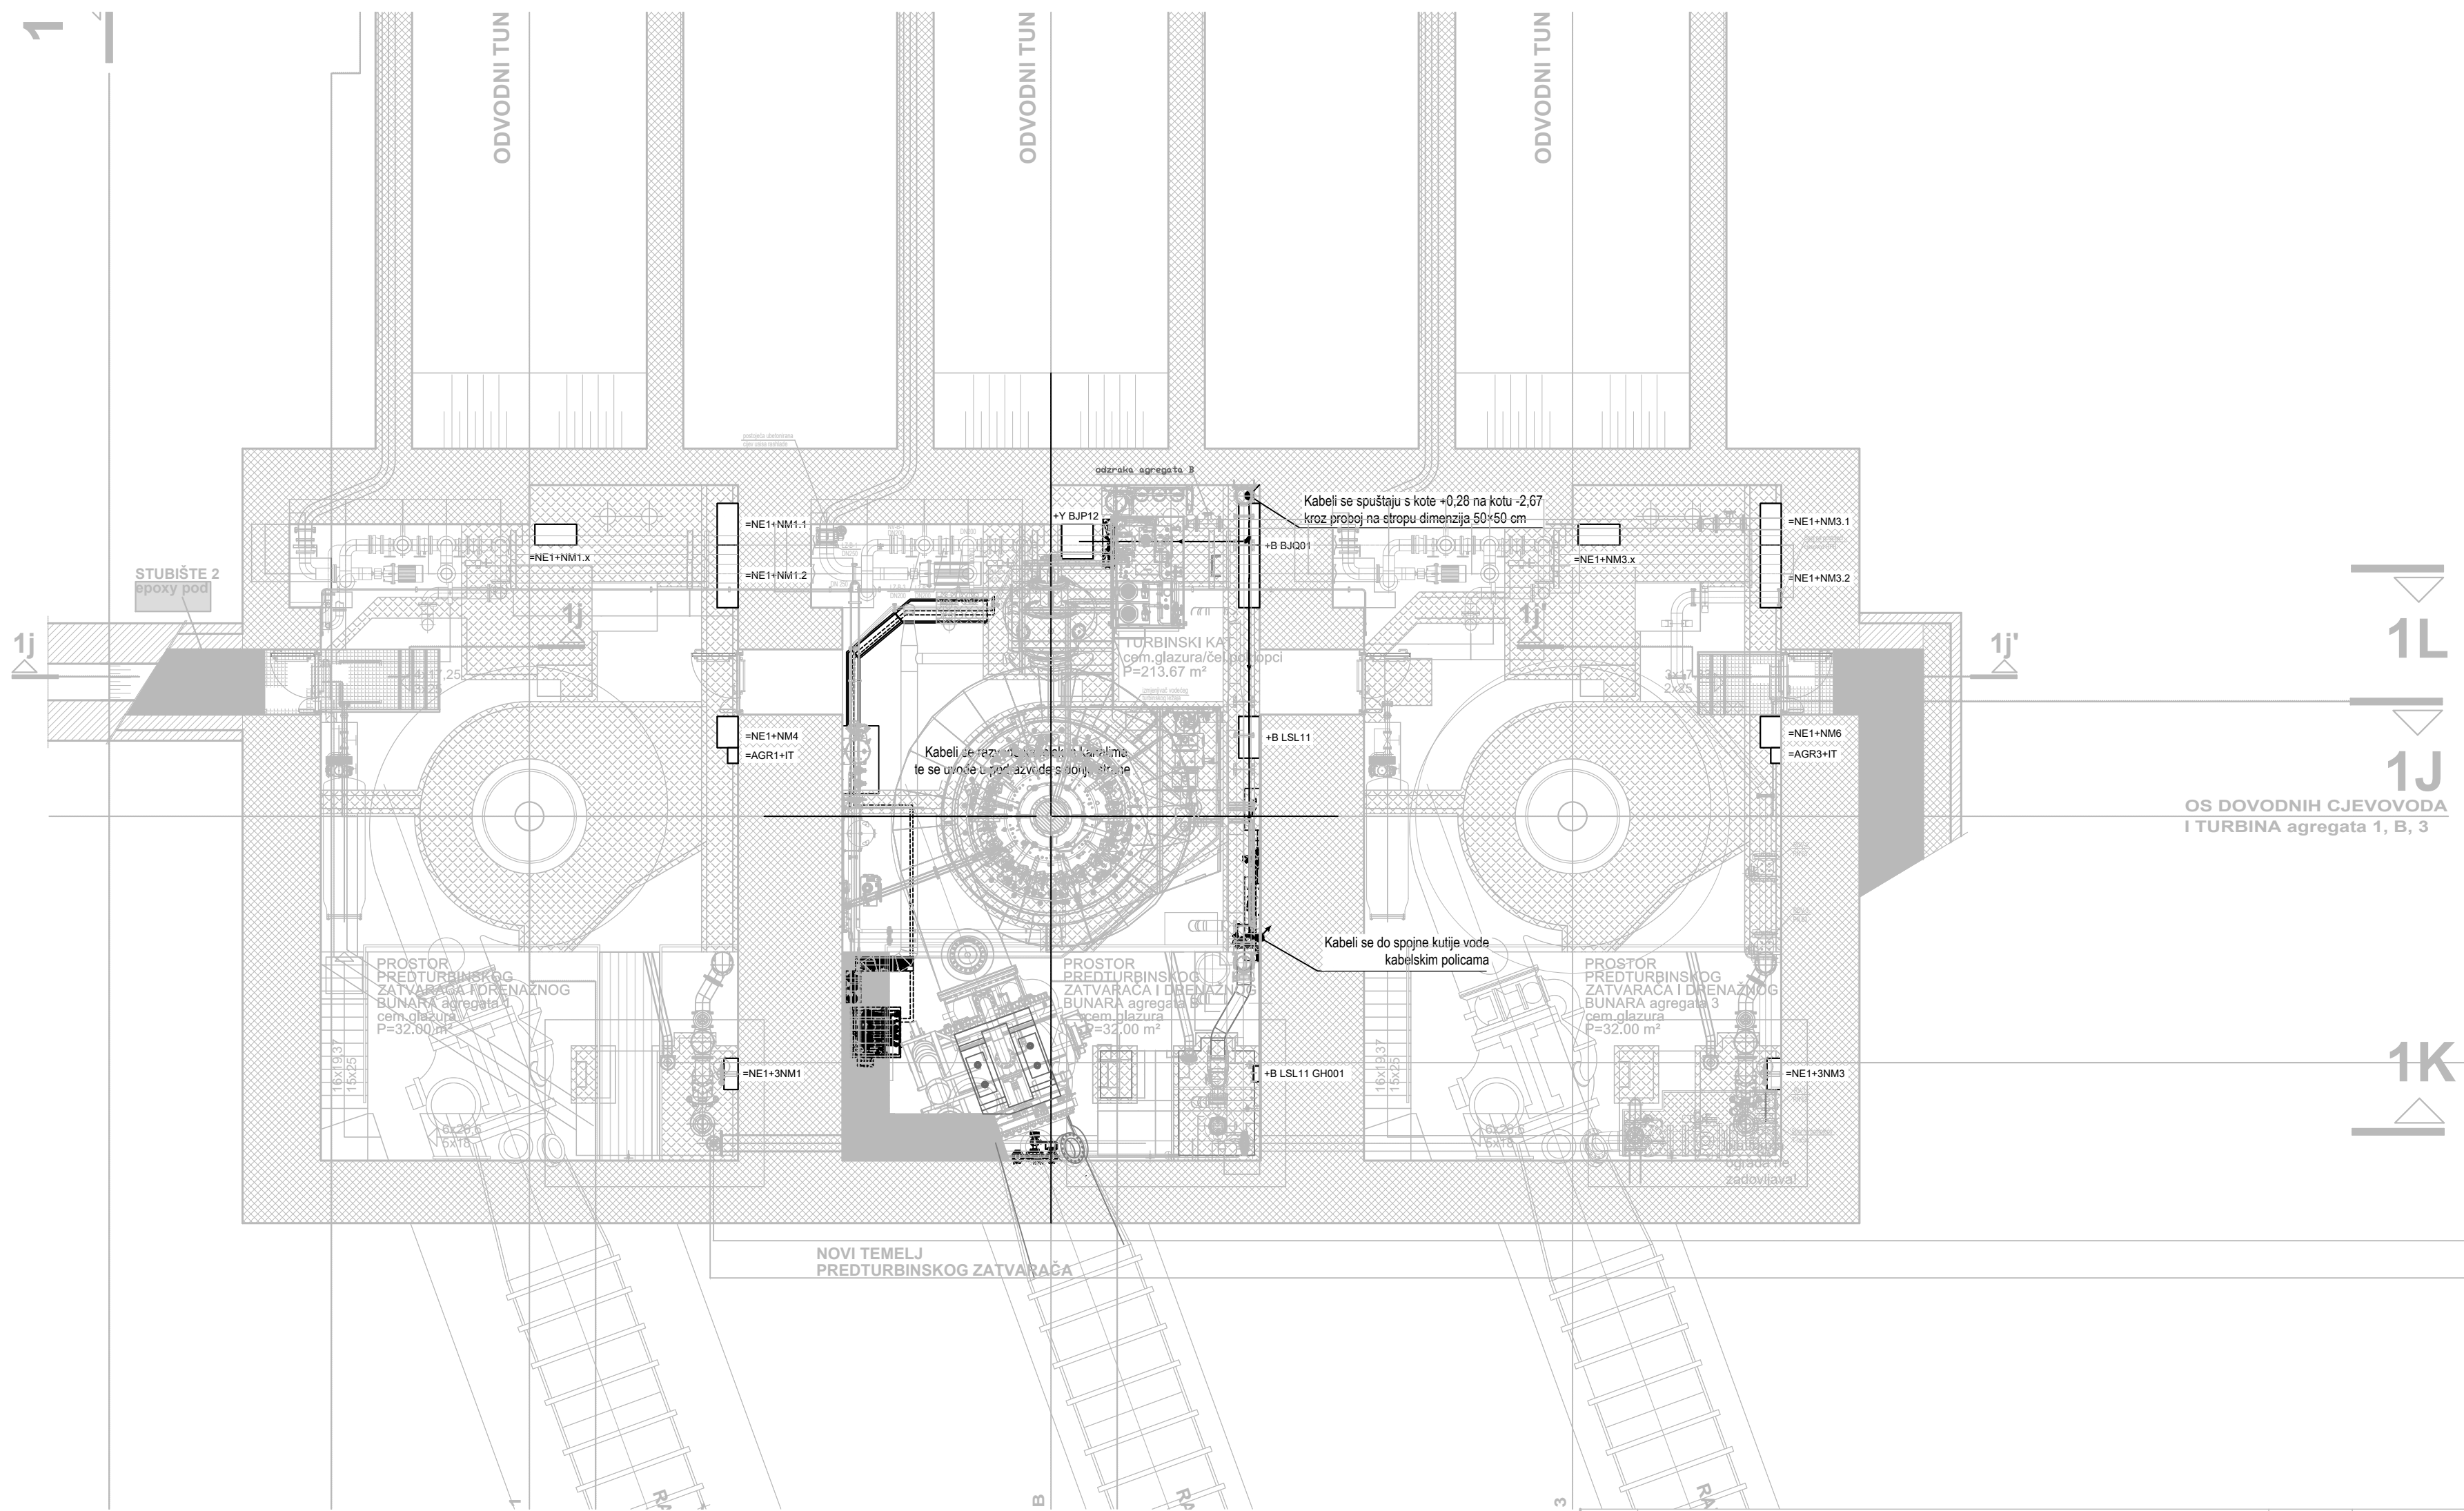

Naziv	Opis
Ormani koji se ugrađuju u fazi I	
+B BUJ01	Ormar pomoćnih pogona generatora i turbine agr. B
+Y BUJ12	Ormar crpnog agregata rashladne vode br. 2
+B LSL11 GH001	Spojna kutija drenažnog bunara B
+B LSL11	Ormar drenaže agregata B
Postojeći ormari	
=NE1+NM1.X	Ormar rashladne vode agregata 1
=NE1+NM1.1	Razvodni ormar pomoćnih pogona agregata 1
=NE1+NM1.2	Ormar pomoćnih pogona agregata 1
=NE1+NM4	Ormar drenaže agregata 1
=AGR1+IT	Ormar turbinskog razdjelnika agregata 1
=NE1+3NM1	Ormar mjerjenja razine vode drenažnog bazena 1
=NE1+NM3.X	Ormar rashladne vode agregata 3
=NE1+NM3.1	Razvodni ormar pomoćnih pogona agregata 3
=NE1+NM3.2	Ormar pomoćnih pogona agregata 3
=NE1+NM6	Ormar drenaže agregata 3
=AGR3+IT	Ormar turbinskog razdjelnika agregata 3
=NE1+3NM3	Ormar mjerjenja razine vode drenažnog bazena 3

LEGENDA:

- Vertikalna kabelska trasa - kabeli se spuštaju na nižu kotu
- Vertikalna kabelska trasa - kabeli se podižu na višu kotu
- Kabelska trasa

SINTAKSA A Volt Company	Sintaksa d.o.o. Ulica Domovinskog rata 104C, 21 000 Split T: +385 1 2330 273 info@sintaksa.hr www.sintaksa.hr	POSLOVA Projekt / job name INVESTITOR PODODJELJENJE ZAHTJEVA INVESTICIONER GRADJEVINAR ZAHVAT U PROSTORU PROJEKTIRANI DIO RAZINA-STRUKA SADRŽAJ DISPOZICIJA ELEKTRO OPREME SUSTAVA RASHLADE - KOTA -2.67	REKONSTRUKCIJA HE SENJ - FAZA I HRVATSKA ELEKTROPRIVREDA d.o.o Ulica grada Vukovara 37, 10000 Zagreb, OIB: 28921978587
PROJEKTANT: Design engineer	Patrik Kovač, mag.ing.el.techn.inf.	GRADJEVINAR ZAHVAT U PROSTORU PROJEKTIRANI DIO RAZINA-STRUKA SADRŽAJ DISPOZICIJA ELEKTRO OPREME SUSTAVA RASHLADE - KOTA -2.67	HE SENJ
IZRADIO: Drawn	Luka Božićević, mag.ing.el.	PROJEKTIRANI DIO RAZINA-STRUKA SADRŽAJ DISPOZICIJA ELEKTRO OPREME SUSTAVA RASHLADE - KOTA -2.67	ELEKTROTEHNIČKI PROJEKT
KONTROLIRAO: Checked	Patrik Kovač, mag.ing.el.techn.inf.	PROJEKTIRANI DIO RAZINA-STRUKA SADRŽAJ DISPOZICIJA ELEKTRO OPREME SUSTAVA RASHLADE - KOTA -2.67	IZVEDBENI PROJEKT
GLAVNI PROJEKTANT: Design manager	Natko Vučković, dipl.ing.el.	PROJEKTIRANI DIO RAZINA-STRUKA SADRŽAJ DISPOZICIJA ELEKTRO OPREME SUSTAVA RASHLADE - KOTA -2.67	
MJESTO I DATUM: Place and date	Zagreb, 2026-07-31	PROJEKTIRANI DIO RAZINA-STRUKA SADRŽAJ DISPOZICIJA ELEKTRO OPREME SUSTAVA RASHLADE - KOTA -2.67	
REV. Rev	00 Radna verzija	2026-07-31	Luka Božićević
NAPOMENA Note			
DATUM Date			
IZRADIO Drawn			
OZNAKA NACRTA Drawing designation			
26015-DD-EE-01-201			
FORMAT Paper size			
1:100			
MJEŠTO Scale			
SEN-1273 - 26015-DD - EE-01 - 201 - 00 - 1/1			