



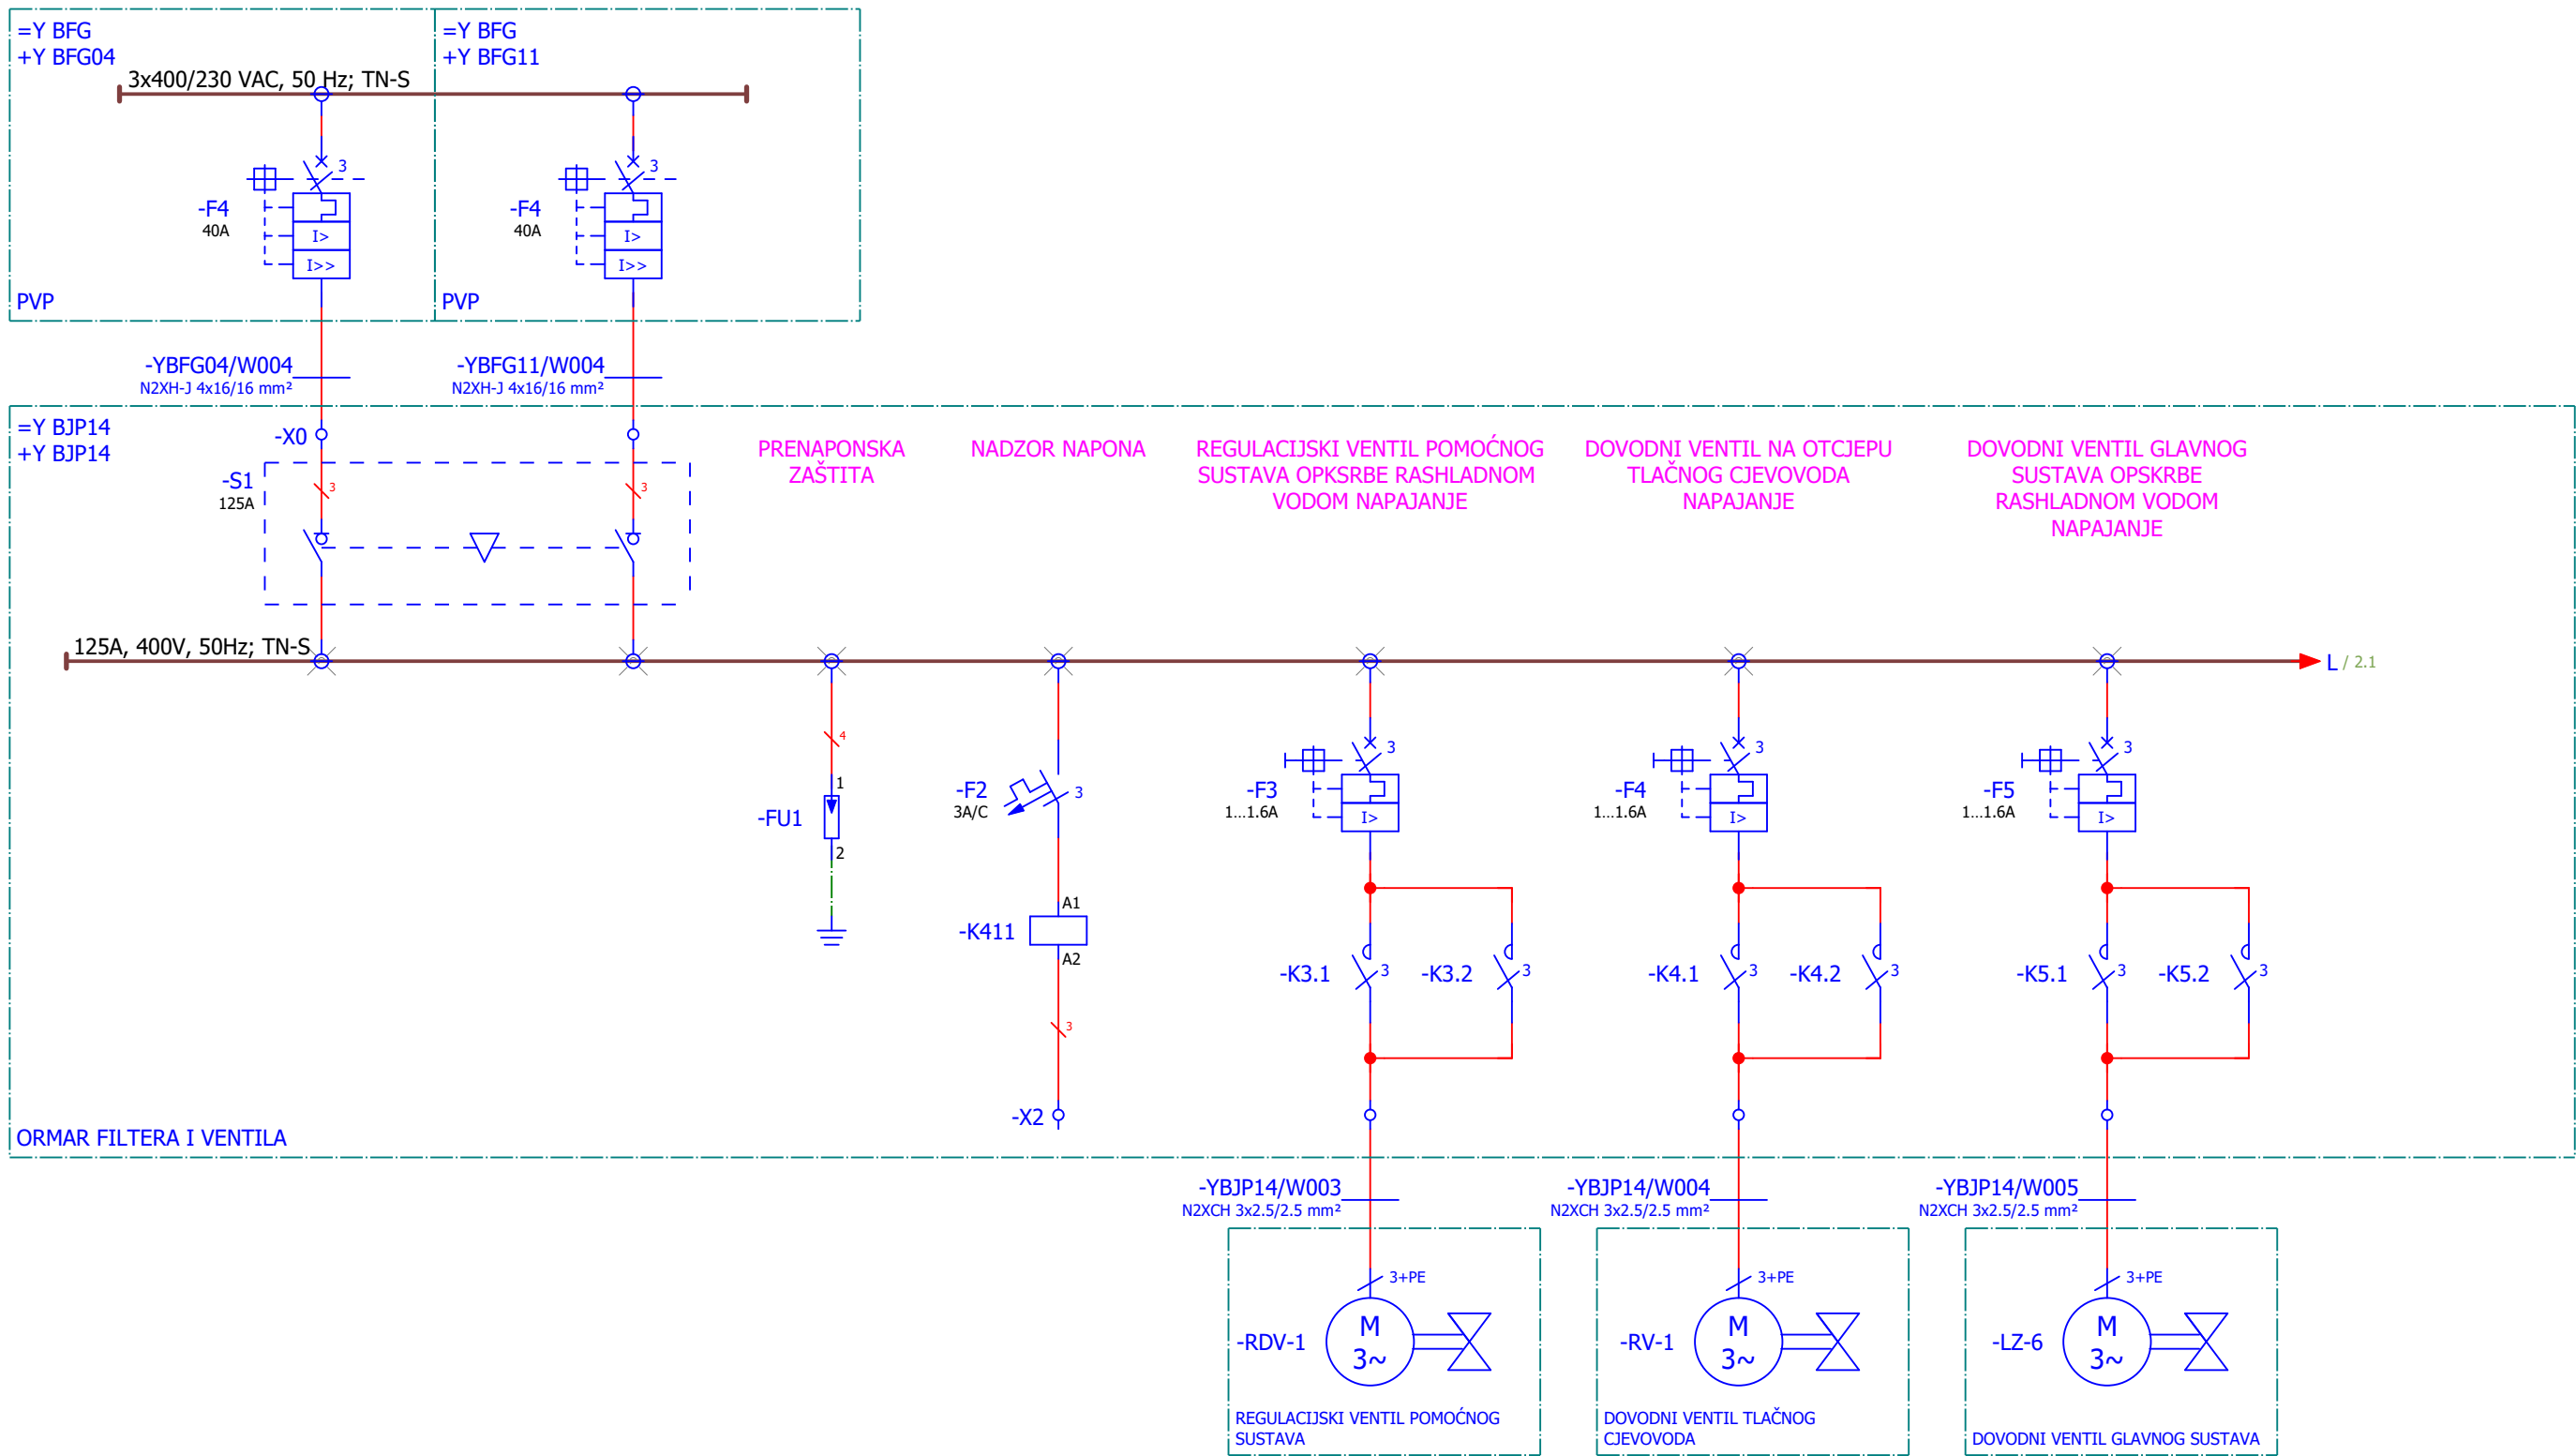


00	Radna verzija	2026-07-31	Tamara Trogrlić
REV. Rev.	NAPOMENA Note	DATUM Date	IZRADIO Drawn

SINTAKSA A Voith Company		Sintaksa d.o.o. Ulica Domovinskog rata 104C, 21 000 Split, Tuškanova 37, 10000 Zagreb T: +385 1 2310 273 info@sintaksa.hr www.sintaksa.hr		NAZIV PROJEKTA / POSLA: Project / job name		REKONSTRUKCIJA HE SENJ - FAZA I.	
PROJEKTANT: Design engineer		Patrik Kovač, mag. ing. el. techn. inf.		INVESTITOR / PODNOŠITELJ ZAHTEVA: Investor		HRVATSKA ELEKTROPRIVREDA d.o.o Ulica grada Vukovara 37, 10000 Zagreb, OIB: 28921978587	
IZRADIO: Drawn		Tamara Trogrlić, mag. ing. el. techn. inf.		GRAĐEVINA / ZAHVAT U PROSTORU: Object		HE Senj Na katastarskim česticama k.o. Sveti Juraj, k.o. Melnice i k.o. Brlog	
KONTROLIRAO: Checked		Patrik Kovač, mag. ing. el. techn. inf.		PROJEKTIRANI DIO: Scope of design		STROJARSKI PROJEKT	
GLAVNI PROJEKTANT: Design manager		Natko Vučković, dipl.ing.el.		RAZINA-STRUKA: Design type		IZVEDBENI PROJEKT	
MJESTO I DATUM: Place and date		Zagreb, 2026-07-31		SADRŽAJ: Content		JEDNOPOLNA SHEMA	
OZNAKA NACRTA Drawing designation		FORMAT Paper size		MJERILO Scale		ZOP Com. pr. des.	PROJEKT Project
26015-DD-EE-01-101-00		A3		1:10		MAPA Folder	PRIOLOG Drawing
						REVIZIJA Revision	LIST Page
						SEN.1273 — 26015 — 1E12-3 — 101 — 00 —	1 / 7

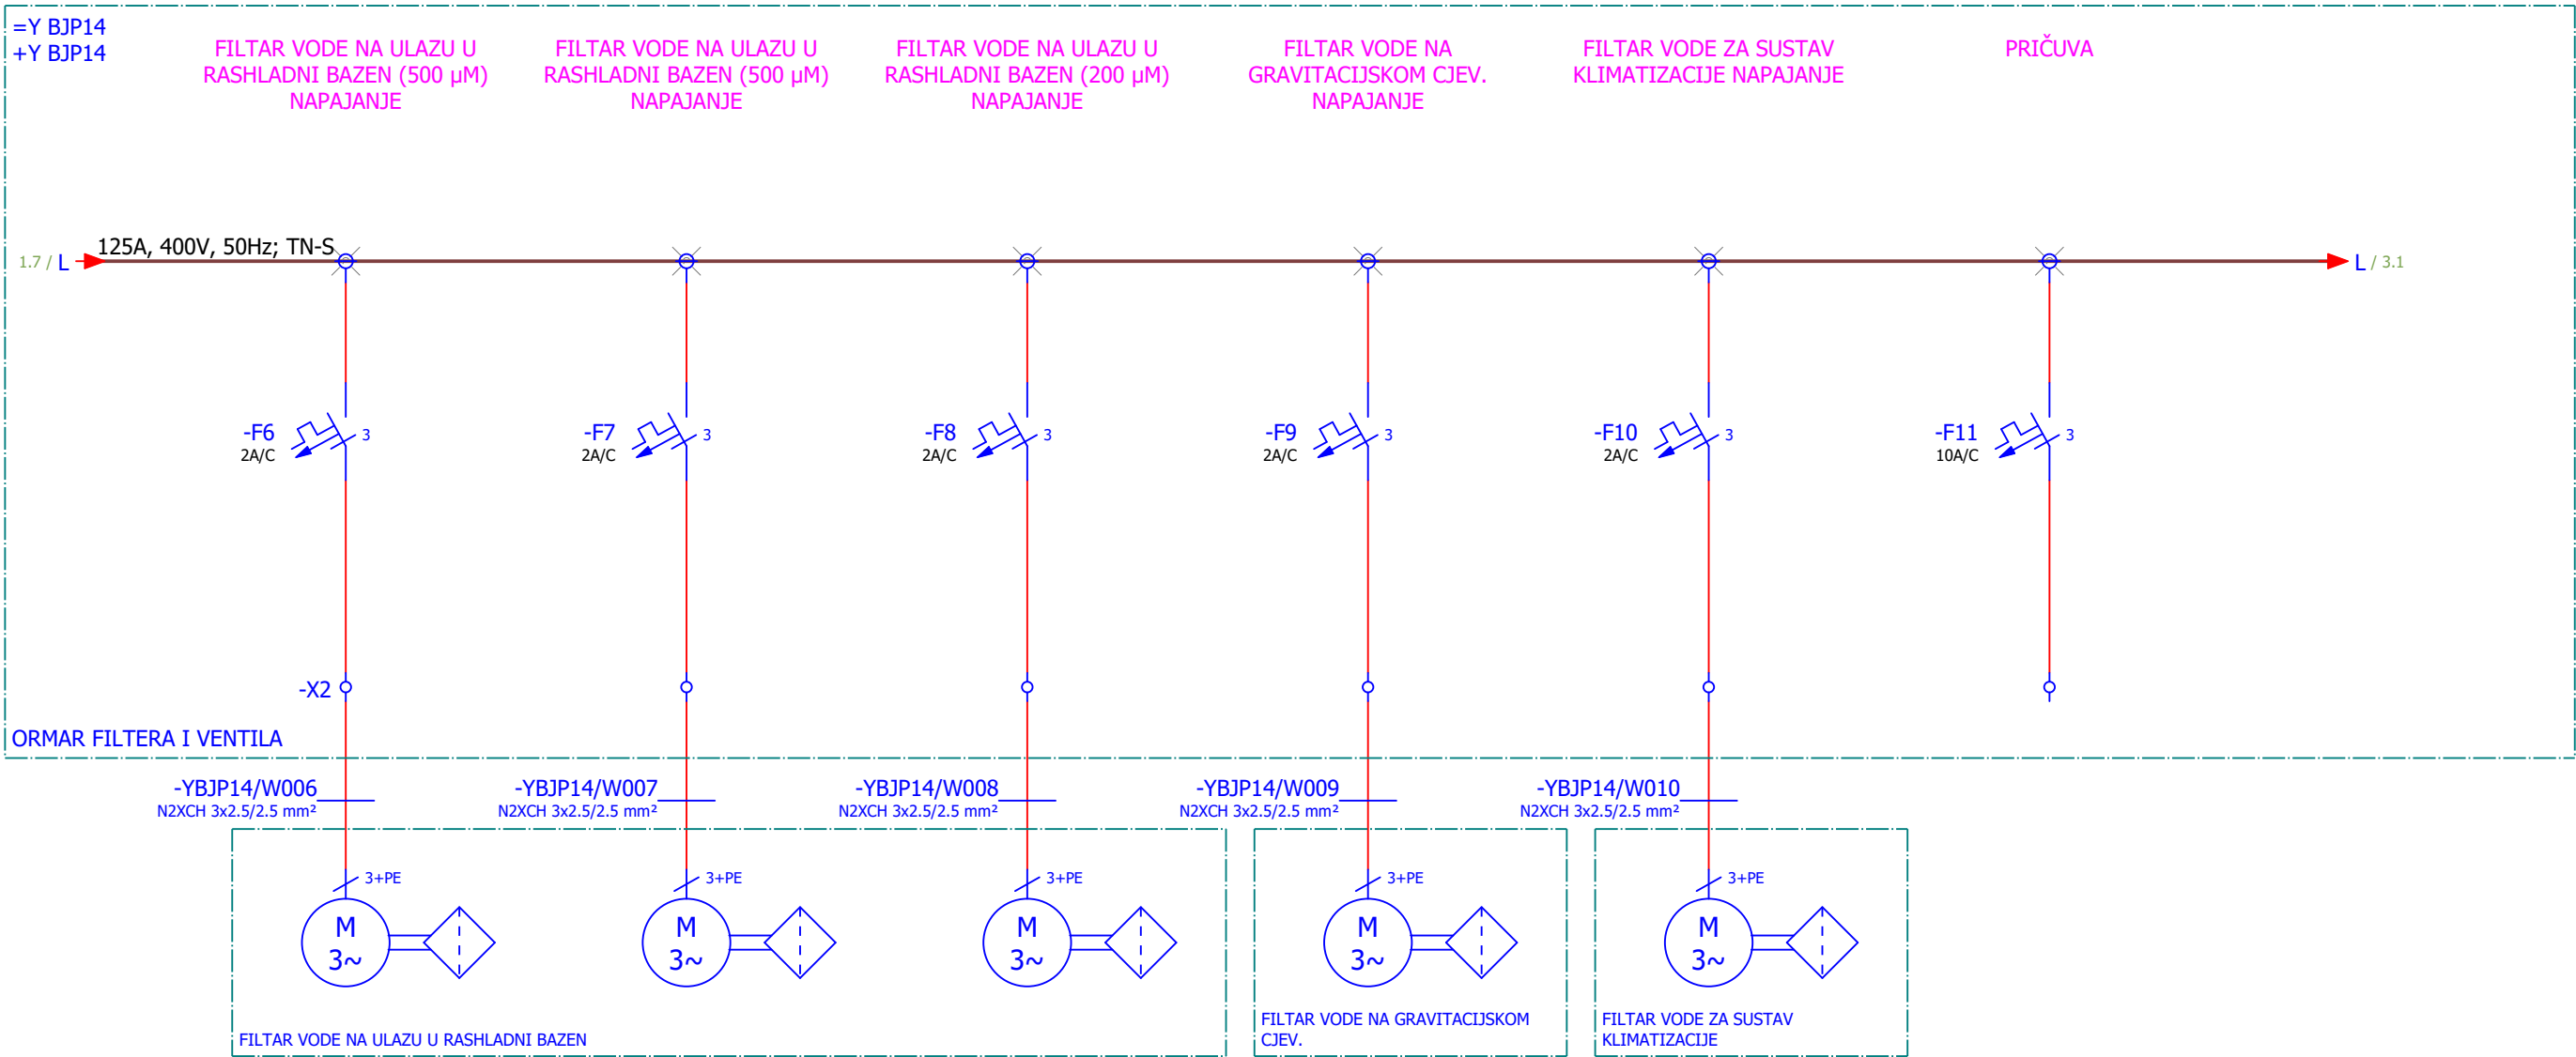


00	Radna verzija	2026-07-31	Tamara Trogrlić
REV. Rev.	NAPOMENA Note	DATUM Date	IZRADIO Drawn

 SINTAKSA A Voith Company Sintaksa d.o.o. Ulica Domovinskog rata 104C, 21 000 Split, Tuškanova 37, 10000 Zagreb T: +385 1 2310 273 info@sintaksa.hr www.sintaksa.hr			NAZIV PROJEKTA / POSLA: <i>Project / job name</i>		REKONSTRUKCIJA HE SENJ - FAZA I.																			
PROJEKTANT: <i>Design engineer</i>			Patrik Kovač, mag. ing. el. techn. inf.		INVESTITOR / PODNOŠITELJ ZAHTEJVA: <i>Investor</i>			HRVATSKA ELEKTROPRIVREDA d.o.o Ulica grada Vukovara 37, 10000 Zagreb, OIB: 28921978587																
IZRADIO: <i>Drawn</i>			Tamara Troglić, mag. ing. el. techn. inf.		GRAĐEVINA / ZAHVAT U PROSTORU: <i>Object</i>			HE Senj Na katastarskim česticama k.o. Sveti Juraj, k.o. Melnice i k.o. Brlog																
KONTROLIRAO: <i>Checked</i>			Patrik Kovač, mag. ing. el. techn. inf.		PROJEKTIRANI DIO: <i>Scope of design</i>			STROJARSKI PROJEKT																
GLAVNI PROJEKTANT: <i>Design manager</i>			Natko Vučković, dipl.ing.el.		RAZINA-STRUKA: <i>Design type</i>			IZVEDBENI PROJEKT																
MJESTO I DATUM: <i>Place and date</i>			Zagreb, 2026-07-31		SADRŽAJ: <i>Content</i>			JEDNOPOLNA SHEMA																
OZNAKA NACRTA <i>Drawing designation</i>			FORMAT <i>Paper size</i>		MJERILO <i>Scale</i>																			
26015-DD-EE-01-101-00			A3		1:10		ZOP <i>Com. pr. des.</i>			PROJEKT <i>Project</i>			MAPA <i>Folder</i>			PRILOG <i>Drawing</i>			REVIZIJA <i>Revision</i>			LIST <i>Page</i>		
							SEN.1273 —			26015 —			1E12-3 —			101 —			00 —			2 / 7		

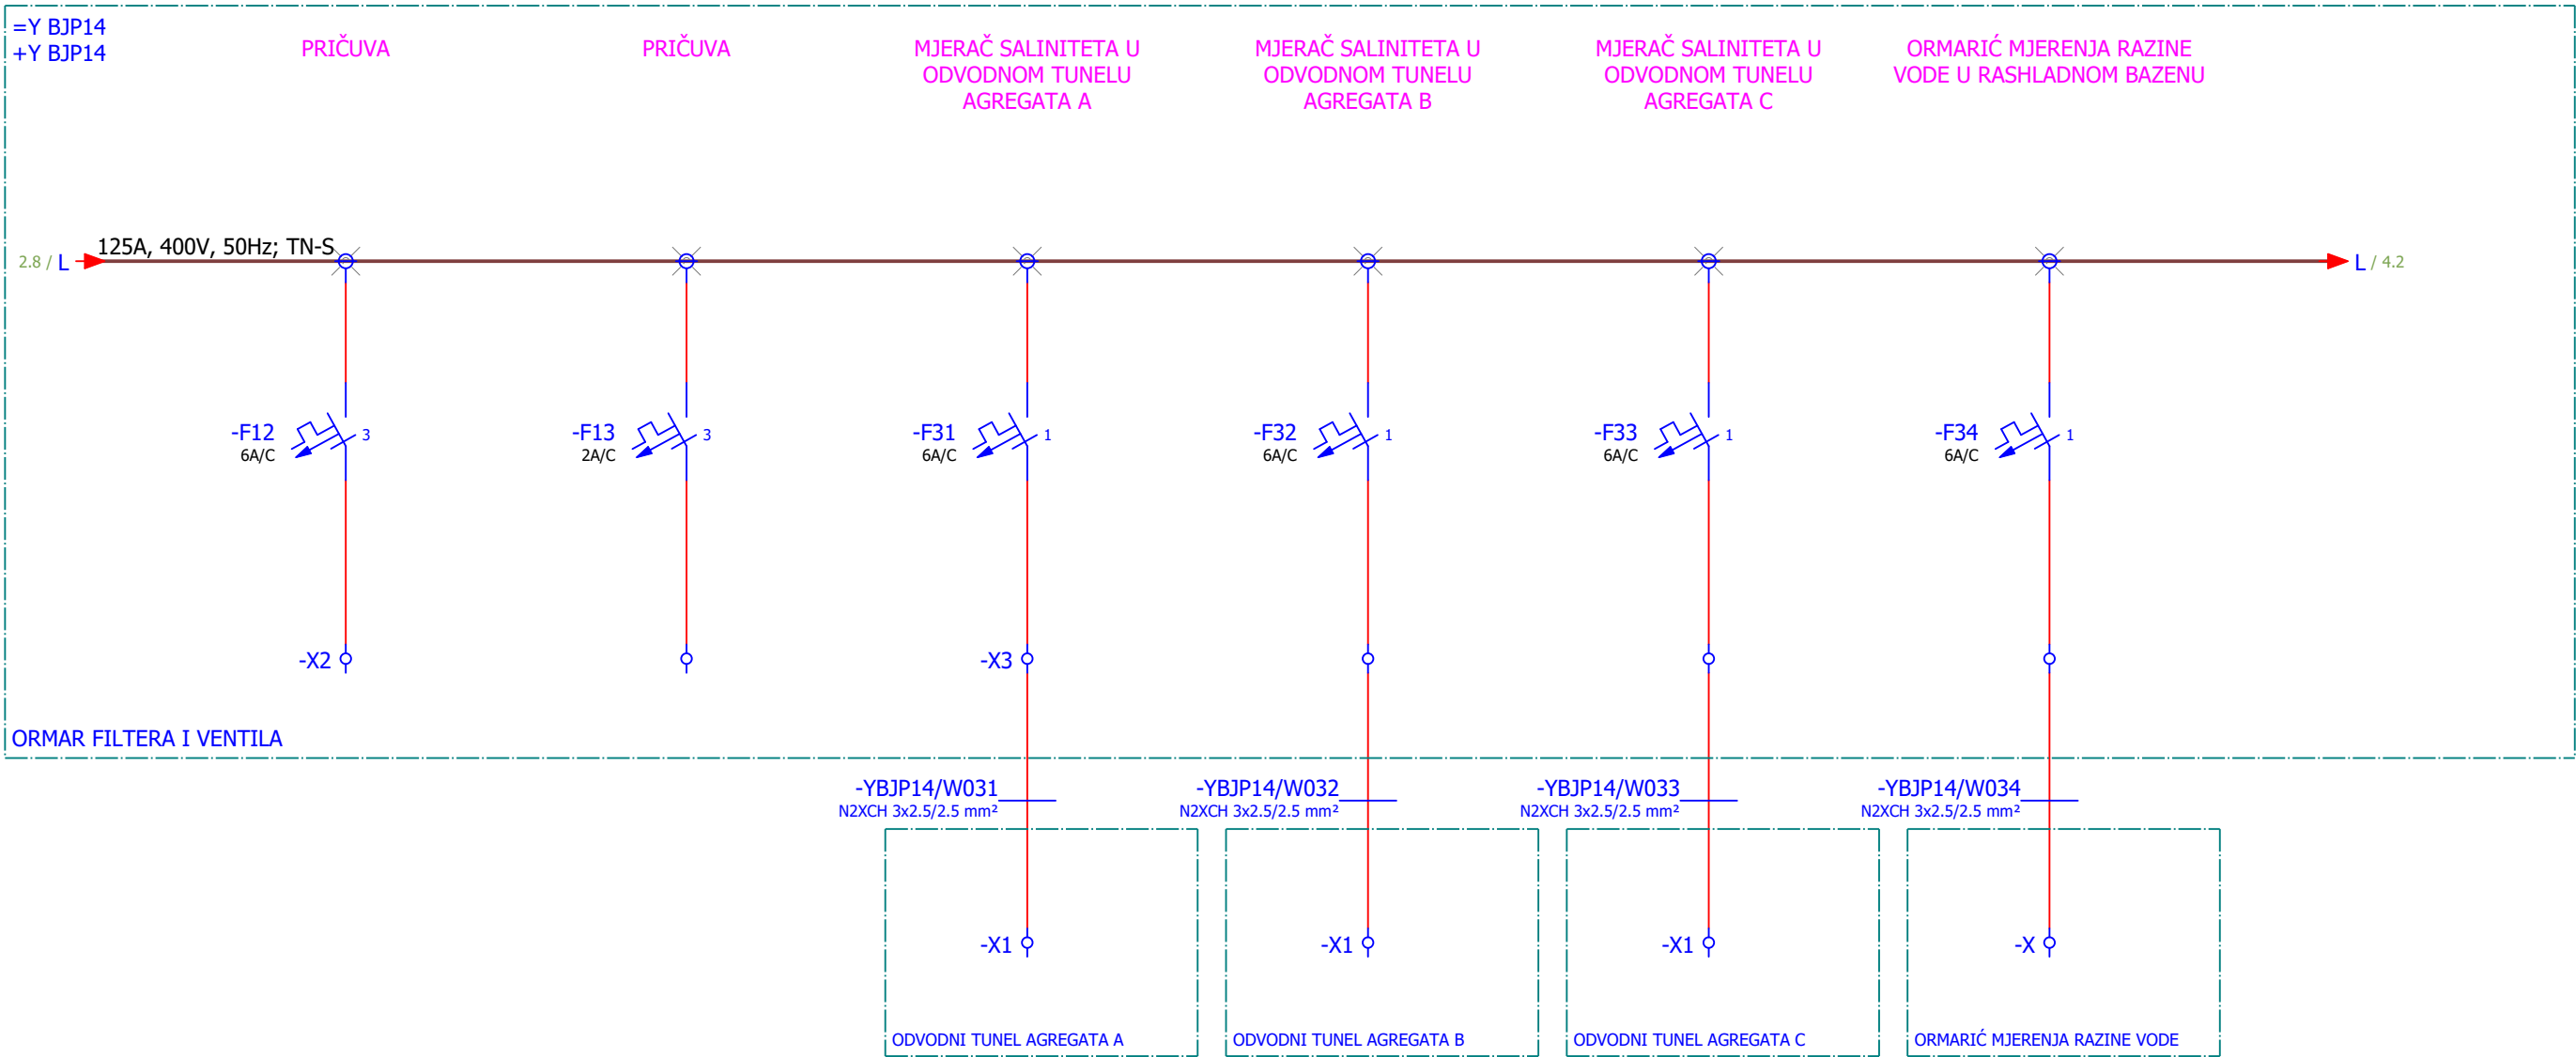


00	Radna verzija	2026-07-31	Tamara Trogrlić
REV. Rev.	NAPOMENA Note	DATUM Date	IZRADIO Drawn

 SINTAKSA A Voith Company Sintaksa d.o.o. Ulica Domovinskog rata 104C, 21 000 Split, Tuškanova 37, 10000 Zagreb T: +385 1 2310 273 info@sintaksa.hr www.sintaksa.hr			NAZIV PROJEKTA / POSLA: <i>Project / job name</i> REKONSTRUKCIJA HE SENJ - FAZA I.					
PROJEKTANT: <i>Design engineer</i> Patrik Kovač, mag. ing. el. techn. inf.			INVESTITOR / PODNOŠITELJ ZAHTEVA: <i>Investor</i> HRVATSKA ELEKTROPRIVREDA d.o.o Ulica grada Vukovara 37, 10000 Zagreb, OIB: 28921978587					
IZRADIO: <i>Drawn</i> Tamara Trogrlić, mag. ing. el. techn. inf.			GRADJEVINA / ZAHVAT U PROSTORU: <i>Object</i> HE Senj Na katastarskim česticama k.o. Sveti Juraj, k.o. Melnice i k.o. Brlog					
KONTROLIRAO: <i>Checked</i> Patrik Kovač, mag. ing. el. techn. inf.			PROJEKTIRANI DIO: <i>Scope of design</i> STROJARSKI PROJEKT					
GLAVNI PROJEKTANT: <i>Design manager</i> Natko Vučković, dipl.ing.el.			RAZINA-STRUKA: <i>Design type</i> IZVEDBENI PROJEKT					
MJESTO I DATUM: <i>Place and date</i> Zagreb, 2026-07-31			SADRŽAJ: <i>Content</i> JEDNOPOLNA SHEMA					
OZNAKA NACRTA <i>Drawing designation</i> 26015-DD-EE-01-101-00	FORMAT <i>Paper size</i> A3	MJERILO <i>Scale</i> 1:10	ZOP <i>Com. pr. des.</i> SEN.1273	PROJEKT <i>Project</i> 26015	MAPA <i>Folder</i> 1E12-3	PRILOG <i>Drawing</i> 101	REVIZIJA <i>Revision</i> 00	LIST <i>Page</i> 3 / 7

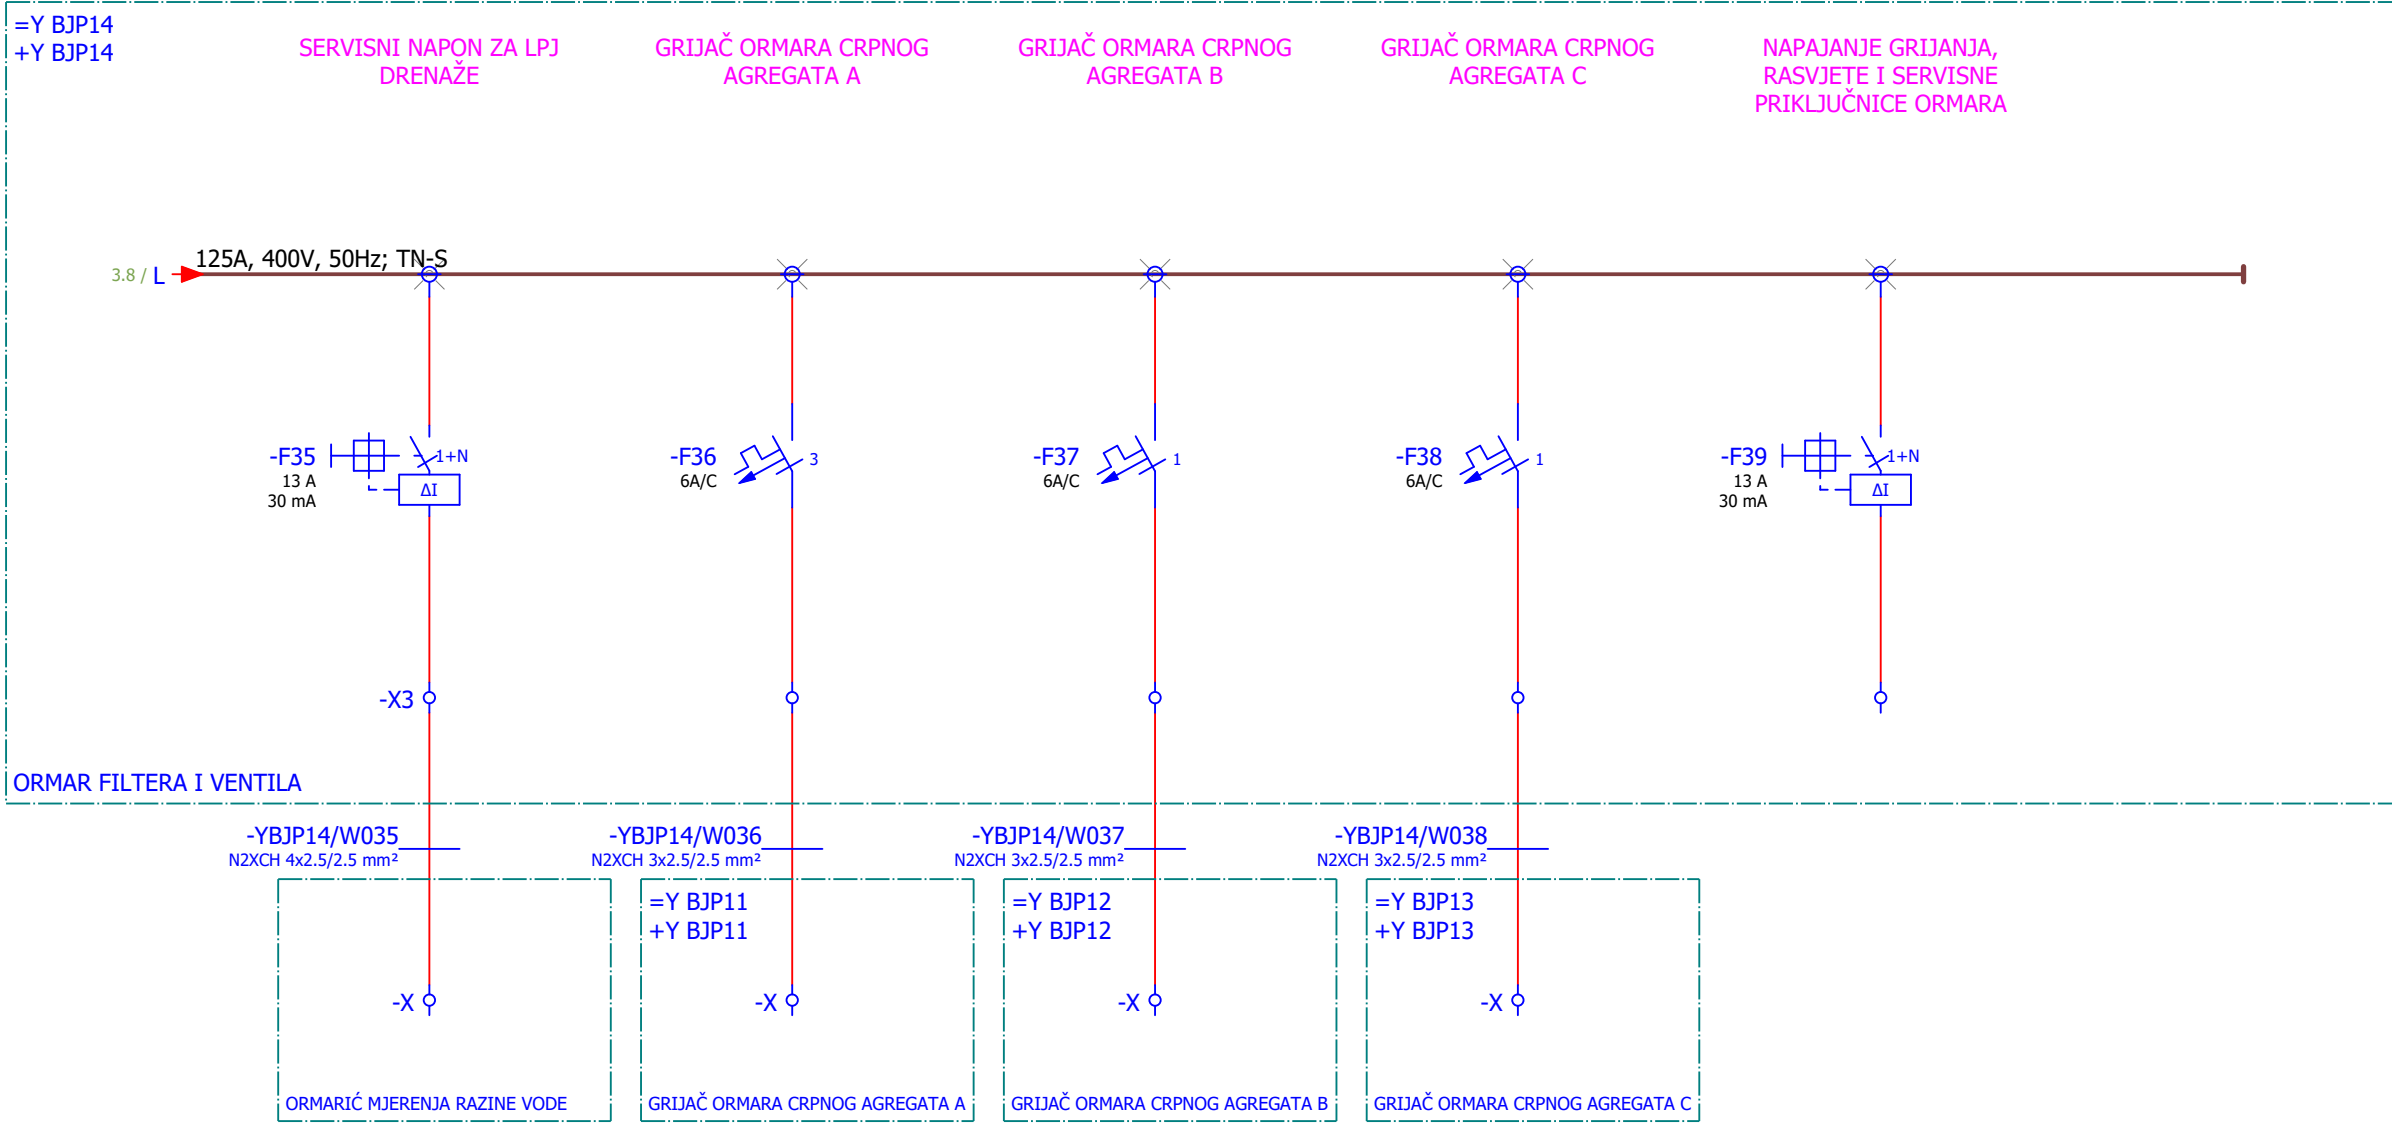


00	Radna verzija	2026-07-31	Tamara Trogrlić
REV. Rev.	NAPOMENA Note	DATUM Date	IZRADIO Drawn

SINTAKSA A Voith Company			Sintaksa d.o.o. Ulica Domovinskog rata 104C, 21 000 Split, Tuškanova 37, 10000 Zagreb T: +385 1 2310 273 info@sintaksa.hr www.sintaksa.hr			NAZIV PROJEKTA / POSLA: Project / job name						REKONSTRUKCIJA HE SENJ - FAZA I.					
PROJEKTANT: Design engineer Patrik Kovač, mag. ing. el. techn. inf.						INVESTITOR / PODNOŠITELJ ZAHTEVA: Investor			HRVATSKA ELEKTROPRIVREDA d.o.o Ulica grada Vukovara 37, 10000 Zagreb, OIB: 28921978587								
IZRADIO: Drawn Tamara Trogrlić, mag. ing. el. techn. inf.						GRAĐEVINA / ZAHVAT U PROSTORU: Object			HE Senj Na katastarskim česticama k.o. Sveti Juraj, k.o. Melnice i k.o. Brlog								
KONTROLIRAO: Checked Patrik Kovač, mag. ing. el. techn. inf.						PROJEKTIRANI DIO: Scope of design			STROJARSKI PROJEKT								
GLAVNI PROJEKTANT: Design manager Natko Vučković, dipl.ing.el.						RAZINA-STRUKA: Design type			IZVEDBENI PROJEKT								
MJESTO I DATUM: Place and date Zagreb, 2026-07-31						SADRŽAJ: Content			JEDNOPOLNA SHEMA								
OZNAKA NACRTA Drawing designation 26015-DD-EE-01-101-00		FORMAT Paper size A3	MJERILO Scale 1:10	ZOP Com. pr. des. SEN.1273 —		PROJEKT Project 26015 —		MAPA Folder 1E12-3 —	PRILOG Drawing 101 —	REVIZIJA Revision 00 —	LIST Page 4 / 7						

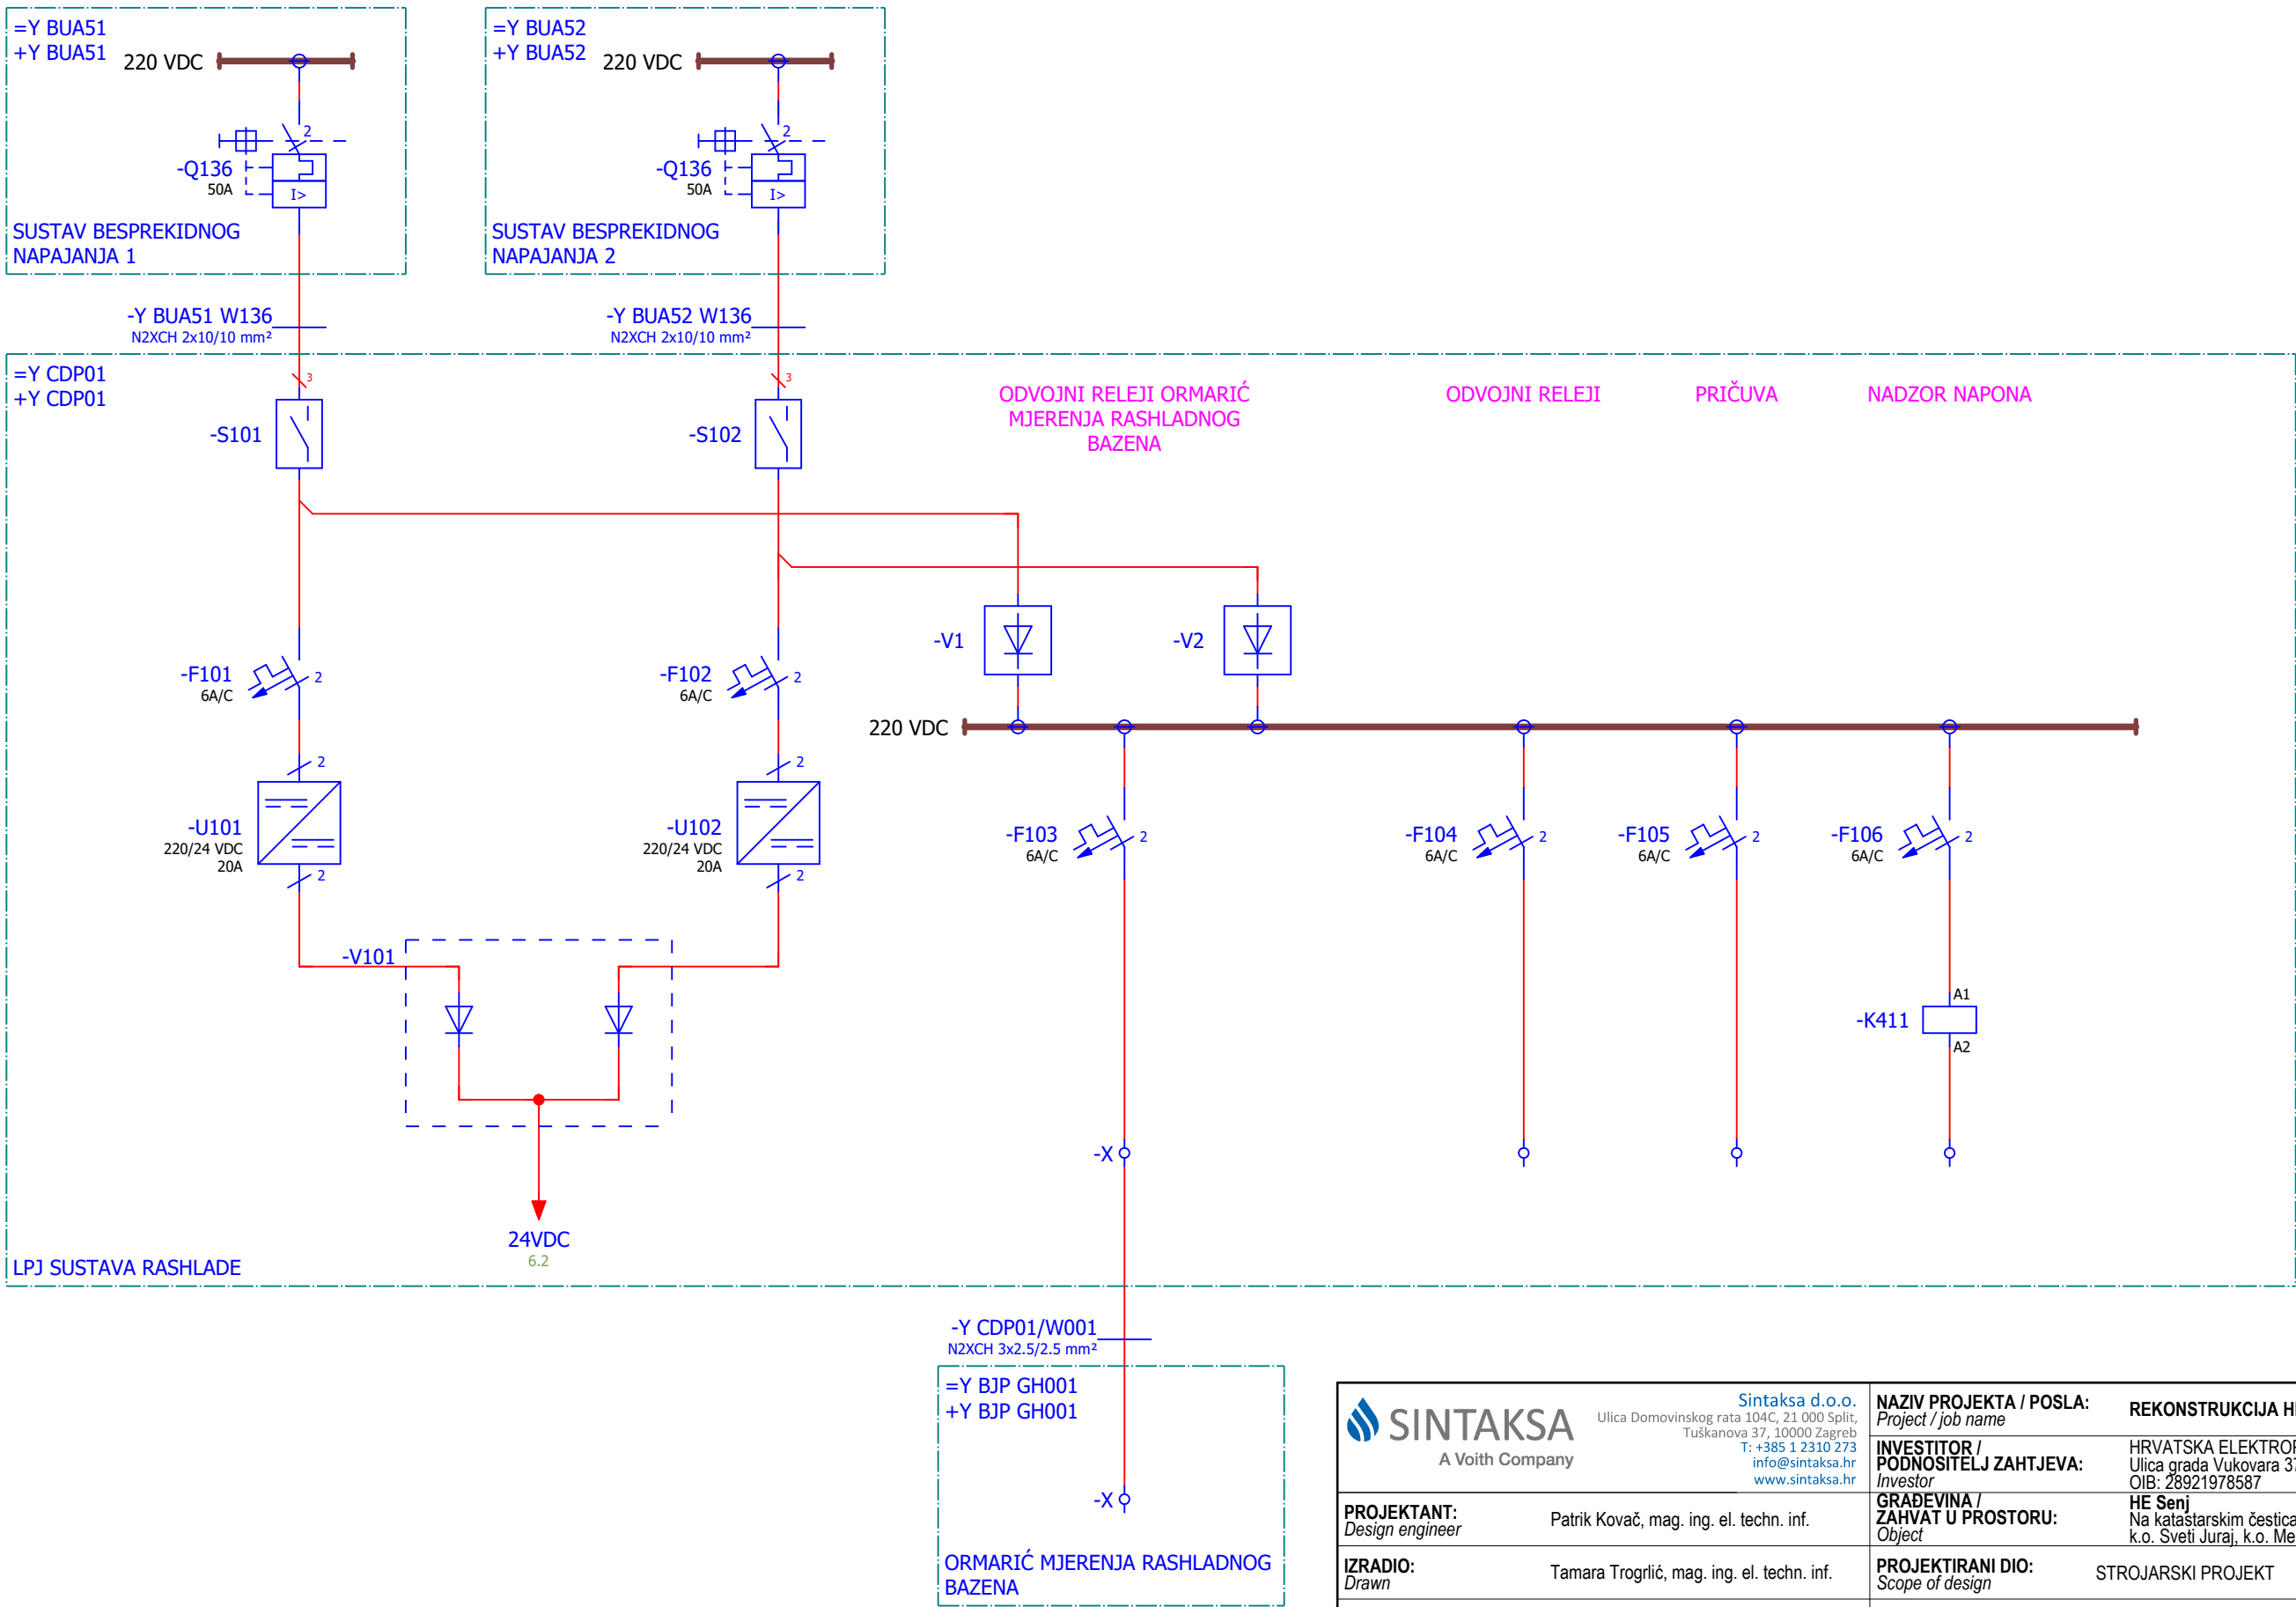


00	Radna verzija	2026-07-31	Tamara Trogrlić
REV. Rev.	NAPOMENA Note	DATUM Date	IZRADIO Drawn

SINTAKSA A Voith Company			NAZIV PROJEKTA / POSLA: Project / job name		REKONSTRUKCIJA HE SENJ - FAZA I.	
Sintaksa d.o.o. Ulica Domovinskog rata 104C, 21 000 Split, Tuškanova 37, 10000 Zagreb T: +385 1 2310 273 info@sintaksa.hr www.sintaksa.hr			INVESTITOR / PODNOŠITELJ ZAHTEVA: Investor		HRVATSKA ELEKTROPRIVREDA d.o.o Ulica grada Vukovara 37, 10000 Zagreb, OIB: 28921978587	
PROJEKTANT: Design engineer			Patrik Kovač, mag. ing. el. techn. inf.		GRAĐEVINA / ZAHVAT U PROSTORU: Object	
IZRADIO: Drawn			Tamara Trogrlić, mag. ing. el. techn. inf.		PROJEKTIRANI DIO: Scope of design	
KONTROLIRAO: Checked			Patrik Kovač, mag. ing. el. techn. inf.		RAZINA-STRUKA: Design type	
GLAVNI PROJEKTANT: Design manager			Natko Vučković, dipl.ing.el.		SADRŽAJ: Content	
MJESTO I DATUM: Place and date			Zagreb, 2026-07-31		JEDNOPOLNA SHEMA	
OZNAKA NACRTA Drawing designation		FORMAT Paper size	MJERILO Scale	ZOP Com. pr. des.	PROJEKT Project	MAPA Folder
26015-DD-EE-01-101-00		A3	1:10	SEN.1273	26015	1E12-3
				PRILOG Drawing	REVIZIJA Revision	LIST Page
				101	00	5 / 7

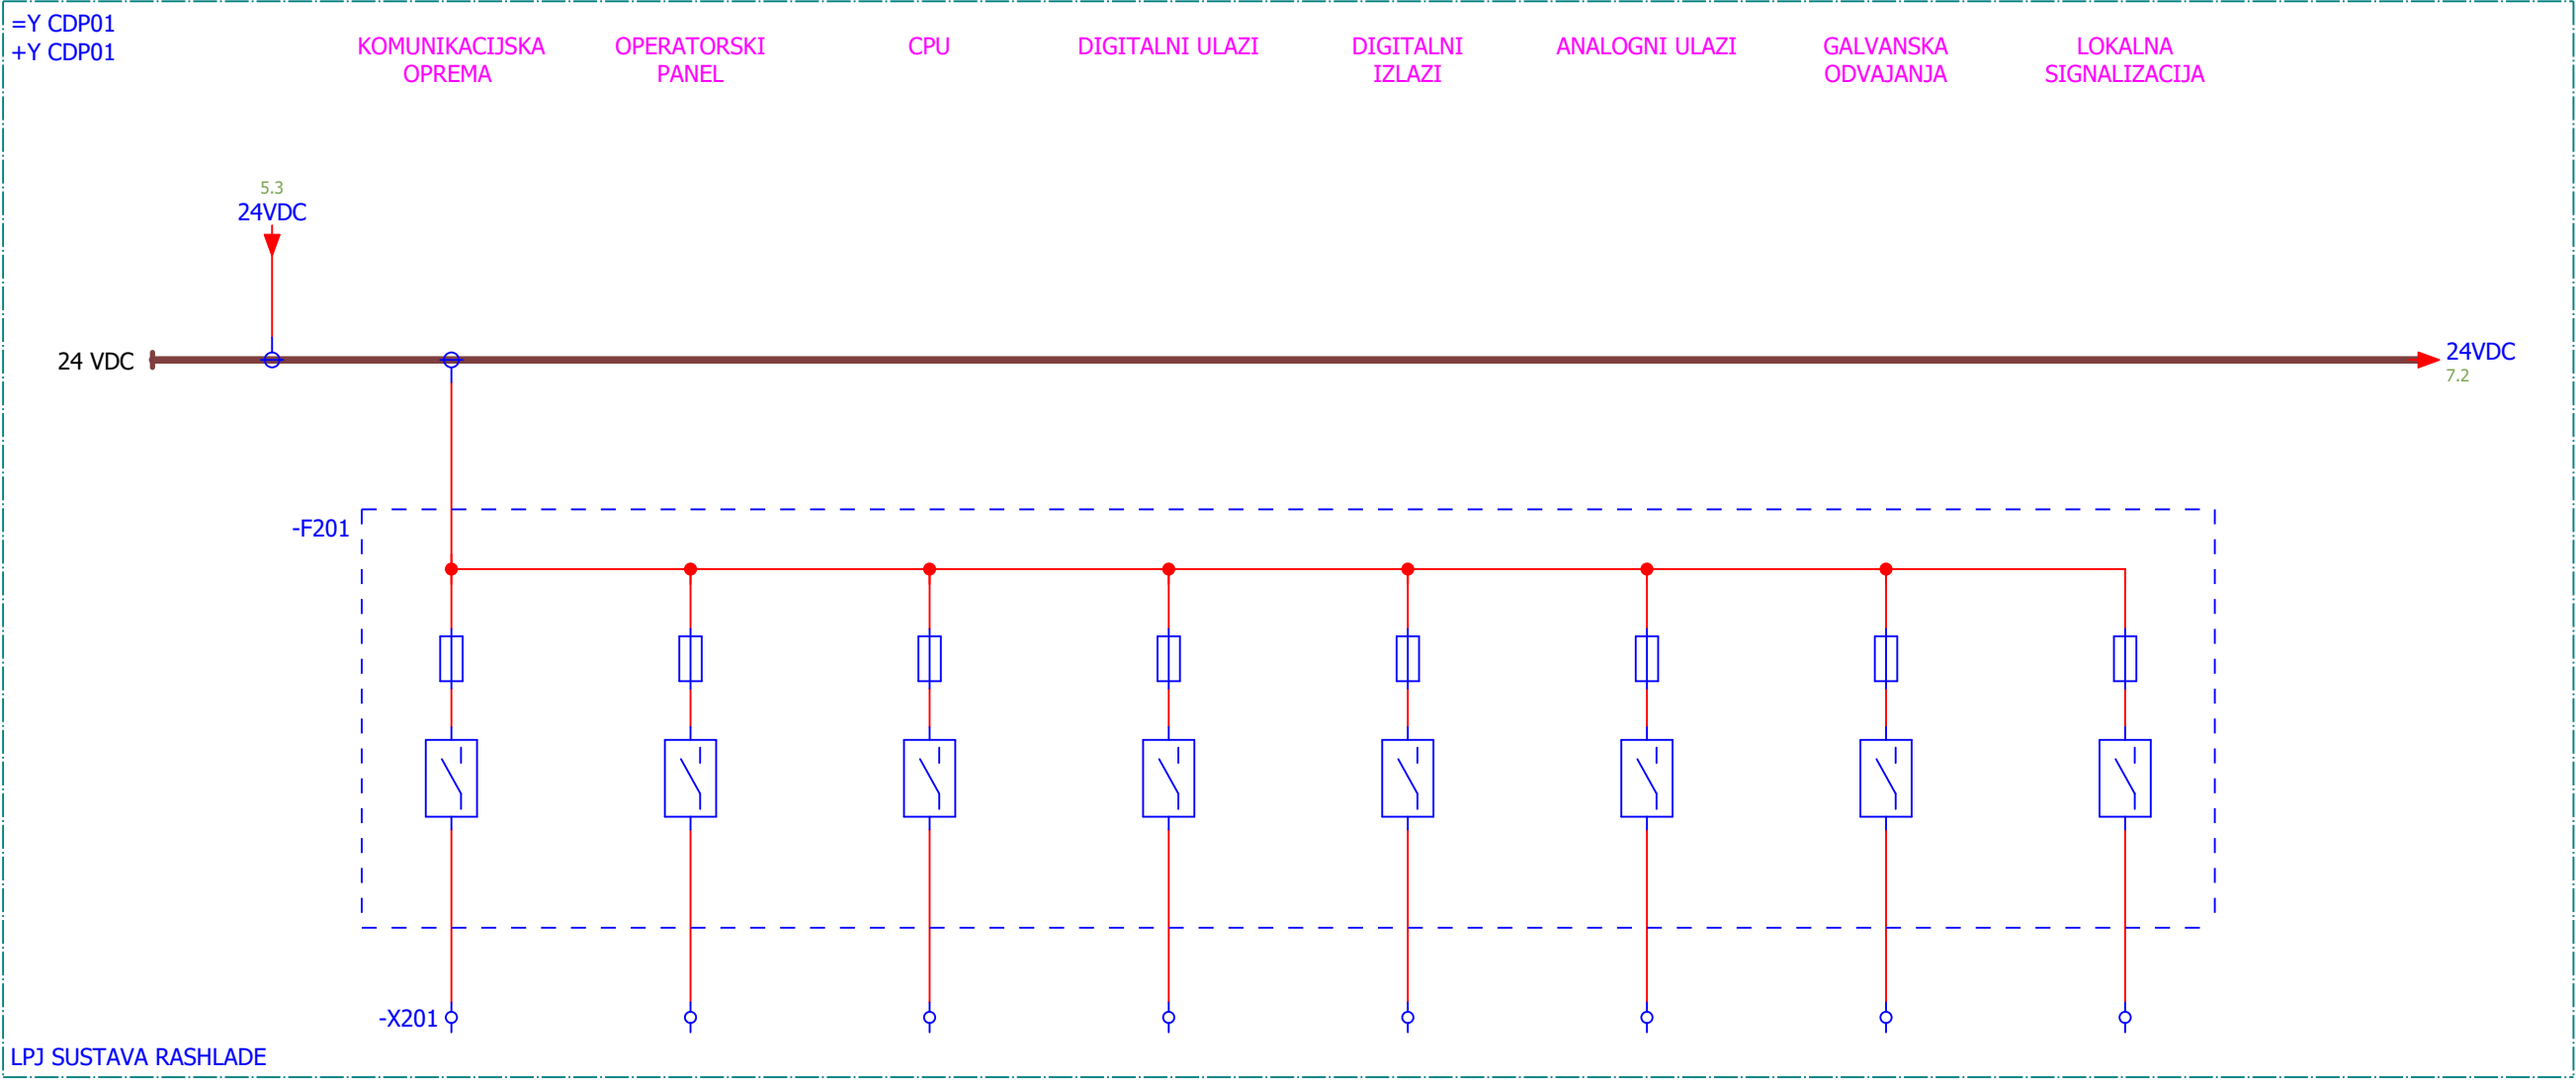

00	Radna verzija	2026-07-31	Tamara Trogrlić
REV. Rev.	NAPOMENA Note	DATUM Date	IZRADIO Drawn

 SINTAKSA A Voith Company Sintaksa d.o.o. Ulica Domovinskog rata 104C, 21 000 Split, Tuškanova 37, 10000 Zagreb T: +385 1 2310 273 info@sintaksa.hr www.sintaksa.hr			NAZIV PROJEKTA / POSLA: <i>Project / job name</i>		REKONSTRUKCIJA HE SENJ - FAZA I.							
PROJEKTANT: <i>Design engineer</i>			Patrik Kovač, mag. ing. el. techn. inf.		INVESTITOR / PODNOŠITELJ ZAHTEVA: <i>Investor</i>							
IZRADIO: <i>Drawn</i>			Tamara Trogrlić, mag. ing. el. techn. inf.		HRVATSKA ELEKTROPRIVREDA d.o.o Ulica grada Vukovara 37, 10000 Zagreb, OIB: 28921978587							
KONTROLIRAO: <i>Checked</i>			Patrik Kovač, mag. ing. el. techn. inf.		HE Senj Na katastarskim česticama k.o. Sveti Juraj, k.o. Melnice i k.o. Brlog							
GLAVNI PROJEKTANT: <i>Design manager</i>			Natko Vučković, dipl.ing.el.		PROJEKTIRANI DIO: <i>Scope of design</i>							
MJESTO I DATUM: <i>Place and date</i>			Zagreb, 2026-07-31		STROJARSKI PROJEKT							
OZNAKA NACRTA <i>Drawing designation</i>			FORMAT <i>Paper size</i>		MJERILO <i>Scale</i>		RAZINA-STRUKA: <i>Design type</i>					
26015-DD-EE-01-101-00			A3		1:10		IZVEDBENI PROJEKT					
SADRŽAJ: <i>Content</i>			JEDNOPOLNA SHEMA									
ZOP <i>Com. pr. des.</i>			PROJEKT <i>Project</i>		MAPA <i>Folder</i>		PRILOG <i>Drawing</i>		REVIZIJA <i>Revision</i>		LIST <i>Page</i>	
SEN.1273 —			26015 —		1E12-3 —		101 —		00 —		6 / 7	

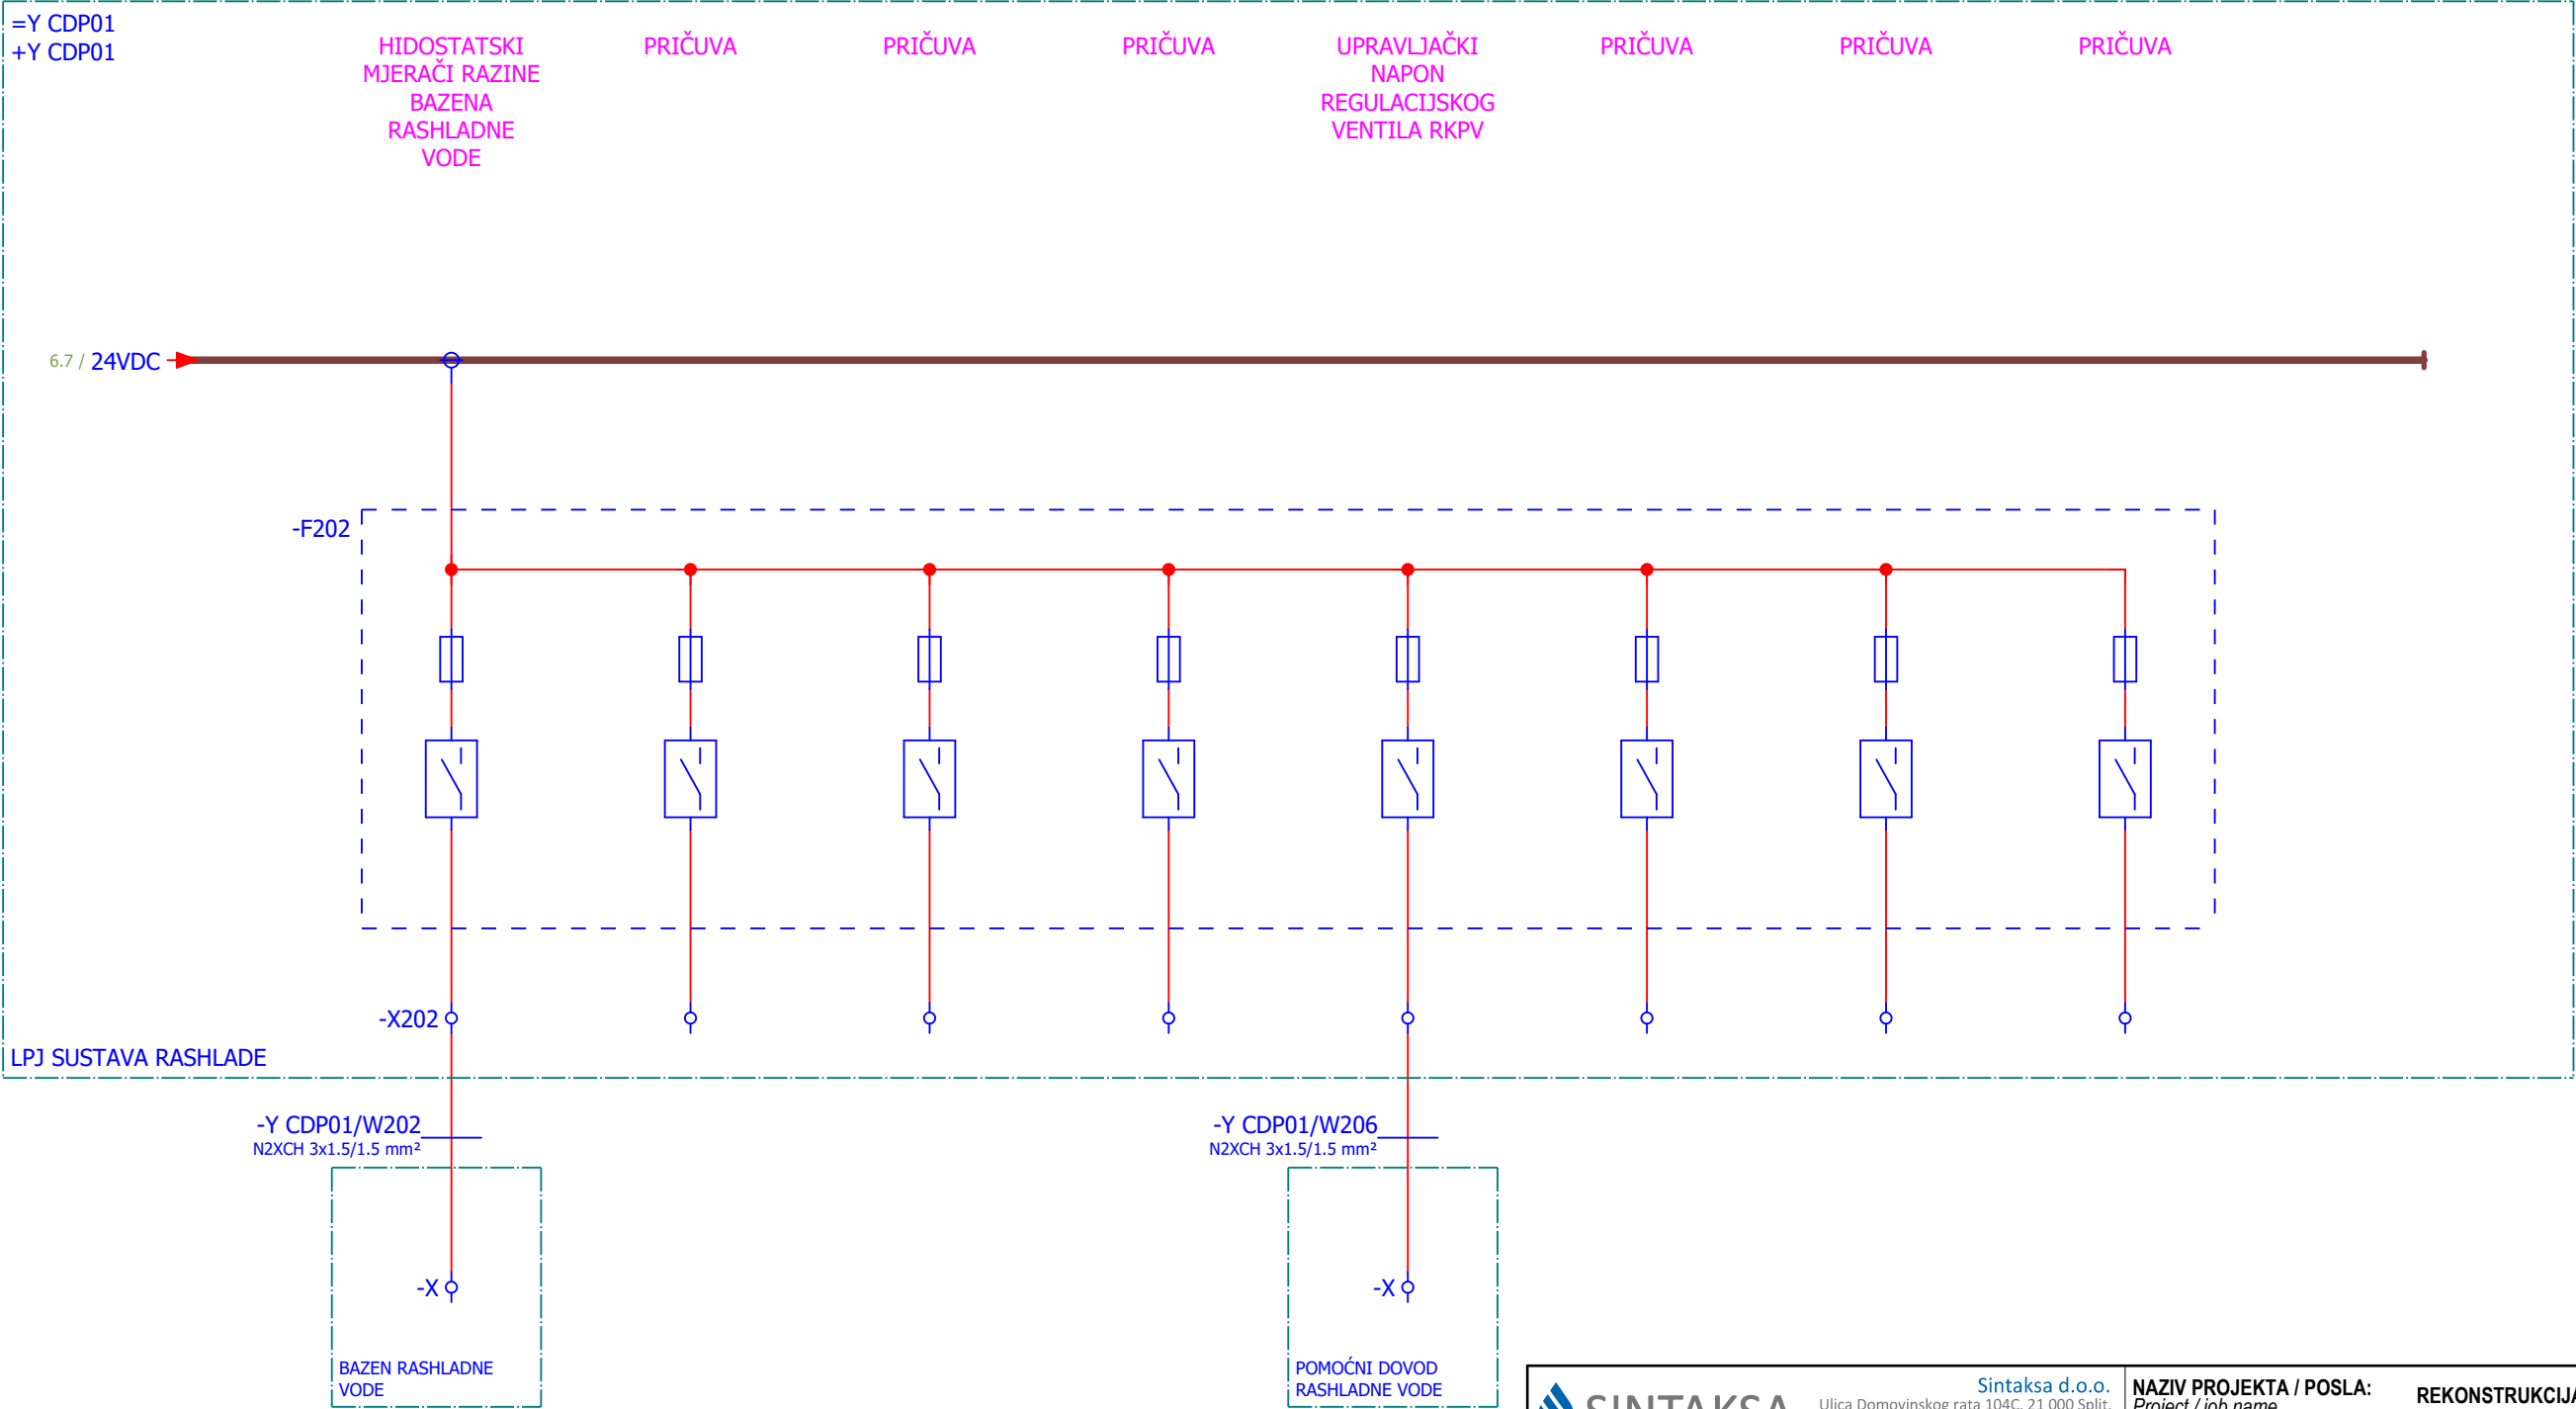

00	Radna verzija	2026-07-31	Tamara Trogrlić
REV. Rev.	NAPOMENA Note	DATUM Date	IZRADIO Drawn

SINTAKSA A Voith Company			Sintaksa d.o.o. Ulica Domovinskog rata 104C, 21 000 Split, Tuškanova 37, 10000 Zagreb T: +385 1 2310 273 info@sintaksa.hr www.sintaksa.hr			NAZIV PROJEKTA / POSLA: <i>Project / job name</i>			REKONSTRUKCIJA HE SENJ - FAZA I.																	
PROJEKTANT: <i>Design engineer</i>			Patrik Kovač, mag. ing. el. techn. inf.			INVESTITOR / PODNOŠITELJ ZAHTEJA: <i>Investor</i>			HRVATSKA ELEKTROPRIVREDA d.o.o Ulica grada Vukovara 37, 10000 Zagreb, OIB: 28921978587																	
IZRADIO: <i>Drawn</i>			Tamara Trogrlić, mag. ing. el. techn. inf.			GRAĐEVINA / ZAHVAT U PROSTORU: <i>Object</i>			HE Senj Na katastarskim česticama k.o. Sveti Juraj, k.o. Melnice i k.o. Brlog																	
PROJEKTIRANI DIO: <i>Scope of design</i>			STROJARSKI PROJEKT			KONTROLIRAO: <i>Checked</i>			Patrik Kovač, mag. ing. el. techn. inf.																	
RAZINA-STRUKA: <i>Design type</i>			IZVEDBENI PROJEKT			GLAVNI PROJEKTANT: <i>Design manager</i>			Natko Vučković, dipl.ing.el.																	
SADRŽAJ: <i>Content</i>			JEDNOPOLNA SHEMA			MJESTO I DATUM: <i>Place and date</i>			Zagreb, 2026-07-31																	
OZNAKA NACRTA <i>Drawing designation</i>			FORMAT <i>Paper size</i>			MJERILO <i>Scale</i>			ZOP <i>Com. pr. des.</i>			PROJEKT <i>Project</i>			MAPA <i>Folder</i>			PRILOG <i>Drawing</i>			REVIZIJA <i>Revision</i>			LIST <i>Page</i>		
26015-DD-EE-01-101-00			A3			1:10			SEN.1273 —			26015 —			1E12-3 —			101 —			00 —			7 / 7		