
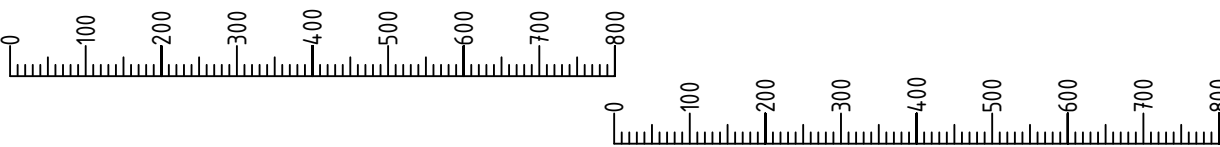



+Y BJP14
FILTRI I VENTILI SUSTAVA
RASHLADE

+Y CDP01
LPJ SUSTAVA RASHLADE

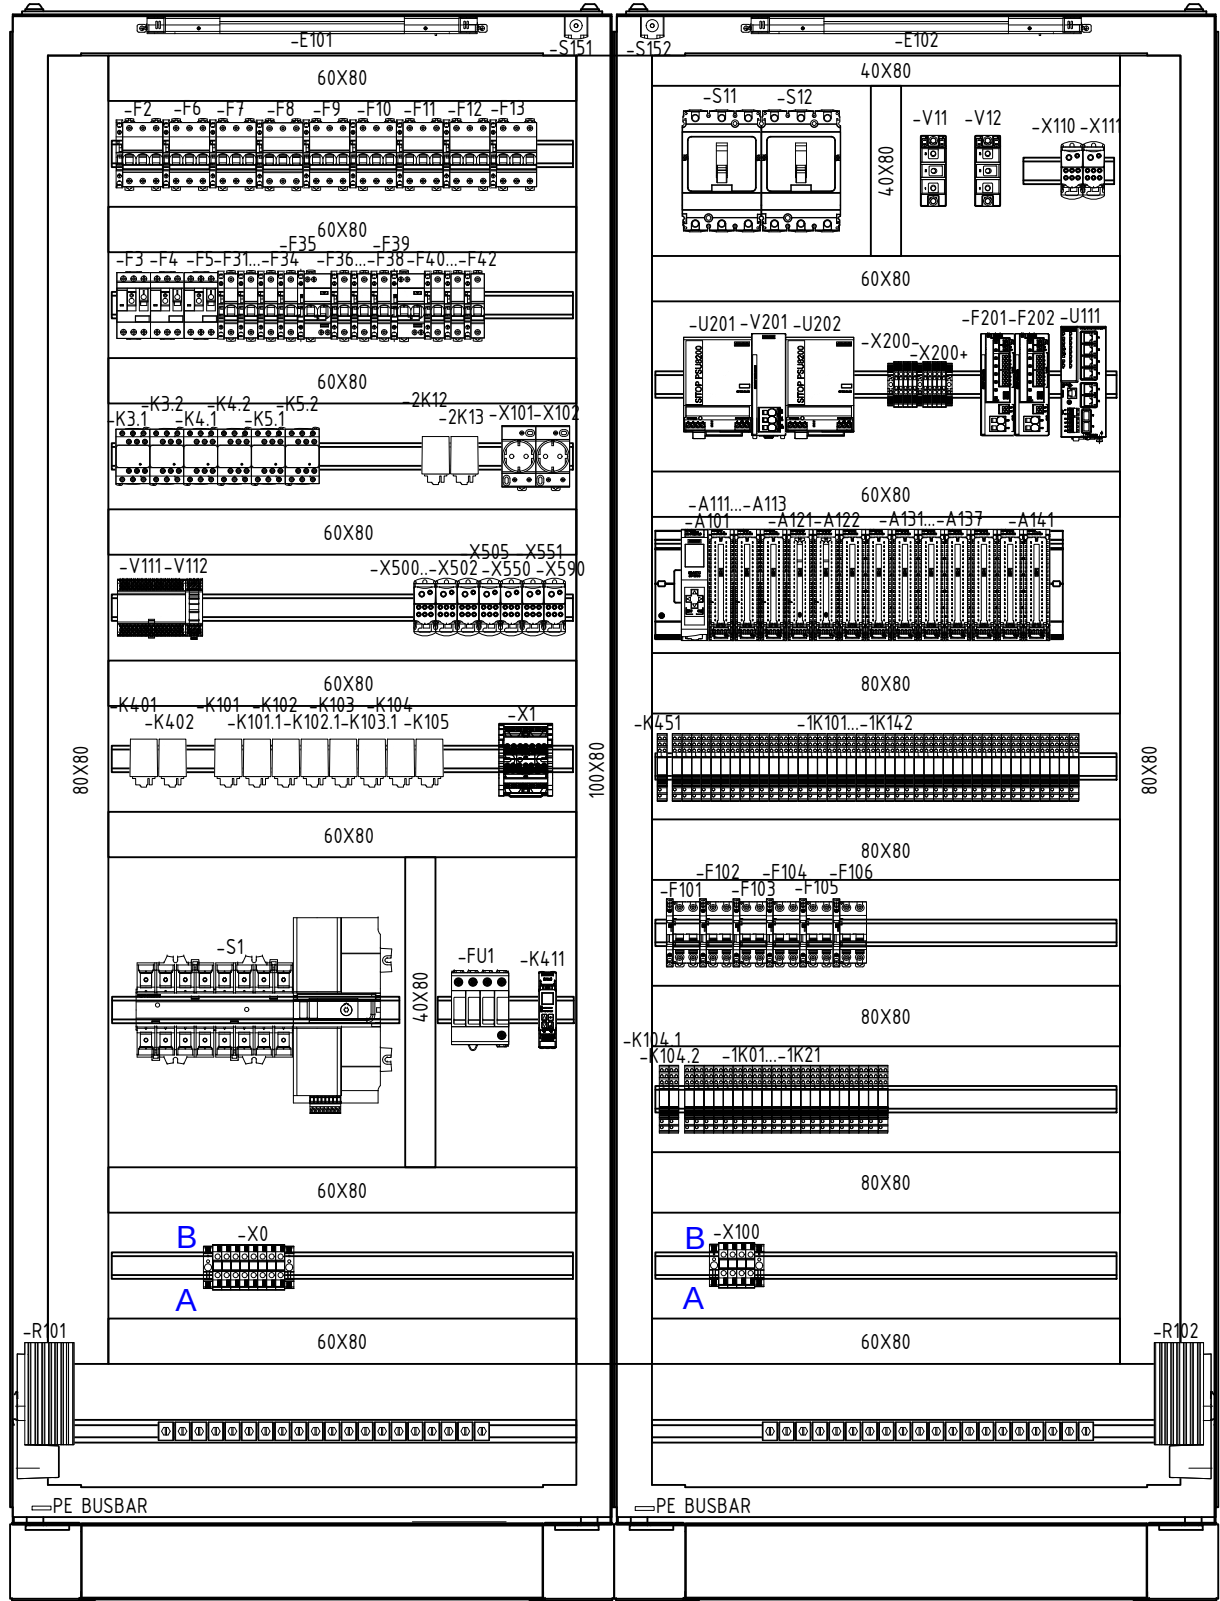

Dubina ormara: 800 mm

POGLED S DESNA

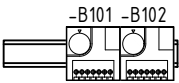


01	Za izradu	21.08.2026.	LB
00	Radna verzija	31.07.2026.	LB
REV. Rev.	NAPOMENA Note		DATUM Date
 Sintaksa d.o.o. projektiranje, konzalting i inženjering d.o.o. HR/21209 Solin, Brza cesta 4, Mravince OIB: 32357958120		NAZIV PROJEKTA / POSILA: Project / job name REKONSTRUKCIJA HE SENJ - FAZA I	
PROJEKTANT: Design engineer Patrik Kovač, mag. ing. el.		NARUČITELJ / PODNOŠITELJ ZAHTEVA: Client HEP-Proizvodnja d.o.o. Ulica grada Vukovara 37, 10000 Zagreb	
IZRADIO: Drawn Luka Božičević, mag. ing. el.		GRAĐEVINA / ZAHVAT U PROSTORU: Object HE SENJ	
PREGLEDAO: Checked Patrik Kovač, mag. ing. el.		PROJEKTIRANI DIO: Scope of design ELEKTROTEHNIČKI PROJEKT	
GLAVNI PROJEKTANT: Design manager Natko Vučković, dipl.ing.el.		RAZINA-STRUKA: Design type IZVEDBENI PROJEKT	
MJESTO I DATUM: Place and date Zagreb, 21.08.2026.		NAZIV: Content Prednji izgled ormara LPJ sustava rashlade +Y CDP01 i ormara filtera i ventila +Y BJP14 - bez vrata	
OZNAKA NACRTA Drawing designation 26015-DD-EE-01-112-01	FORMAT Paper size A3	MJERILO Scale 1:10	ZOP Common pr. des. SEN.1273 -
PROJEKT Project 26015 -		MAPA Folder 1E12-3 -	PRILOG Drawing 112 -
REVIZIJA Revision 01 -		LIST Page 2 / 6	

+Y CDP01

LPJ SUSTAVA RASHLADE

+Y BJP14

FILTRI I VENTILI SUSTAVA RASHLADE

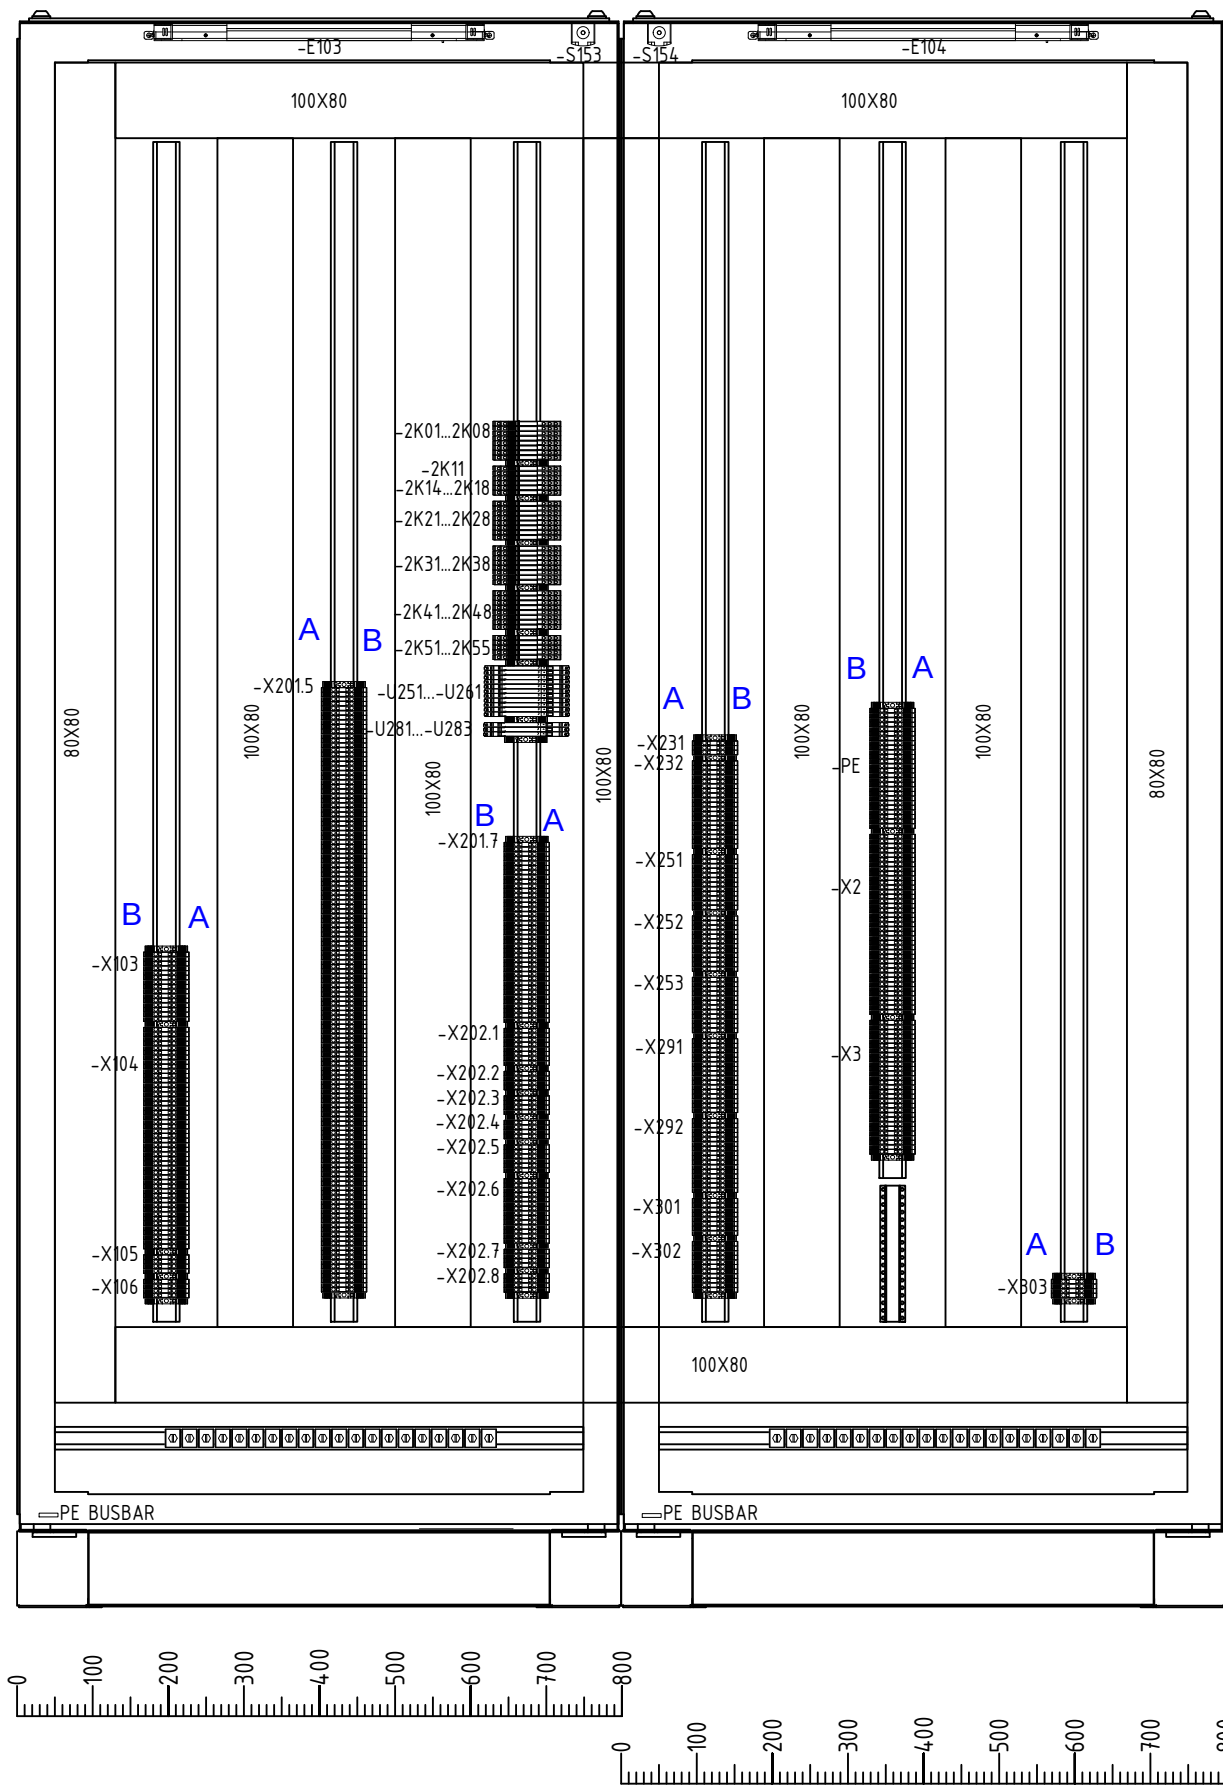

01	Za izradu	21.08.2026.	LB
00	Radna verzija	31.07.2026.	LB
REV. Rev.	NAPOMENA Note		DATUM Date
IZRADIO Drawn			
PROJEKTANT: Design engineer		NAZIV PROJEKTA / POSLA: Project / job name	
IZRADIO: Drawn		NARUČITELJ / PODNOSITELJ ZAHTEVA: Client	
PREGLEDAO: Checked		GRAĐEVINA / ZAHVAT U PROSTORU: Object	
GLAVNI PROJEKTANT: Design manager		PROJEKTIRANI DIO: Scope of design	
MJESTO I DATUM: Place and date		RAZINA-STRUKA: Design type	
OZNAKA NACRTA Drawing designation		NAZIV: Content	
FORMAT Paper size		ZOP Common pr. des.	
MJERILO Scale		PROJEKT Project	
		MAPA Folder	
		PRILOG Drawing	
		REVIZIJA Revision	
		LIST Page	
26015-DD-EE-01-112-01		SEN.1273 - 26015 - 1E12-3 - 112 - 01 - 4 / 6	