


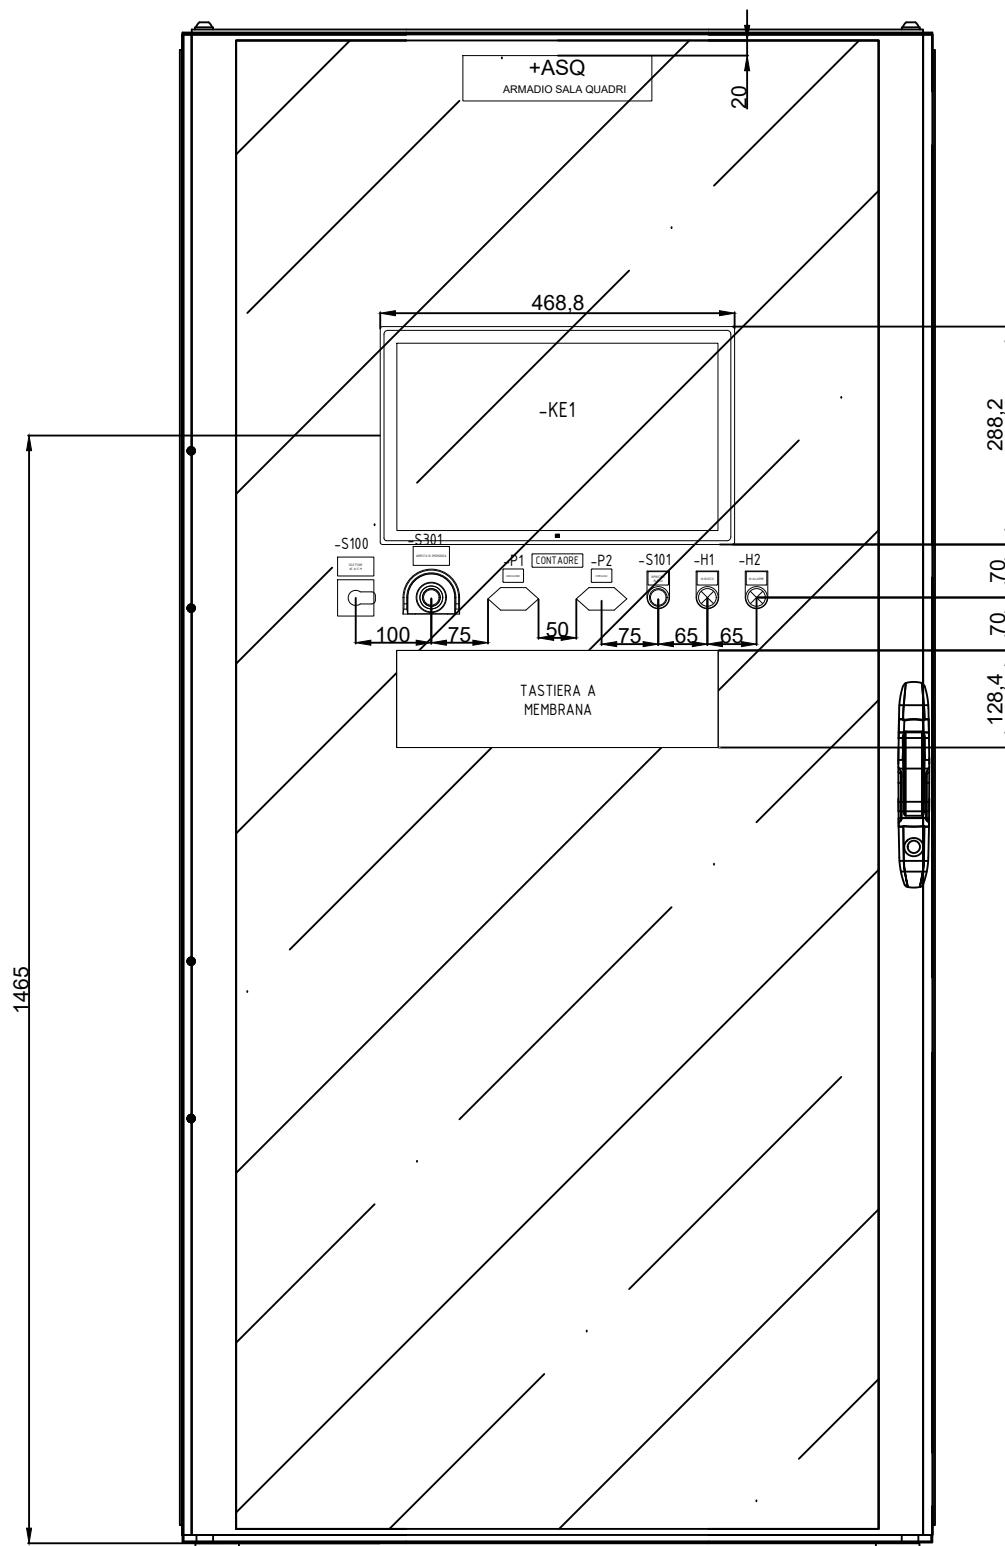


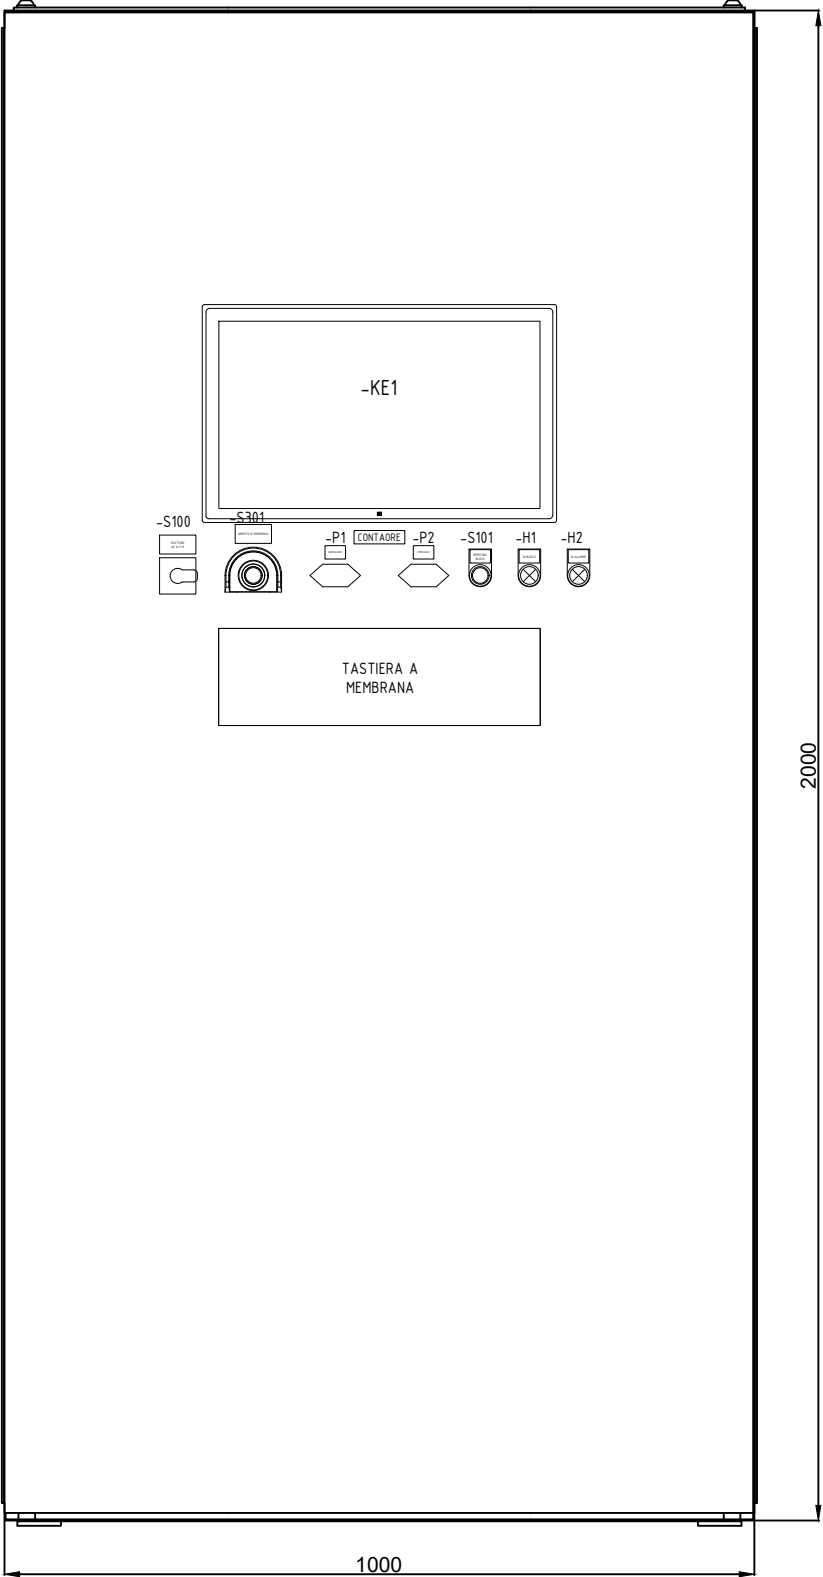

				Progettato da: Luka Božičević, mag. polytechn. et inf.			 Sintaksa d.o.o. Brza cesta 4, 21 210 Mravince-Solin, Croatia Tuškanova 37, 10000 Zagreb, Croatia T: +385 1 2310 273 info@sintaksa.hr www.sintaksa.hr					Commissa:	Centrale idroelettrica di Santa Massenza Italia	
01	Updated cable gland plate	2026-05-29	L.Božičević	Approvato da: Patrik Kovač, dipl. ing. el.								Ambito di progettazione:	Elettrico Systema di controllo, E-BoP	
00	First issue	2024-11-20	L.Božičević	Luogo e data: Zagreb, 2026-05-29			Cliente: Hydro Dolomiti Energia Srl Viale Trieste 43, 38122 Trento, Italia					Tipologia di disegno:	Offerta	
Rev.	Descrizione	Data	Firme	Designazione del disegno OF-SI-24109-000	Formato A3	Scala 1:10	Progetto OF-SI	Mappa 24109	Allegato 000	Revisione 01	Foglio 1 / 3	Contenuto:	Armadio sala quadri +ASQ - Disegno di assemblaggio cubicolo - Vista frontale con porta	

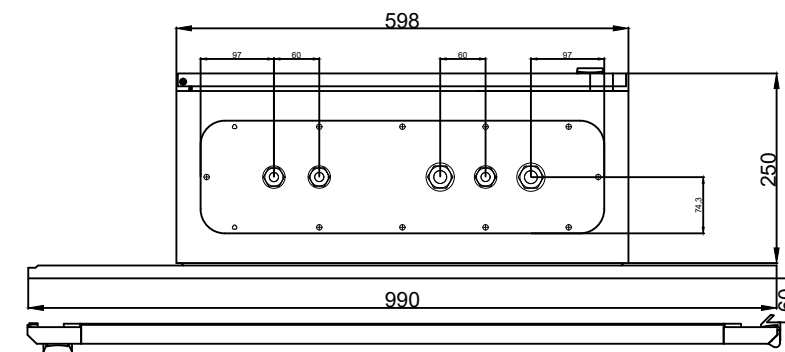

				Progettato da: Luka Božičević, mag. polytechn. et inf.			SINTAKSA Brza cesta 4, 21 210 Mravince-Solin, Croatia Tuškanova 37, 10000 Zagreb, Croatia T: +385 1 2310 273 info@sintaksa.hr www.sintaksa.hr A Voith Company Sintaksa d.o.o.					Commissa:	Centrale idroelettrica di Santa Massenza Italia	
01	Updated cable gland plate	2026-05-29	L.Božičević	Approvato da: Patrik Kovač, dipl. ing. el.								Ambito di progettazione:	Elettrico Systema di controllo, E-BoP	
00	First issue	2024-11-20	L.Božičević	Luogo e data: Zagreb, 2026-05-29			Cliente: Hydro Dolomiti Energia Srl Viale Trieste 43, 38122 Trento, Italia					Tipologia di disegno:	Offerta	
Rev.	Descrizione	Data	Firme	Designazione del disegno OF-SI-24109-000	Formato A3	Scala 1:10	Progetto OF-SI	Mappa 24109	Allegato 000	Revisione 01	Foglio 2 / 3	Contenuto:	Armadio sala quadri +ASQ - Disegno di assemblaggio cubicolo - Vista frontale senza porta	

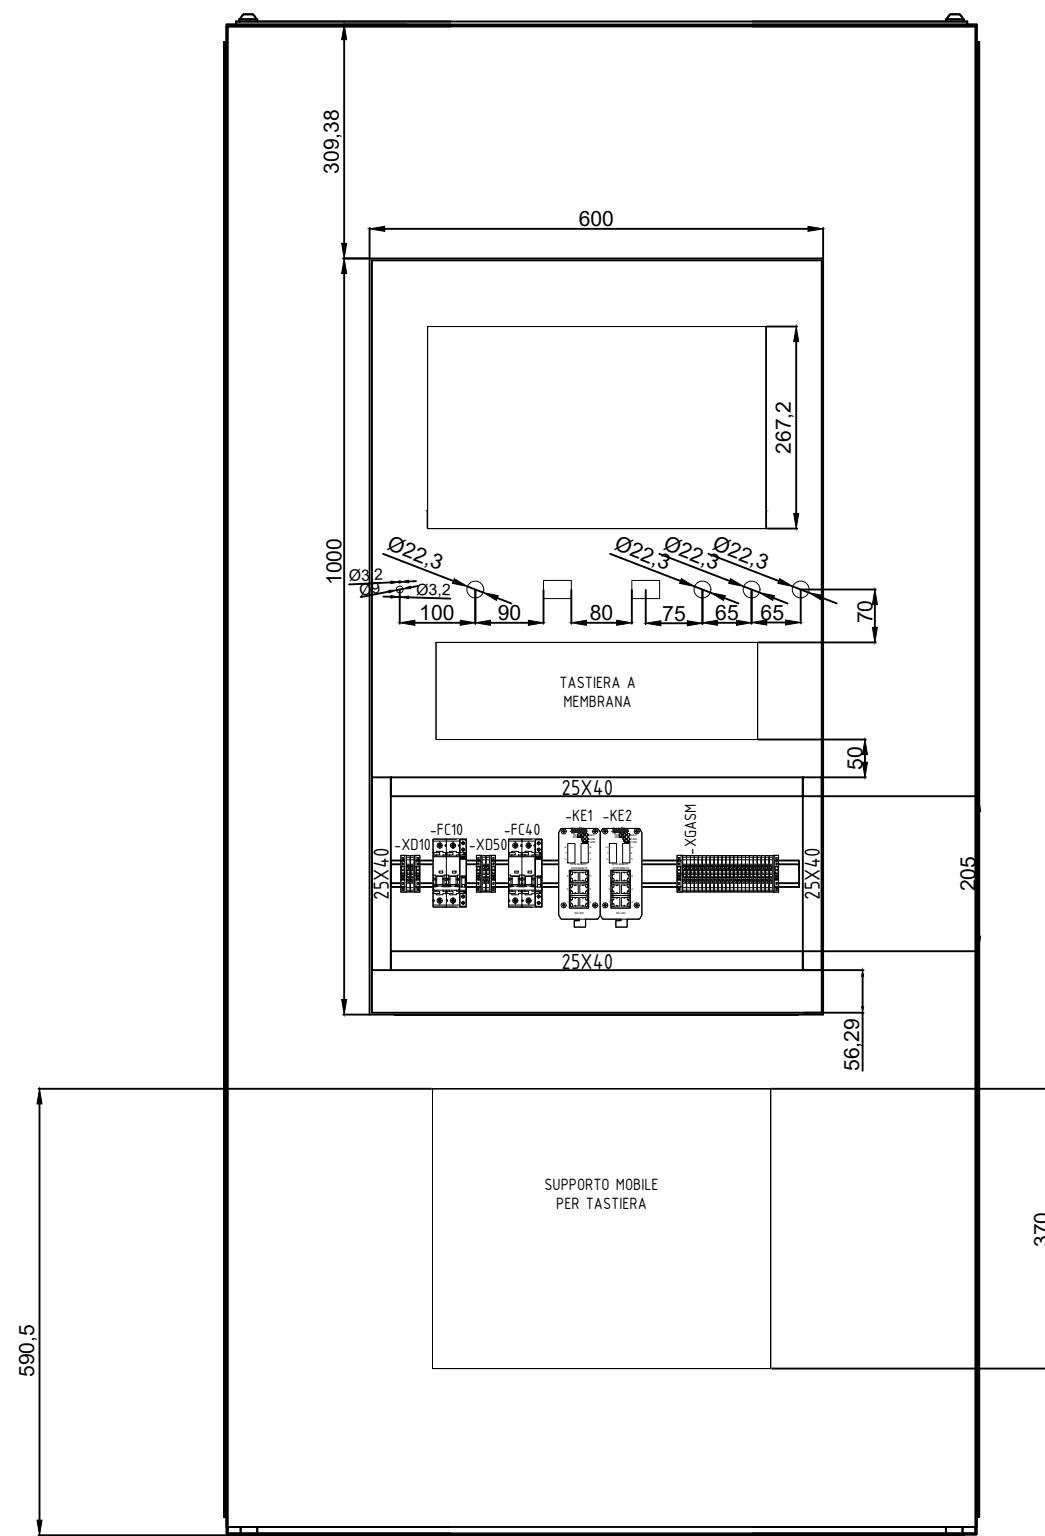

				Progettato da: Luka Božičević, mag. polytechn. et inf.			 Sintaksa d.o.o. Brza cesta 4, 21 210 Mravince-Solin, Croatia Tuškanova 37, 10000 Zagreb, Croatia T: +385 1 2310 273 info@sintaksa.hr www.sintaksa.hr A Voith Company					Commessa: Centrale idroelettrica di Santa Massenza Italia	
01	Updated cable gland plate	2026-05-29	L.Božičević	Approvato da: Patrik Kovač, dipl. ing. el.								Ambito di progettazione: Elettrico Systema di controllo, E-BoP	
00	First issue	2024-11-20	L.Božičević	Luogo e data: Zagreb, 2026-05-29			Cliente: Hydro Dolomiti Energia Srl Viale Trieste 43, 38122 Trento, Italia					Tipologia di disegno: Offerta	
Rev.	Descrizione	Data	Firme	Designazione del disegno OF-SI-24109-000	Formato A3	Scala 1:10	Progetto OF-SI	Mappa 24109	Allegato 000	Revisione 01	Foglio 3 / 3	Contenuto:	Armadio sala quadri +ASQ - Disegno di assemblaggio cubicolo - Vista posteriore senza porta