


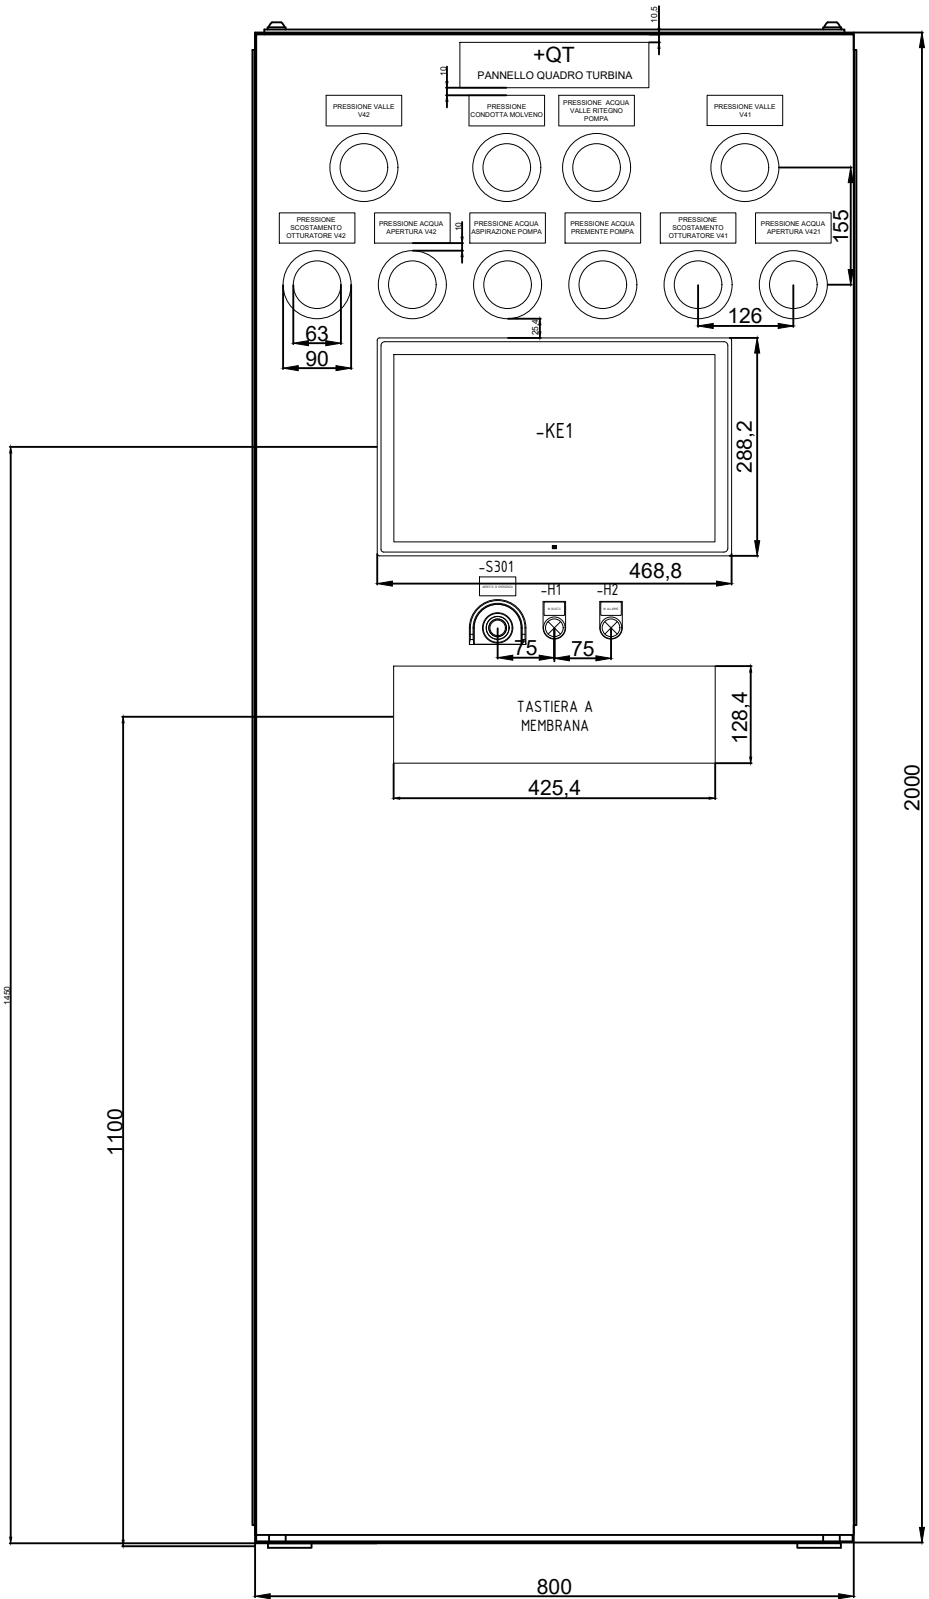


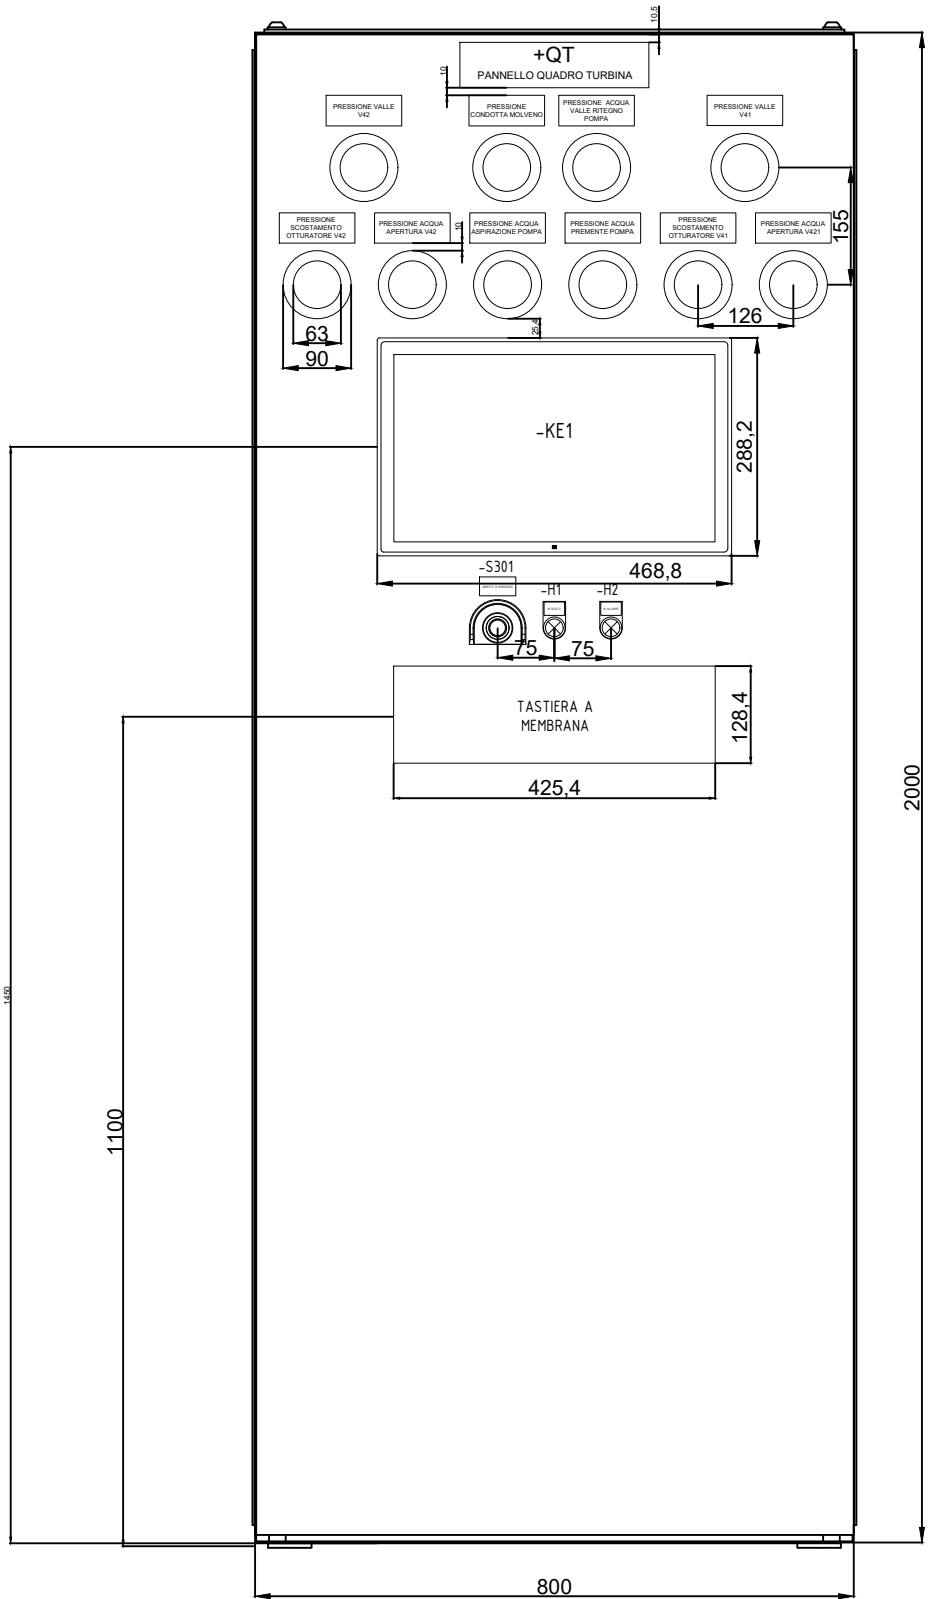

|      |                           |            |             |                                                        |               |               |   |                |                 |                 |                 |                             |                                                                                           |  |
|------|---------------------------|------------|-------------|--------------------------------------------------------|---------------|---------------|---|----------------|-----------------|-----------------|-----------------|-----------------------------|-------------------------------------------------------------------------------------------|--|
|      |                           |            |             | Progettato da: Luka Božičević, mag. polytechn. et inf. |               |               | <div><div>SINTAKSA<br/>A Voith Company</div></div> <div>Sintaksa d.o.o.<br/>Brza cesta 4, 21 210 Mravince-Solin, Croatia<br/>Tuškanova 37, 10000 Zagreb, Croatia<br/>T: +385 1 2310 273<br/>info@sintaksa.hr<br/>www.sintaksa.hr</div> |                |                 |                 |                 | Commessa:                   | Centrale idroelettrica di Santa Massenza<br>Italia                                        |  |
| 01   | Updated cable gland plate | 2026-05-29 | L.Božičević | Approvato da: Patrik Kovač, dipl. ing. el.             |               |               |   |                |                 |                 |                 | Ambito di<br>progettazione: | Elettrico<br>Systema di controllo, E-BoP                                                  |  |
| 00   | First issue               | 2024-11-20 | L.Božičević | Luogo e data: Zagreb, 2026-05-29                       |               |               | Cliente: Hydro Dolomiti Energia Srl<br>Viale Trieste 43, 38122 Trento, Italia   |                |                 |                 |                 | Tipologia di<br>disegno:    | Offerta                                                                                   |  |
| Rev. | Descrizione               | Data       | Firme       | Designazione del disegno<br>OF-SI-24109-000            | Formato<br>A3 | Scala<br>1:10 | Progetto<br>OF-SI   | Mappa<br>24109 | Allegato<br>000 | Revisione<br>01 | Foglio<br>1 / 3 | Contenuto:                  | Armadio sala quadri +ASQ - Disegno di assemblaggio<br>cubicolo - Vista frontale con porta |  |

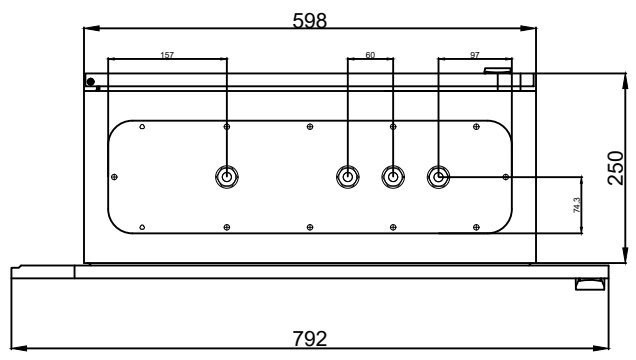

|      |                           |            |             |                                                        |               |               |   |                |                 |                 |                 |                             |                                                                                             |  |
|------|---------------------------|------------|-------------|--------------------------------------------------------|---------------|---------------|---|----------------|-----------------|-----------------|-----------------|-----------------------------|---------------------------------------------------------------------------------------------|--|
|      |                           |            |             | Progettato da: Luka Božičević, mag. polytechn. et inf. |               |               | <div><div>SINTAKSA<br/>A Voith Company</div></div> <div><div>Sintaksa d.o.o.</div><div>Brza cesta 4, 21 210 Mravince-Solin, Croatia<br/>Tuškanova 37, 10000 Zagreb, Croatia<br/>T: +385 1 2310 273<br/>info@sintaksa.hr<br/>www.sintaksa.hr</div></div> |                |                 |                 |                 | Commissa:                   | Centrale idroelettrica di Santa Massenza<br>Italia                                          |  |
| 01   | Updated cable gland plate | 2026-05-29 | L.Božičević | Approvato da: Patrik Kovač, dipl. ing. el.             |               |               |   |                |                 |                 |                 | Ambito di<br>progettazione: | Elettrico<br>Systema di controllo, E-BoP                                                    |  |
| 00   | First issue               | 2024-11-20 | L.Božičević | Luogo e data: Zagreb, 2026-05-29                       |               |               | Cliente: Hydro Dolomiti Energia Srl<br>Viale Trieste 43, 38122 Trento, Italia   |                |                 |                 |                 | Tipologia di<br>disegno:    | Offerta                                                                                     |  |
| Rev. | Descrizione               | Data       | Firme       | Designazione del disegno<br>OF-SI-24109-000            | Formato<br>A3 | Scala<br>1:10 | Progetto<br>OF-SI   | Mappa<br>24109 | Allegato<br>000 | Revisione<br>01 | Foglio<br>2 / 3 | Contenuto:                  | Armadio sala quadri +ASQ - Disegno di assemblaggio<br>cubicolo - Vista frontale senza porta |  |

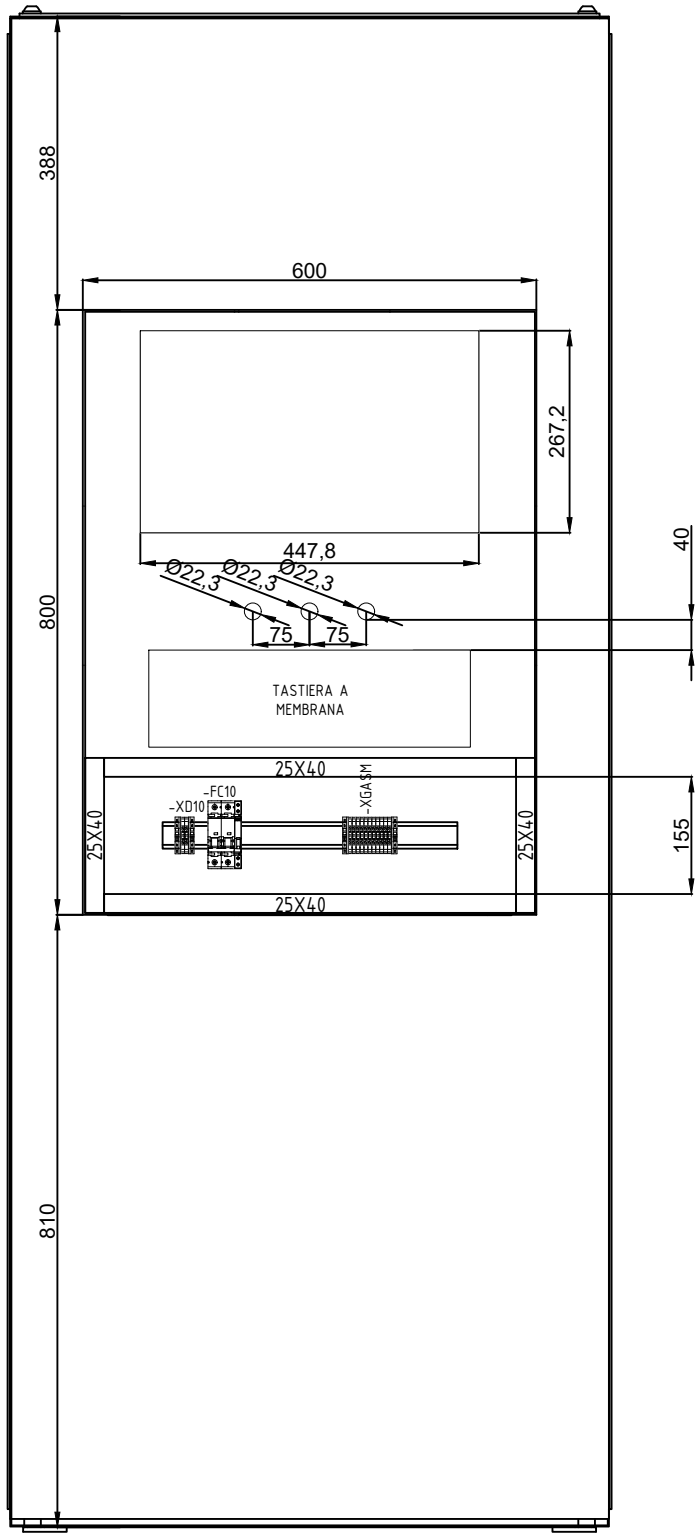

|      |                           |            |             |                                                        |               |               |   |                  |                   |                   |                   |                             |                                                                                               |  |
|------|---------------------------|------------|-------------|--------------------------------------------------------|---------------|---------------|---|------------------|-------------------|-------------------|-------------------|-----------------------------|-----------------------------------------------------------------------------------------------|--|
|      |                           |            |             | Progettato da: Luka Božičević, mag. polytechn. et inf. |               |               | <div><div><div><div>Sintaksa d.o.o.</div><div>Brza cesta 4, 21 210 Mravince-Solin, Croatia</div><div>Tužkanova 37, 10000 Zagreb, Croatia</div><div>T: +385 1 2310 273</div><div>info@sintaksa.hr</div><div>www.sintaksa.hr</div></div></div></div> |                  |                   |                   |                   | Commessa:                   | Centrale idroelettrica di Santa Massenza<br>Italia                                            |  |
| 01   | Updated cable gland plate | 2026-05-29 | L.Božičević | Approvato da: Patrik Kovač, dipl. ing. el.             |               |               |   |                  |                   |                   |                   | Ambito di<br>progettazione: | Elettrico<br>Systema di controllo, E-BoP                                                      |  |
| 00   | First issue               | 2024-11-20 | L.Božičević | Luogo e data: Zagreb, 2026-05-29                       |               |               | Cliente: Hydro Dolomiti Energia Srl<br>Viale Trieste 43, 38122 Trento, Italia   |                  |                   |                   |                   | Tipologia di<br>disegno:    | Offerta                                                                                       |  |
| Rev. | Descrizione               | Data       | Firme       | Designazione del disegno<br>OF-SI-24109-000            | Formato<br>A3 | Scala<br>1:10 | Progetto<br>OF-SI   | Mappa<br>— 24109 | Allegato<br>— 000 | Revisione<br>— 01 | Foglio<br>— 3 / 3 | Contenuto:                  | Armadio sala quadri +ASQ - Disegno di assemblaggio<br>cubicolo - Vista posteriore senza porta |  |