



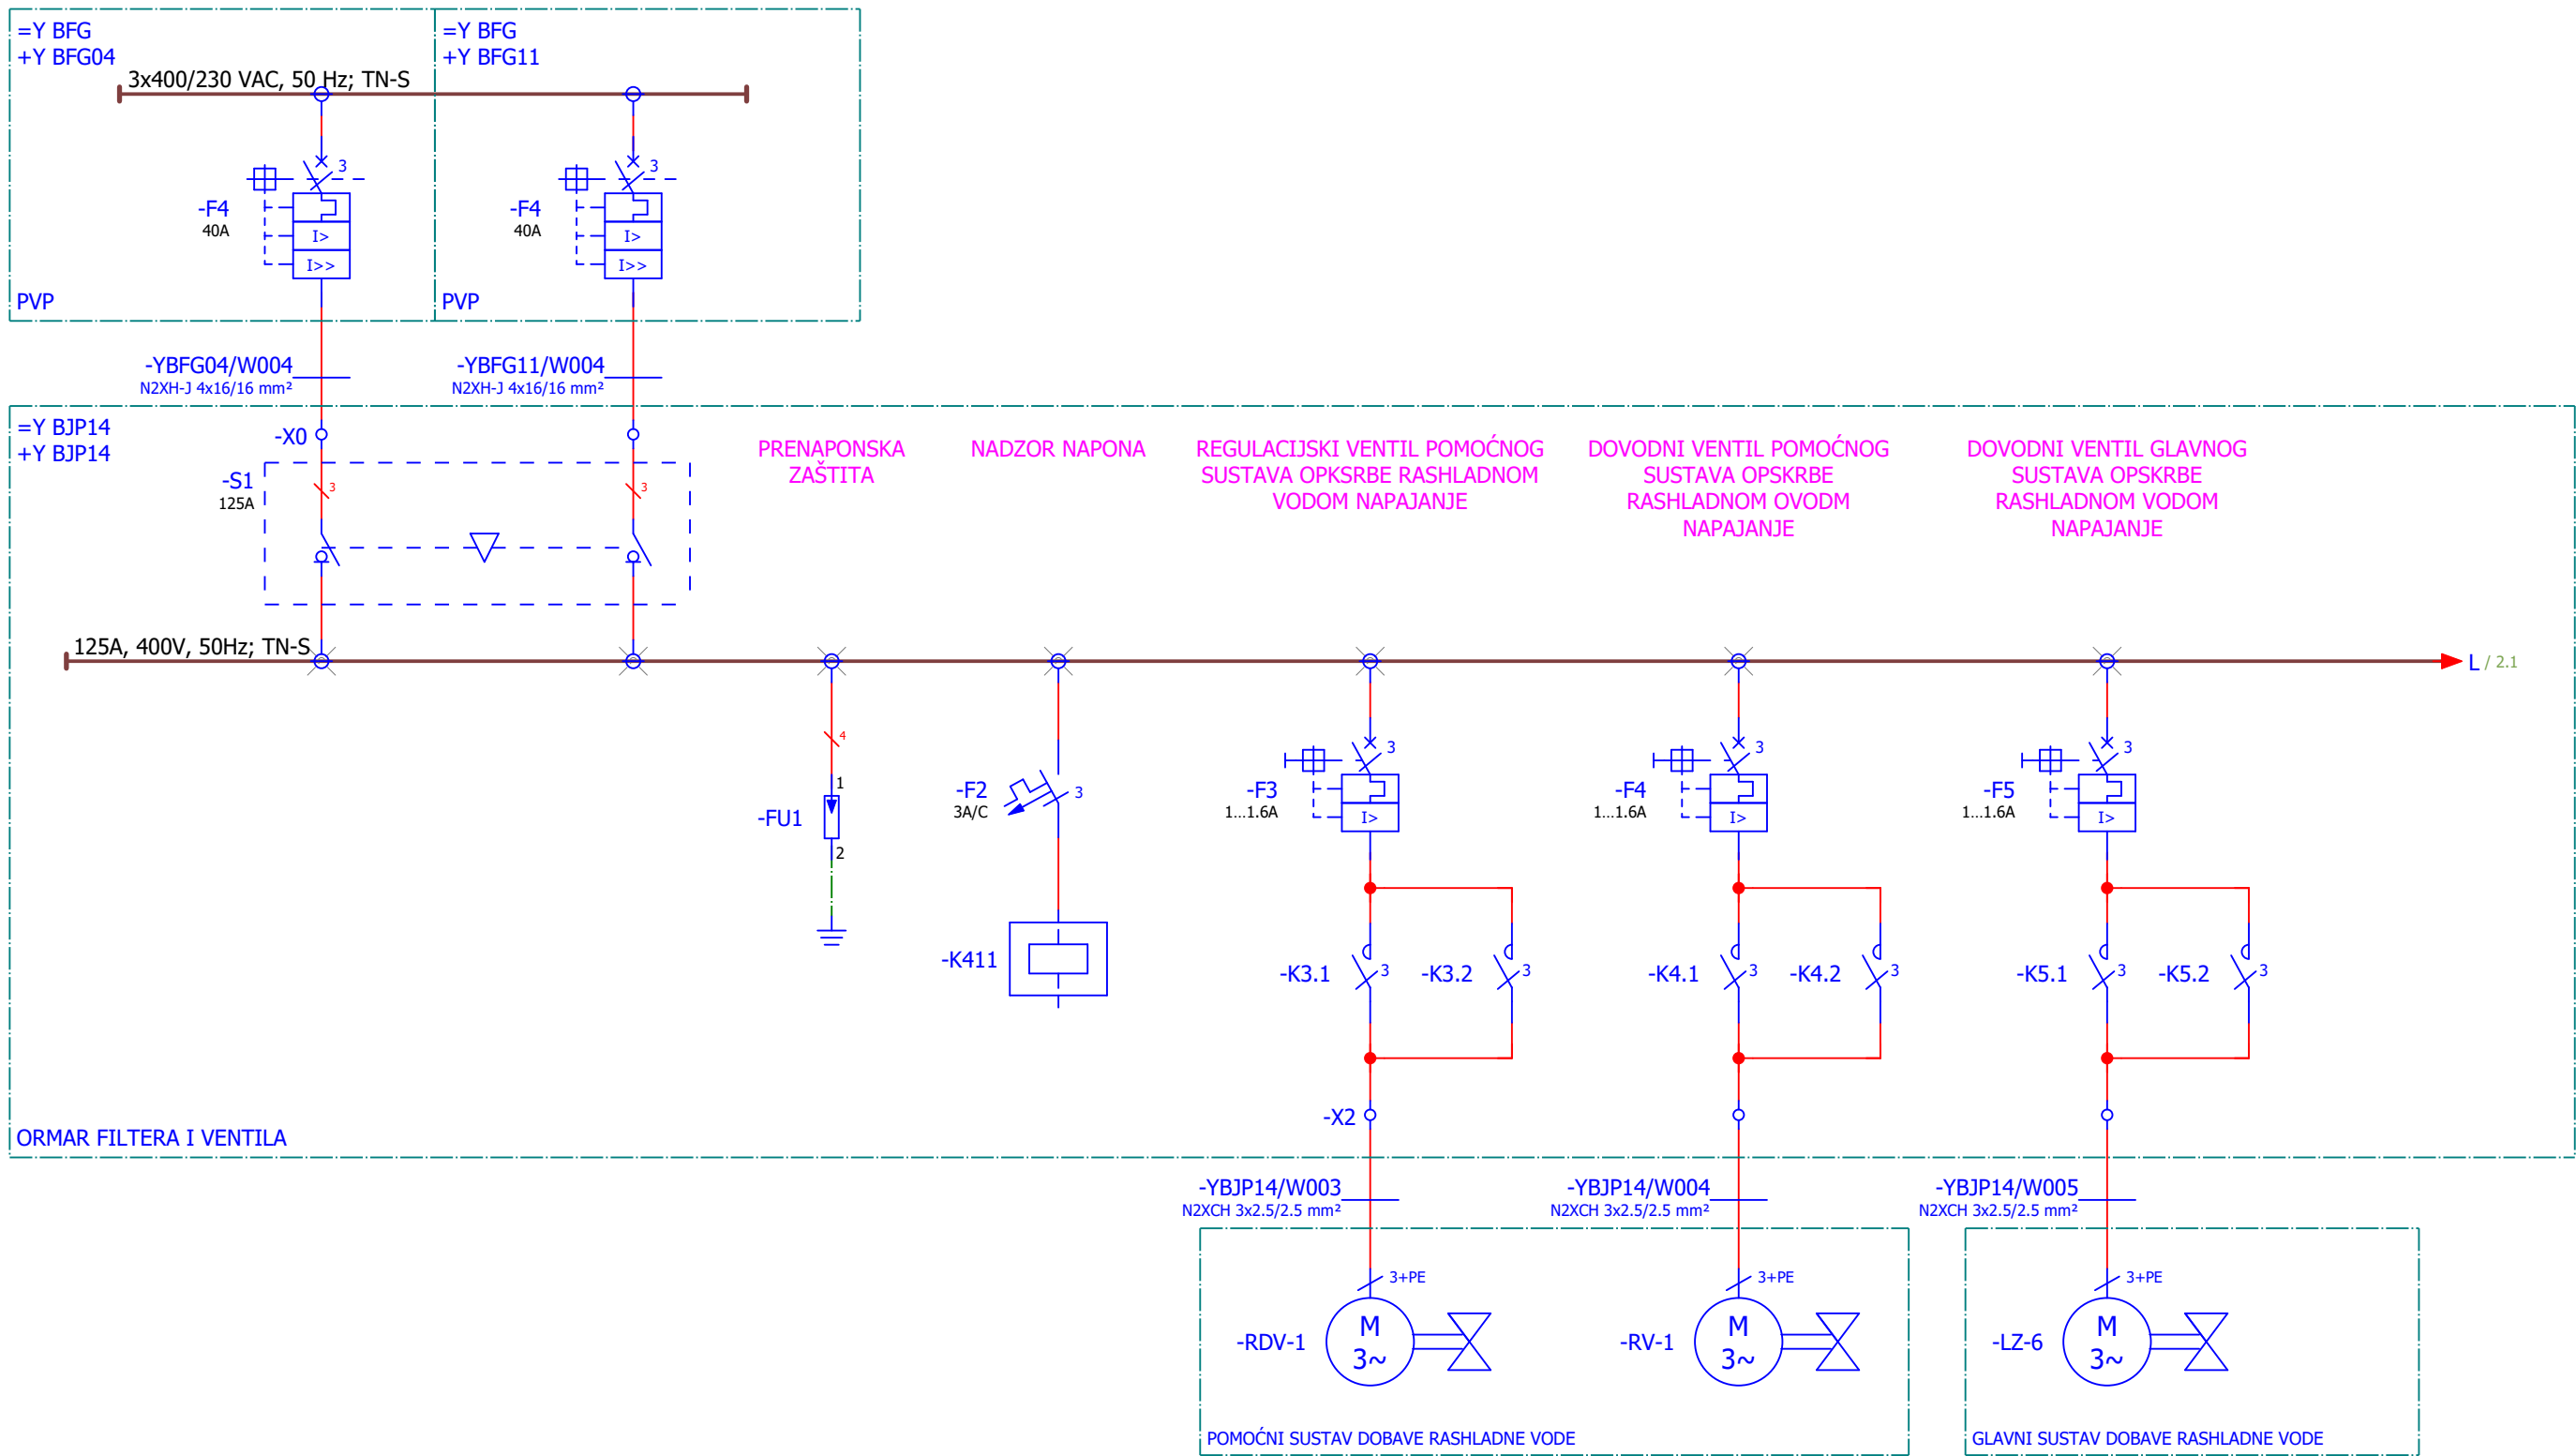


01	Za izradu	2026-08-26	Tamara Trogrić
00	Radna verzija	2026-07-31	Tamara Trogrić
REV. Rev.	NAPOMENA Note		DATUM Date
			IZRADIO Drawn

SINTAKSA A Voith Company		Sintaksa d.o.o. Ulica Domovinskog rata 104C, 21 000 Split, Tuškanova 37, 10000 Zagreb T: +385 1 2310 273 info@sintaksa.hr www.sintaksa.hr		NAZIV PROJEKTA / POSLA: Project / job name		REKONSTRUKCIJA HE SENJ - FAZA I.	
PROJEKTANT: Design engineer		Patrik Kovač, mag. ing. el. techn. inf.		INVESTITOR / PODNOŠITELJ ZAHTJEVA: Investor		HRVATSKA ELEKTROPRIVREDA d.o.o Ulica grada Vukovara 37, 10000 Zagreb, OIB: 28921978587	
IZRADIO: Drawn		Tamara Trogrić, mag. ing. el. techn. inf.		GRAĐEVINA / ZAHVAT U PROSTORU: Object		HE Senj Na katastarskim česticama k.o. Sveti Juraj, k.o. Melnice i k.o. Brlog	
KONTROLIRAO: Checked		Patrik Kovač, mag. ing. el. techn. inf.		PROJEKTIRANI DIO: Scope of design		STROJARSKI PROJEKT	
GLAVNI PROJEKTANT: Design manager		Natko Vučković, dipl.ing.el.		RAZINA-STRUKA: Design type		IZVEDBENI PROJEKT	
MJESTO I DATUM: Place and date		Zagreb, 2026-07-31		SADRŽAJ: Content		JEDNOPOLNA SHEMA	
OZNAKA NACRTA Drawing designation		FORMAT Paper size		MJERILO Scale		ZOP Com. pr. des.	PROJEKT Project
26015-DD-EE-01-101-00		A3		1:10		MAPA Folder	PRILOG Drawing
						REVIZIJA Revision	LIST Page
						SEN.1273 — 26015 — 1E12-3 — 101 — 00 —	1 / 8

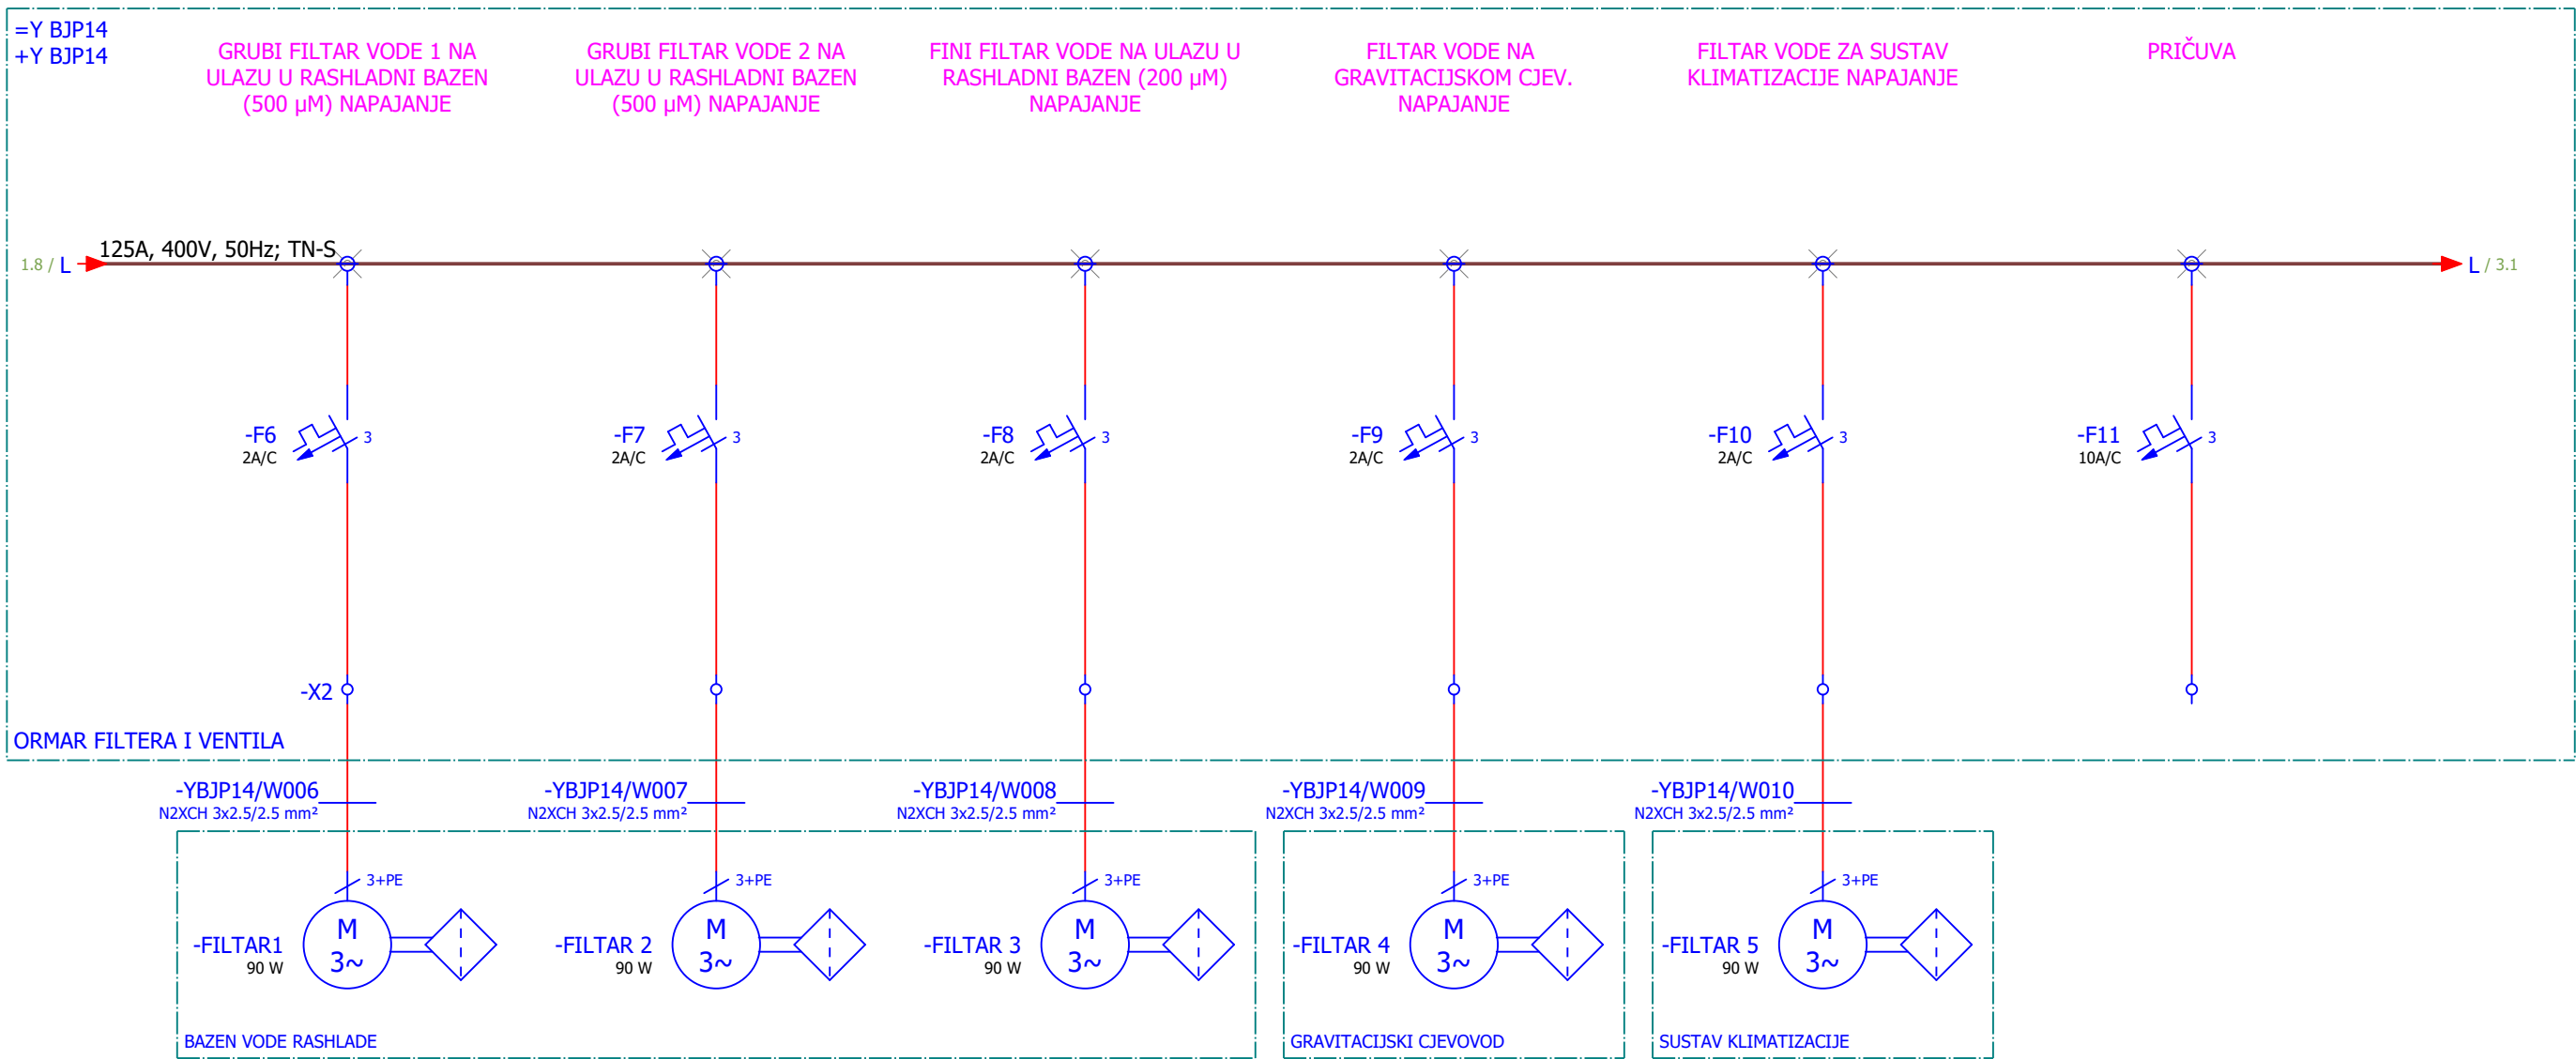


01	Za izradu	2026-08-26	Tamara Trogrić
00	Radna verzija	2026-07-31	Tamara Trogrić
REV. Rev.	NAPOMENA Note	DATUM Date	IZRADIO Drawn

 SINTAKSA A Voith Company Sintaksa d.o.o. Ulica Domovinskog rata 104C, 21 000 Split, Tuškanova 37, 10000 Zagreb T: +385 1 2310 273 info@sintaksa.hr www.sintaksa.hr			NAZIV PROJEKTA / POSLA: <i>Project / job name</i>		REKONSTRUKCIJA HE SENJ - FAZA I.							
PROJEKTANT: <i>Design engineer</i>			Patrik Kovač, mag. ing. el. techn. inf.		INVESTITOR / PODNOŠITELJ ZAHTJEVA: <i>Investor</i>		HRVATSKA ELEKTROPRIVREDA d.o.o Ulica grada Vukovara 37, 10000 Zagreb, OIB: 28921978587					
IZRADIO: <i>Drawn</i>			Tamara Trogrić, mag. ing. el. techn. inf.		GRAĐEVINA / ZAHTVAT U PROSTORU: <i>Object</i>		HE Senj Na katastarskim česticama k.o. Sveti Juraj, k.o. Melnice i k.o. Brlog					
KONTROLIRAO: <i>Checked</i>			Patrik Kovač, mag. ing. el. techn. inf.		PROJEKTIRANI DIO: <i>Scope of design</i>		STROJARSKI PROJEKT					
GLAVNI PROJEKTANT: <i>Design manager</i>			Natko Vučković, dipl.ing.el.		RAZINA-STRUKA: <i>Design type</i>		IZVEDBENI PROJEKT					
MJESTO I DATUM: <i>Place and date</i>			Zagreb, 2026-07-31		SADRŽAJ: <i>Content</i>		JEDNOPOLNA SHEMA					
OZNAKA NACRTA <i>Drawing designation</i>			FORMAT <i>Paper size</i>		MJERILO <i>Scale</i>		ZOP <i>Com. pr. des.</i>	PROJEKT <i>Project</i>	MAPA <i>Folder</i>	PRILOG <i>Drawing</i>	REVIZIJA <i>Revision</i>	LIST <i>Page</i>
26015-DD-EE-01-101-00			A3		1:10		SEN.1273 —	26015 —	1E12-3 —	101 —	00 —	2 / 8

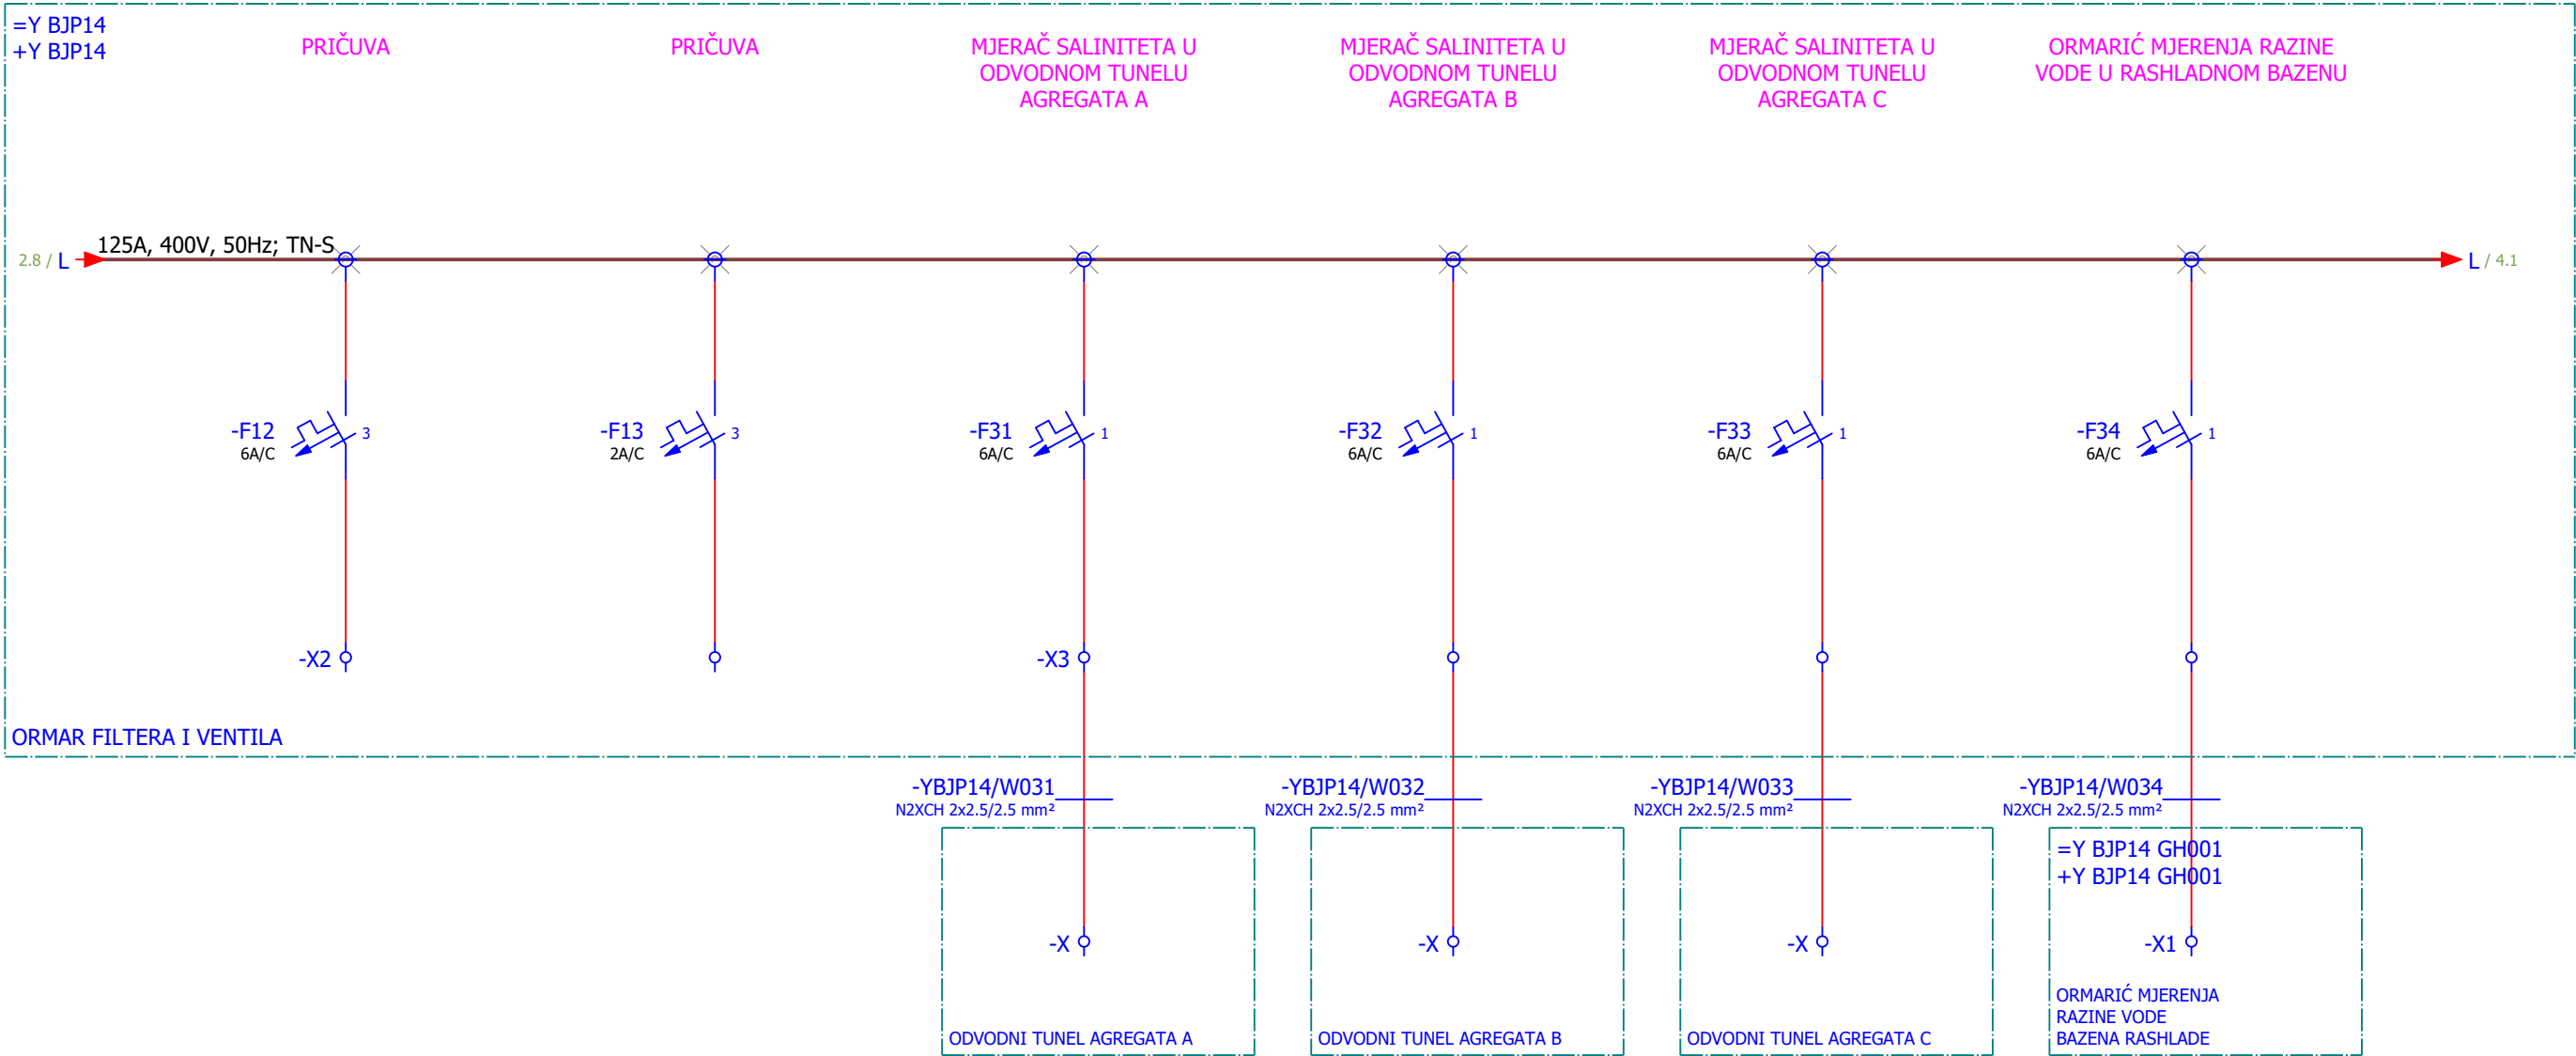


01	Za izradu	2026-08-26	Tamara Trogrić
00	Radna verzija	2026-07-31	Tamara Trogrić
REV. Rev.	NAPOMENA Note		IZRADIO Drawn

SINTAKSA A Voith Company Sintaksa d.o.o. Ulica Domovinskog rata 104C, 21 000 Split, Tuškanova 37, 10000 Zagreb T: +385 1 2310 273 info@sintaksa.hr www.sintaksa.hr			NAZIV PROJEKTA / POSLA: <i>Project / job name</i>		REKONSTRUKCIJA HE SENJ - FAZA I.							
PROJEKTANT: <i>Design engineer</i>			Patrik Kovač, mag. ing. el. techn. inf.		INVESTITOR / PODNOŠITELJ ZAHTJEVA: <i>Investor</i>		HRVATSKA ELEKTROPRIVREDA d.o.o Ulica grada Vukovara 37, 10000 Zagreb, OIB: 28921978587					
IZRADIO: <i>Drawn</i>			Tamara Trogrić, mag. ing. el. techn. inf.		GRAĐEVINA / ZAHVAT U PROSTORU: <i>Object</i>		HE Senj Na katastarskim česticama k.o. Sveti Juraj, k.o. Melnice i k.o. Brlog					
KONTROLIRAO: <i>Checked</i>			Patrik Kovač, mag. ing. el. techn. inf.		PROJEKTIRANI DIO: <i>Scope of design</i>		STROJARSKI PROJEKT					
KONTROLIRAO: <i>Checked</i>			Patrik Kovač, mag. ing. el. techn. inf.		RAZINA-STRUKA: <i>Design type</i>		IZVEDBENI PROJEKT					
GLAVNI PROJEKTANT: <i>Design manager</i>			Natko Vučković, dipl.ing.el.		SADRŽAJ: <i>Content</i>		JEDNOPOLNA SHEMA					
MJESTO I DATUM: <i>Place and date</i>			Zagreb, 2026-07-31									
OZNAKA NACRTA <i>Drawing designation</i>			FORMAT <i>Paper size</i>		MJERILO <i>Scale</i>		ZOP <i>Com. pr. des.</i>	PROJEKT <i>Project</i>	MAPA <i>Folder</i>	PRILOG <i>Drawing</i>	REVIZIJA <i>Revision</i>	LIST <i>Page</i>
26015-DD-EE-01-101-00			A3		1:10		SEN.1273 —	26015 —	1E12-3 —	101 —	00 —	3 / 8

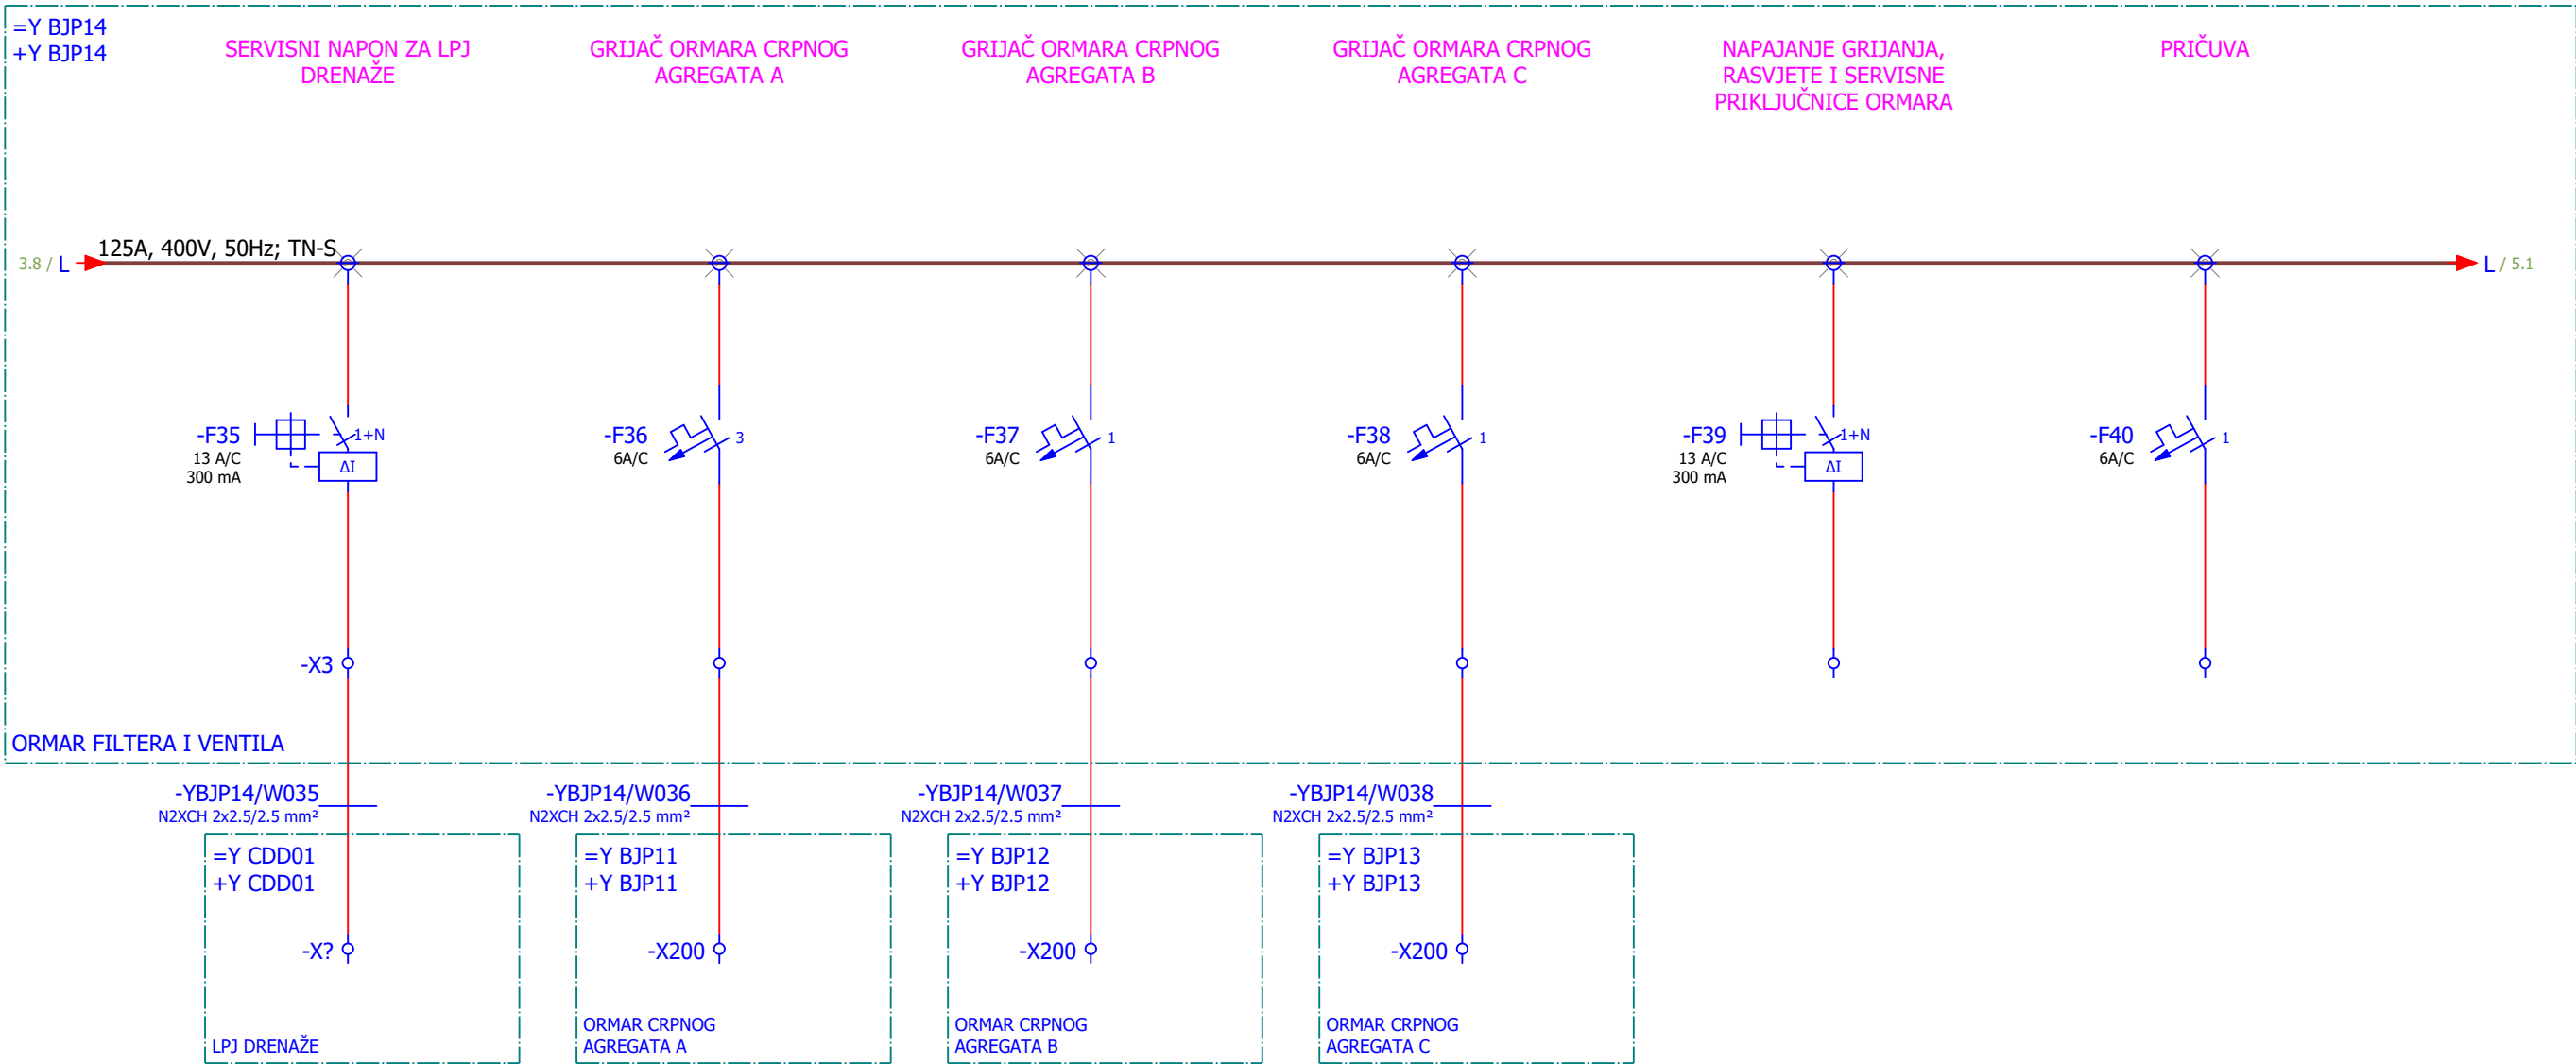


01	Za izradu	2026-08-26	Tamara Trogrić
00	Radna verzija	2026-07-31	Tamara Trogrić
REV. Rev.	NAPOMENA Note	DATUM Date	IZRADIO Drawn

 SINTAKSA A Voith Company Sintaksa d.o.o. Ulica Domovinskog rata 104C, 21 000 Split, Tuškanova 37, 10000 Zagreb T: +385 1 2310 273 info@sintaksa.hr www.sintaksa.hr			NAZIV PROJEKTA / POSLA: <i>Project / job name</i>		REKONSTRUKCIJA HE SENJ - FAZA I.													
PROJEKTANT: <i>Design engineer</i>			Patrik Kovač, mag. ing. el. techn. inf.		INVESTITOR / PODNOŠITELJ ZAHTEVA: <i>Investor</i>		HRVATSKA ELEKTROPRIVREDA d.o.o Ulica grada Vukovara 37, 10000 Zagreb, OIB: 28921978587											
IZRADIO: <i>Drawn</i>			Tamara Trogrić, mag. ing. el. techn. inf.		GRAĐEVINA / ZAHVAT U PROSTORU: <i>Object</i>		HE Senj Na katastarskim česticama k.o. Sveti Juraj, k.o. Melnice i k.o. Brlog											
KONTROLIRAO: <i>Checked</i>			Patrik Kovač, mag. ing. el. techn. inf.		PROJEKTIRANI DIO: <i>Scope of design</i>		STROJARSKI PROJEKT											
GLAVNI PROJEKTANT: <i>Design manager</i>			Natko Vučković, dipl.ing.el.		RAZINA-STRUKA: <i>Design type</i>		IZVEDBENI PROJEKT											
MJESTO I DATUM: <i>Place and date</i>			Zagreb, 2026-07-31		SADRŽAJ: <i>Content</i>		JEDNOPOLNA SHEMA											
OZNAKA NACRTA <i>Drawing designation</i>			FORMAT <i>Paper size</i>		MJERILO <i>Scale</i>													
26015-DD-EE-01-101-00			A3		1:10		ZOP <i>Com. pr. des.</i>		PROJEKT <i>Project</i>		MAPA <i>Folder</i>		PRILOG <i>Drawing</i>		REVIZIJA <i>Revision</i>		LIST <i>Page</i>	
							SEN.1273 —		26015 —		1E12-3 —		101 —		00 —		4 / 8	

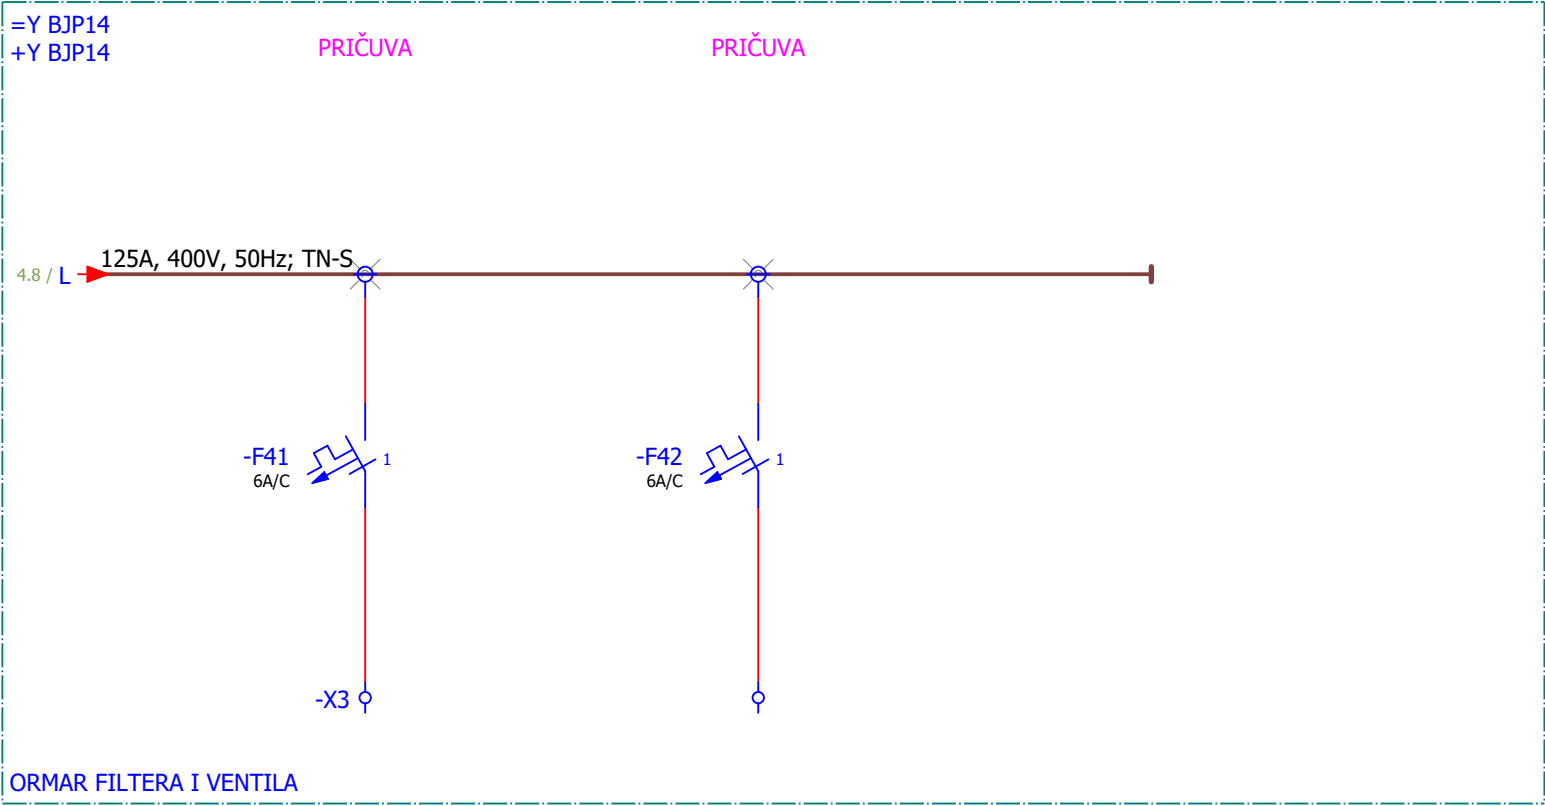


01	Za izradu	2026-08-26	Tamara Trogrić
00	Radna verzija	2026-07-31	Tamara Trogrić
REV. Rev.	NAPOMENA Note	DATUM Date	IZRADIO Drawn

 SINTAKSA A Voith Company Sintaksa d.o.o. Ulica Domovinskog rata 104C, 21 000 Split, Tuškanova 37, 10000 Zagreb T: +385 1 2310 273 info@sintaksa.hr www.sintaksa.hr			NAZIV PROJEKTA / POSLA: <i>Project / job name</i>			REKONSTRUKCIJA HE SENJ - FAZA I.													
PROJEKTANT: <i>Design engineer</i>			Patrik Kovač, mag. ing. el. techn. inf.			INVESTITOR / PODNOŠITELJ ZAHTJEVA: <i>Investor</i>			HRVATSKA ELEKTROPRIVREDA d.o.o Ulica grada Vukovara 37, 10000 Zagreb, OIB: 28921978587										
IZRADIO: <i>Drawn</i>			Tamara Trogrić, mag. ing. el. techn. inf.			GRAĐEVINA / ZAHVAT U PROSTORU: <i>Object</i>			HE Senj Na katastarskim česticama k.o. Sveti Juraj, k.o. Melnice i k.o. Brlog										
KONTROLIRAO: <i>Checked</i>			Patrik Kovač, mag. ing. el. techn. inf.			PROJEKTIRANI DIO: <i>Scope of design</i>			STROJARSKI PROJEKT										
GLAVNI PROJEKTANT: <i>Design manager</i>			Natko Vučković, dipl.ing.el.			RAZINA-STRUKA: <i>Design type</i>			IZVEDBENI PROJEKT										
MJESTO I DATUM: <i>Place and date</i>			Zagreb, 2026-07-31			SADRŽAJ: <i>Content</i>			JEDNOPOLNA SHEMA										
OZNAKA NACRTA <i>Drawing designation</i>			FORMAT <i>Paper size</i>			MJERILO <i>Scale</i>			ZOP <i>Com. pr. des.</i>	PROJEKT <i>Project</i>	MAPA <i>Folder</i>	PRILOG <i>Drawing</i>	REVIZIJA <i>Revision</i>	LIST <i>Page</i>					
26015-DD-EE-01-101-00			A3			1:10			SEN.1273	—	26015	—	1E12-3	—	101	—	00	—	5 / 8

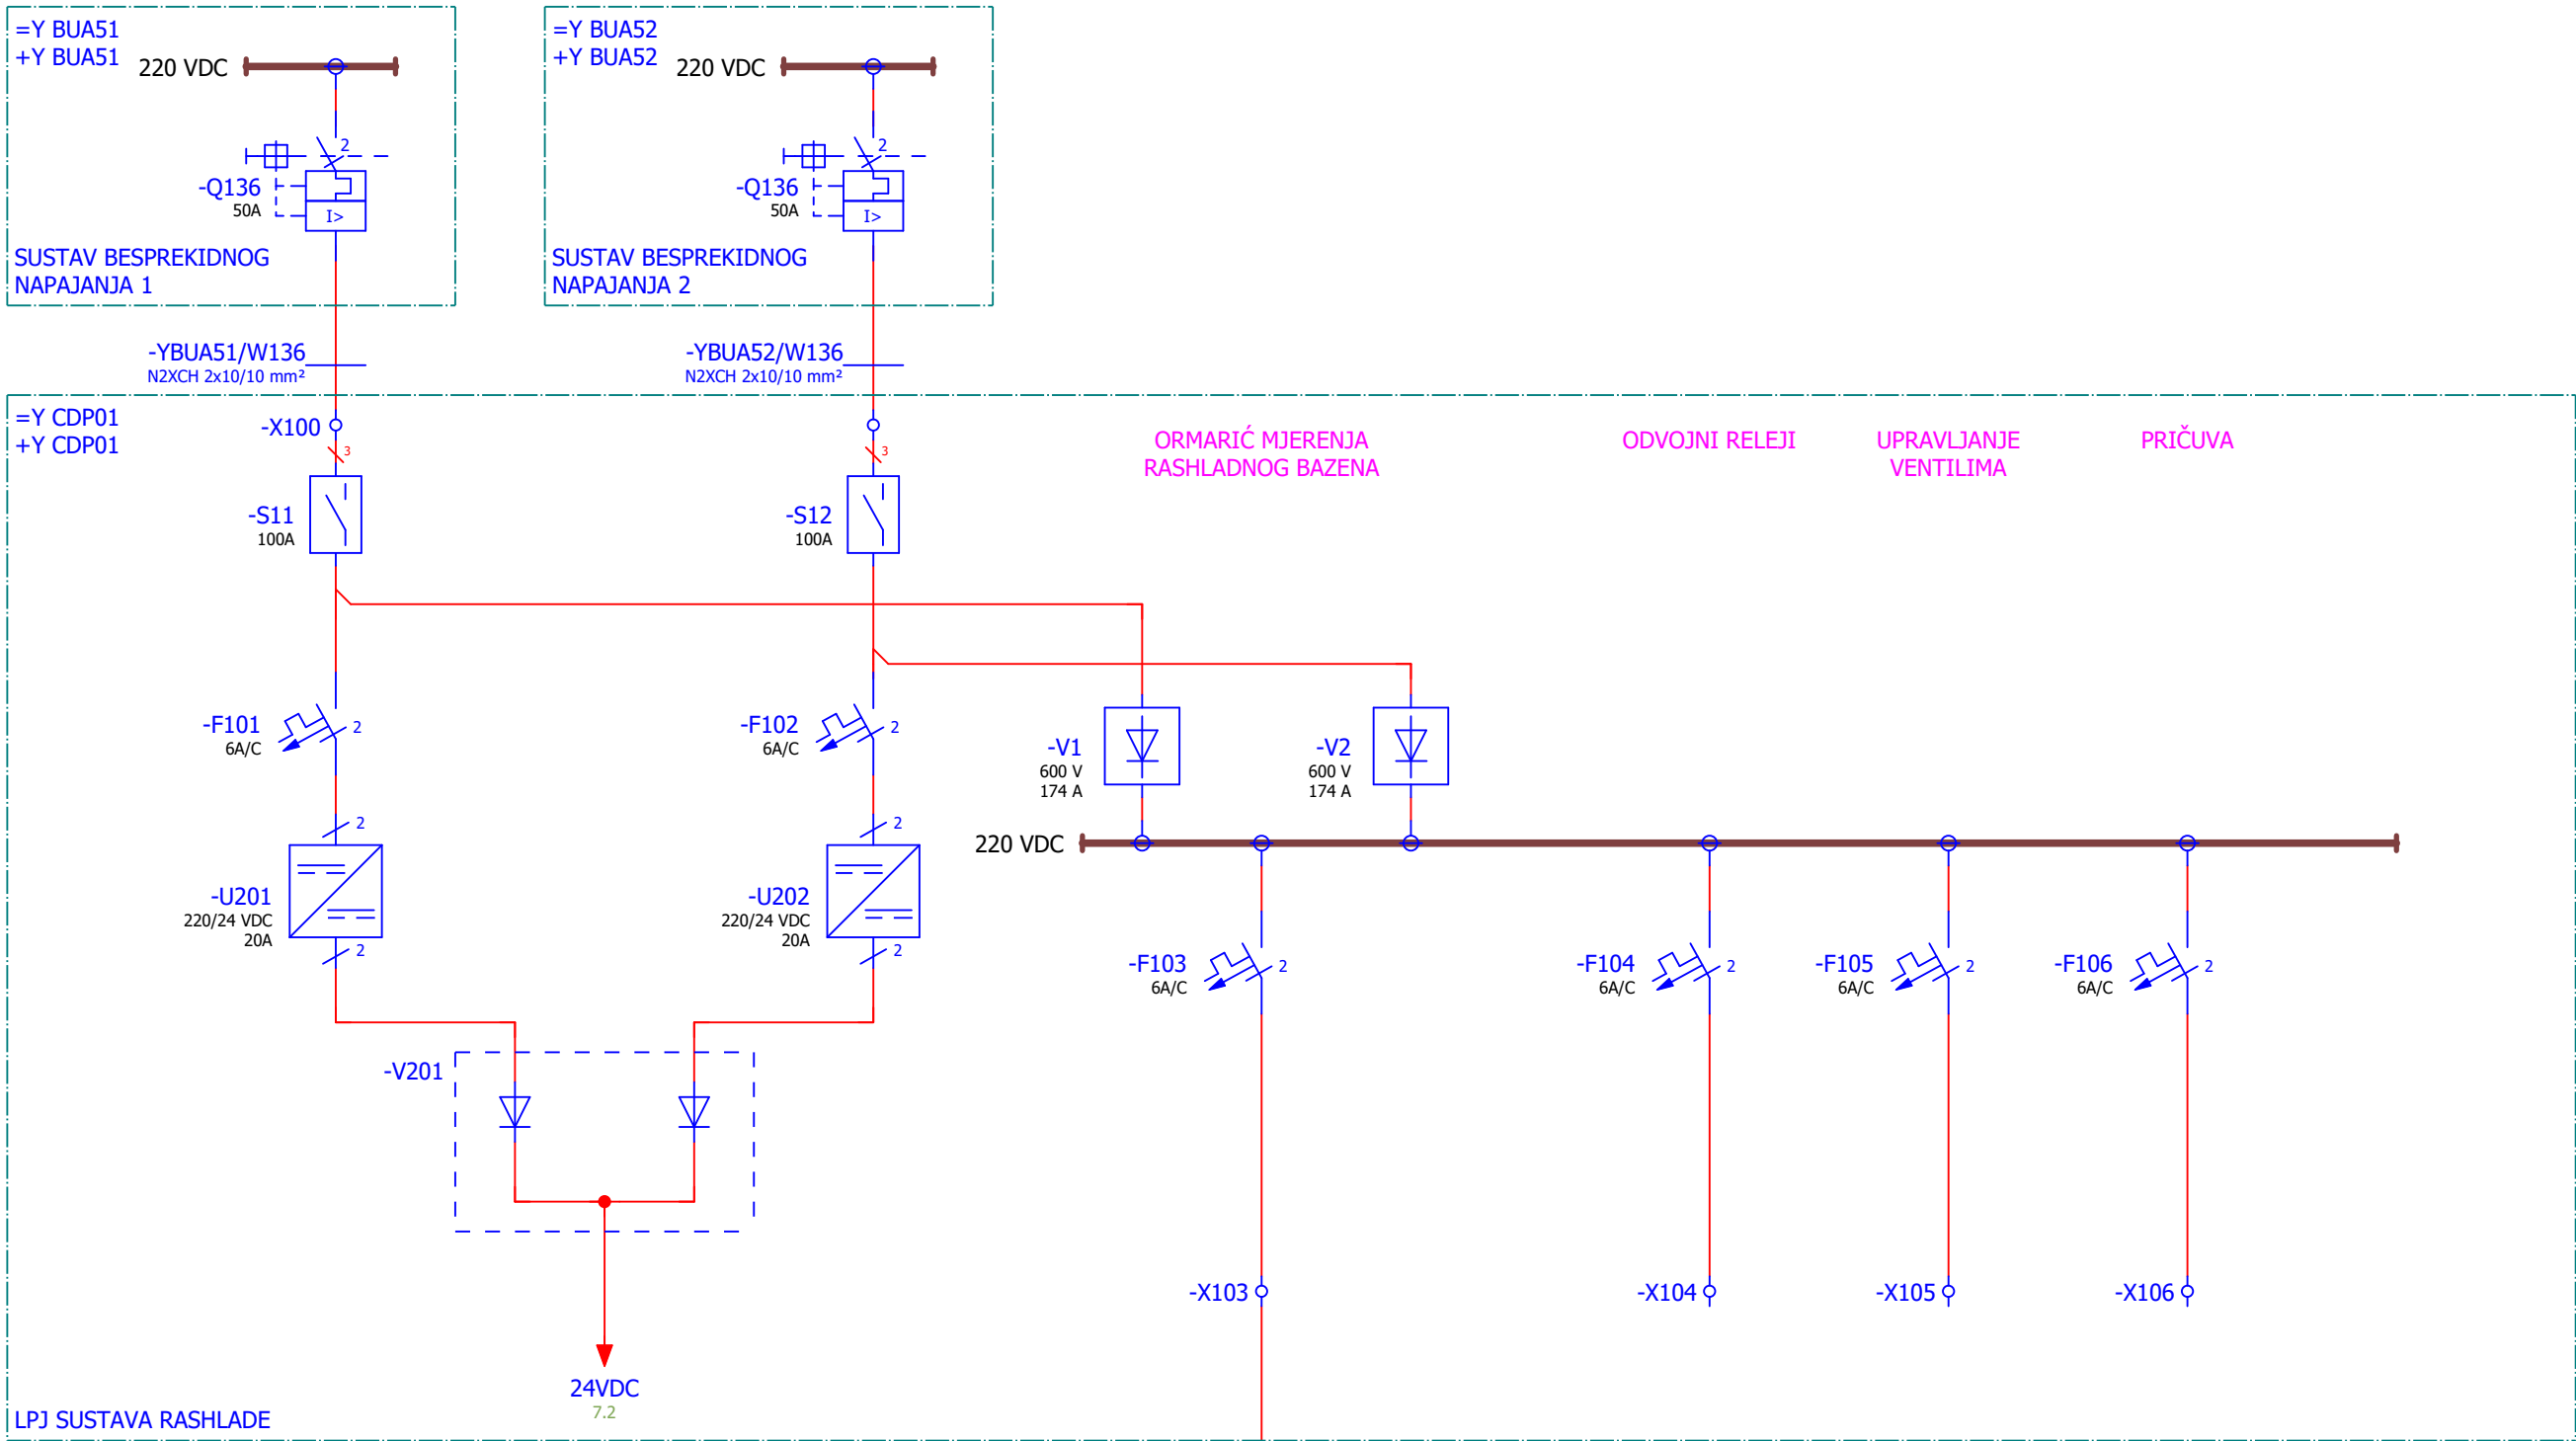


01	Za izradu	2026-08-26	Tamara Trogrić
00	Radna verzija	2026-07-31	Tamara Trogrić
REV. Rev.	NAPOMENA Note	DATUM Date	IZRADIO Drawn

 SINTAKSA A Voith Company Sintaksa d.o.o. Ulica Domovinskog rata 104C, 21 000 Split, Tuškanova 37, 10000 Zagreb T: +385 1 2310 273 info@sintaksa.hr www.sintaksa.hr			NAZIV PROJEKTA / POSLA: <i>Project / job name</i>		REKONSTRUKCIJA HE SENJ - FAZA I.							
PROJEKTANT: <i>Design engineer</i>			Patrik Kovač, mag. ing. el. techn. inf.		INVESTITOR / PODNOŠITELJ ZAHTEVA: <i>Investor</i>		HRVATSKA ELEKTROPRIVREDA d.o.o Ulica grada Vukovara 37, 10000 Zagreb, OIB: 28921978587					
IZRADIO: <i>Drawn</i>			Tamara Trogrić, mag. ing. el. techn. inf.		GRAĐEVINA / ZAHVAT U PROSTORU: <i>Object</i>		HE Senj Na katastarskim česticama k.o. Sveti Juraj, k.o. Melnice i k.o. Brlog					
KONTROLIRAO: <i>Checked</i>			Patrik Kovač, mag. ing. el. techn. inf.		PROJEKTIRANI DIO: <i>Scope of design</i>		STROJARSKI PROJEKT					
GLAVNI PROJEKTANT: <i>Design manager</i>			Natko Vučković, dipl.ing.el.		RAZINA-STRUKA: <i>Design type</i>		IZVEDBENI PROJEKT					
MJESTO I DATUM: <i>Place and date</i>			Zagreb, 2026-07-31		SADRŽAJ: <i>Content</i>		JEDNOPOLNA SHEMA					
OZNAKA NACRTA <i>Drawing designation</i>			FORMAT <i>Paper size</i>		MJERILO <i>Scale</i>		ZOP <i>Com. pr. des.</i>	PROJEKT <i>Project</i>	MAPA <i>Folder</i>	PRILOG <i>Drawing</i>	REVIZIJA <i>Revision</i>	LIST <i>Page</i>
26015-DD-EE-01-101-00			A3		1:10		SEN.1273 —	26015 —	1E12-3 —	101 —	00 —	6 / 8

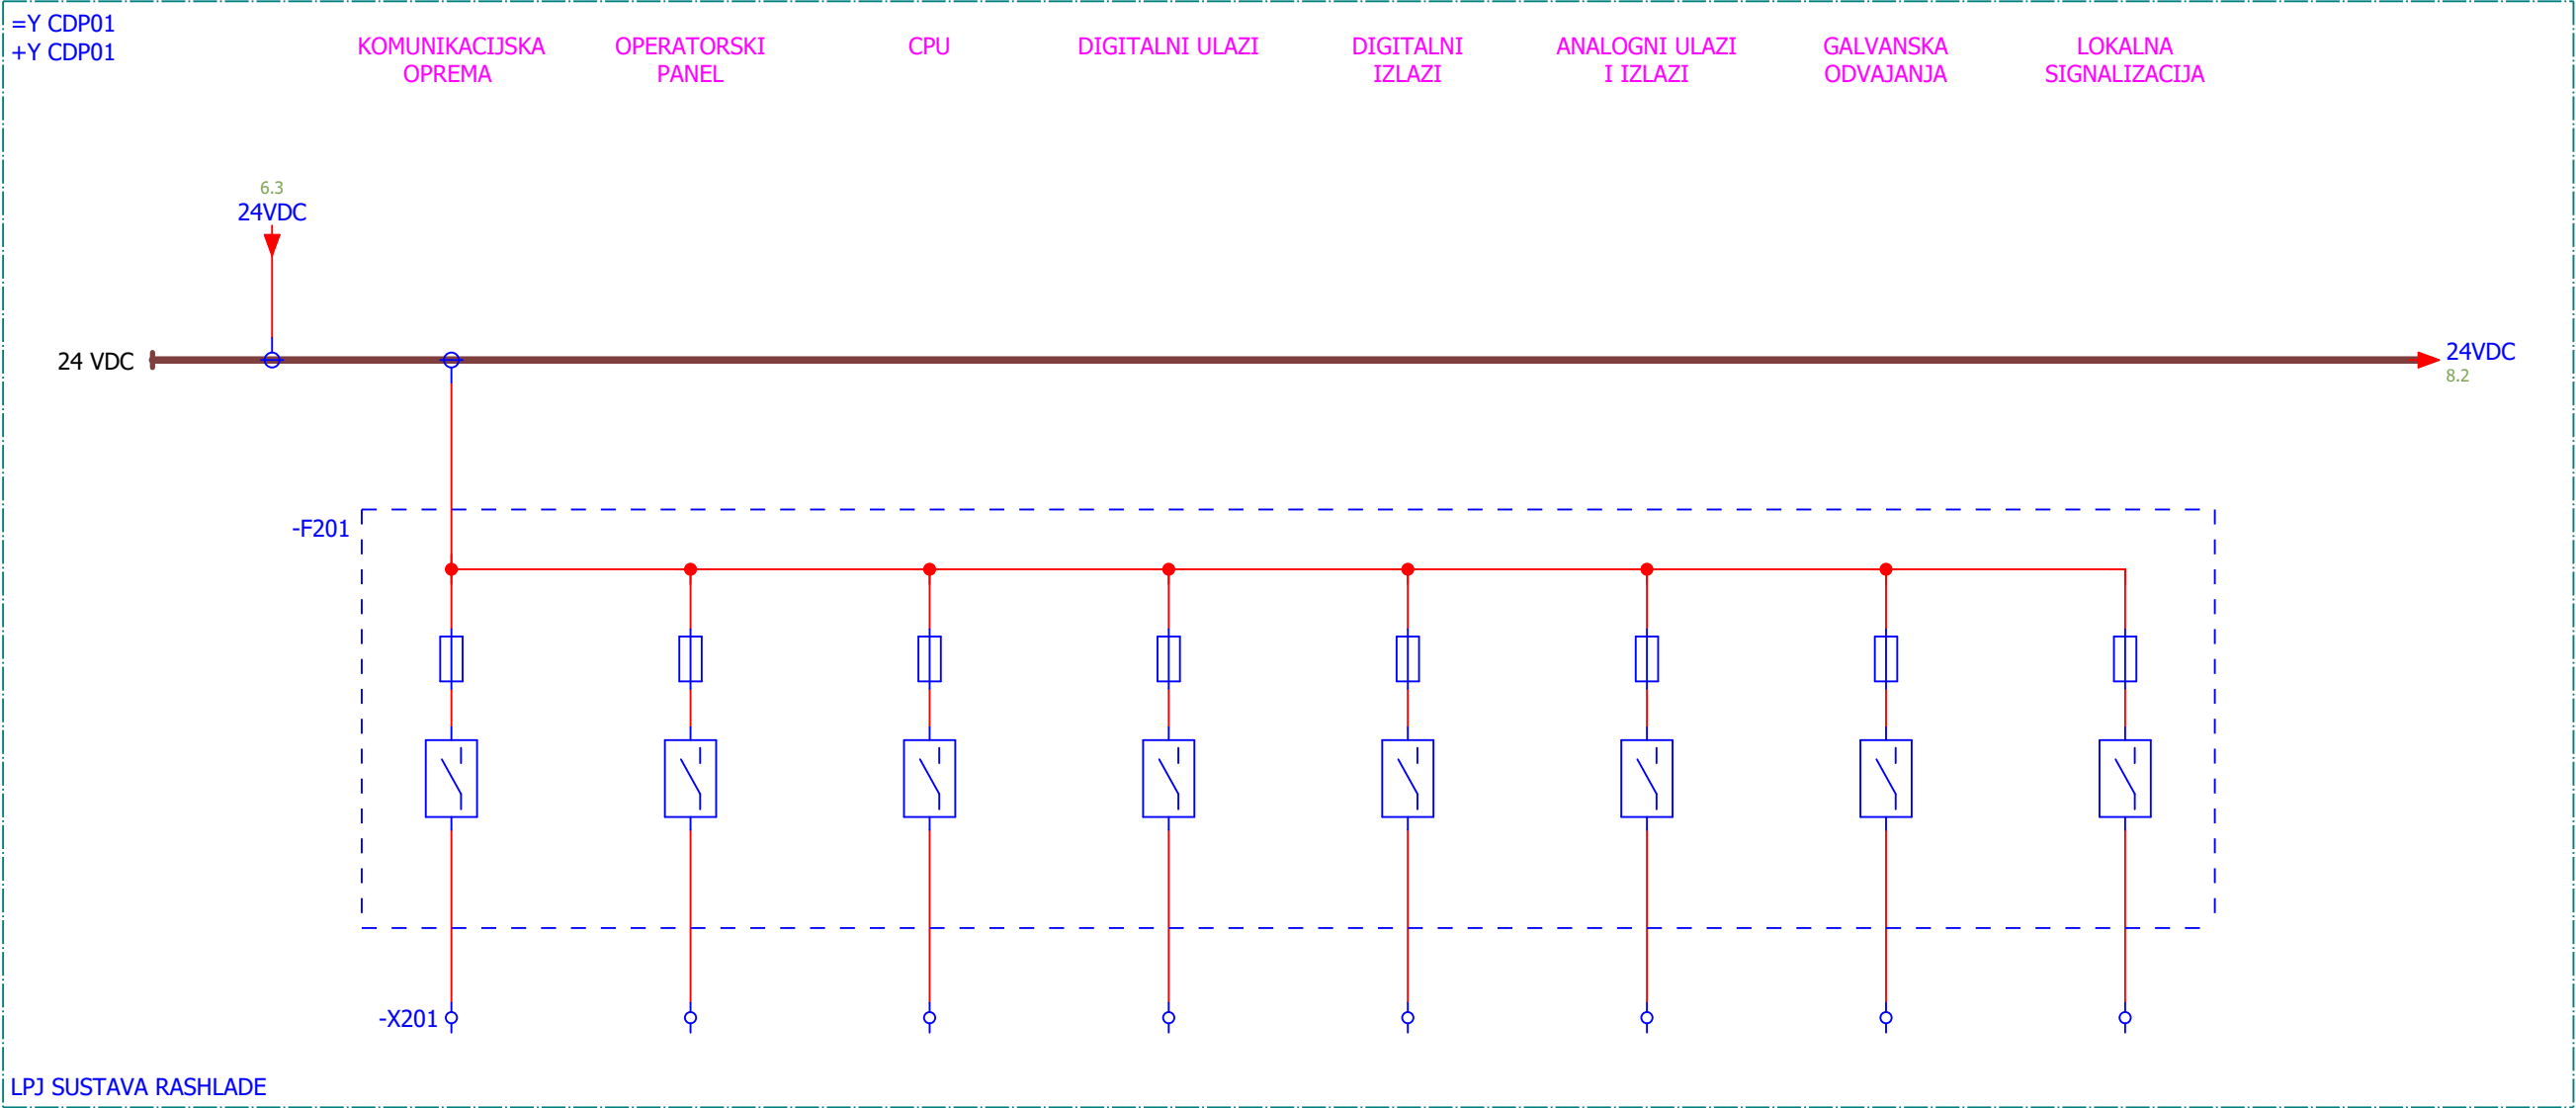

01	Za izradu	2026-08-26	Tamara Trogrić
00	Radna verzija	2026-07-31	Tamara Trogrić
REV. Rev.	NAPOMENA Note	DATUM Date	IZRADIO Drawn

 SINTAKSA A Voith Company Sintaksa d.o.o. Ulica Domovinskog rata 104C, 21 000 Split, Tuškanova 37, 10000 Zagreb T: +385 1 2310 273 info@sintaksa.hr www.sintaksa.hr			NAZIV PROJEKTA / POSLA: <i>Project / job name</i>			REKONSTRUKCIJA HE SENJ - FAZA I.								
PROJEKTANT: <i>Design engineer</i>			Patrik Kovač, mag. ing. el. techn. inf.			INVESTITOR / PODNOŠITELJ ZAHTJEVA: <i>Investor</i>			HRVATSKA ELEKTROPRIVREDA d.o.o Ulica grada Vukovara 37, 10000 Zagreb, OIB: 28921978587					
IZRADIO: <i>Drawn</i>			Tamara Trogrić, mag. ing. el. techn. inf.			GRAĐEVINA / ZAHVAT U PROSTORU: <i>Object</i>			HE Senj Na katastarskim česticama k.o. Sveti Juraj, k.o. Melnice i k.o. Brlog					
KONTROLIRAO: <i>Checked</i>			Patrik Kovač, mag. ing. el. techn. inf.			PROJEKTIRANI DIO: <i>Scope of design</i>			STROJARSKI PROJEKT					
GLAVNI PROJEKTANT: <i>Design manager</i>			Natko Vučković, dipl.ing.el.			RAZINA-STRUKA: <i>Design type</i>			IZVEDBENI PROJEKT					
MJESTO I DATUM: <i>Place and date</i>			Zagreb, 2026-07-31			SADRŽAJ: <i>Content</i>			JEDNOPOLNA SHEMA					
OZNAKA NACRTA <i>Drawing designation</i>		FORMAT <i>Paper size</i>	MJERILO <i>Scale</i>		ZOP <i>Com. pr. des.</i>	PROJEKT <i>Project</i>	MAPA <i>Folder</i>	PRILOG <i>Drawing</i>	REVIZIJA <i>Revision</i>	LIST <i>Page</i>				
26015-DD-EE-01-101-00		A3	1:10		SEN.1273 —	26015 —	1E12-3 —	101 —	00 —	7 / 8				

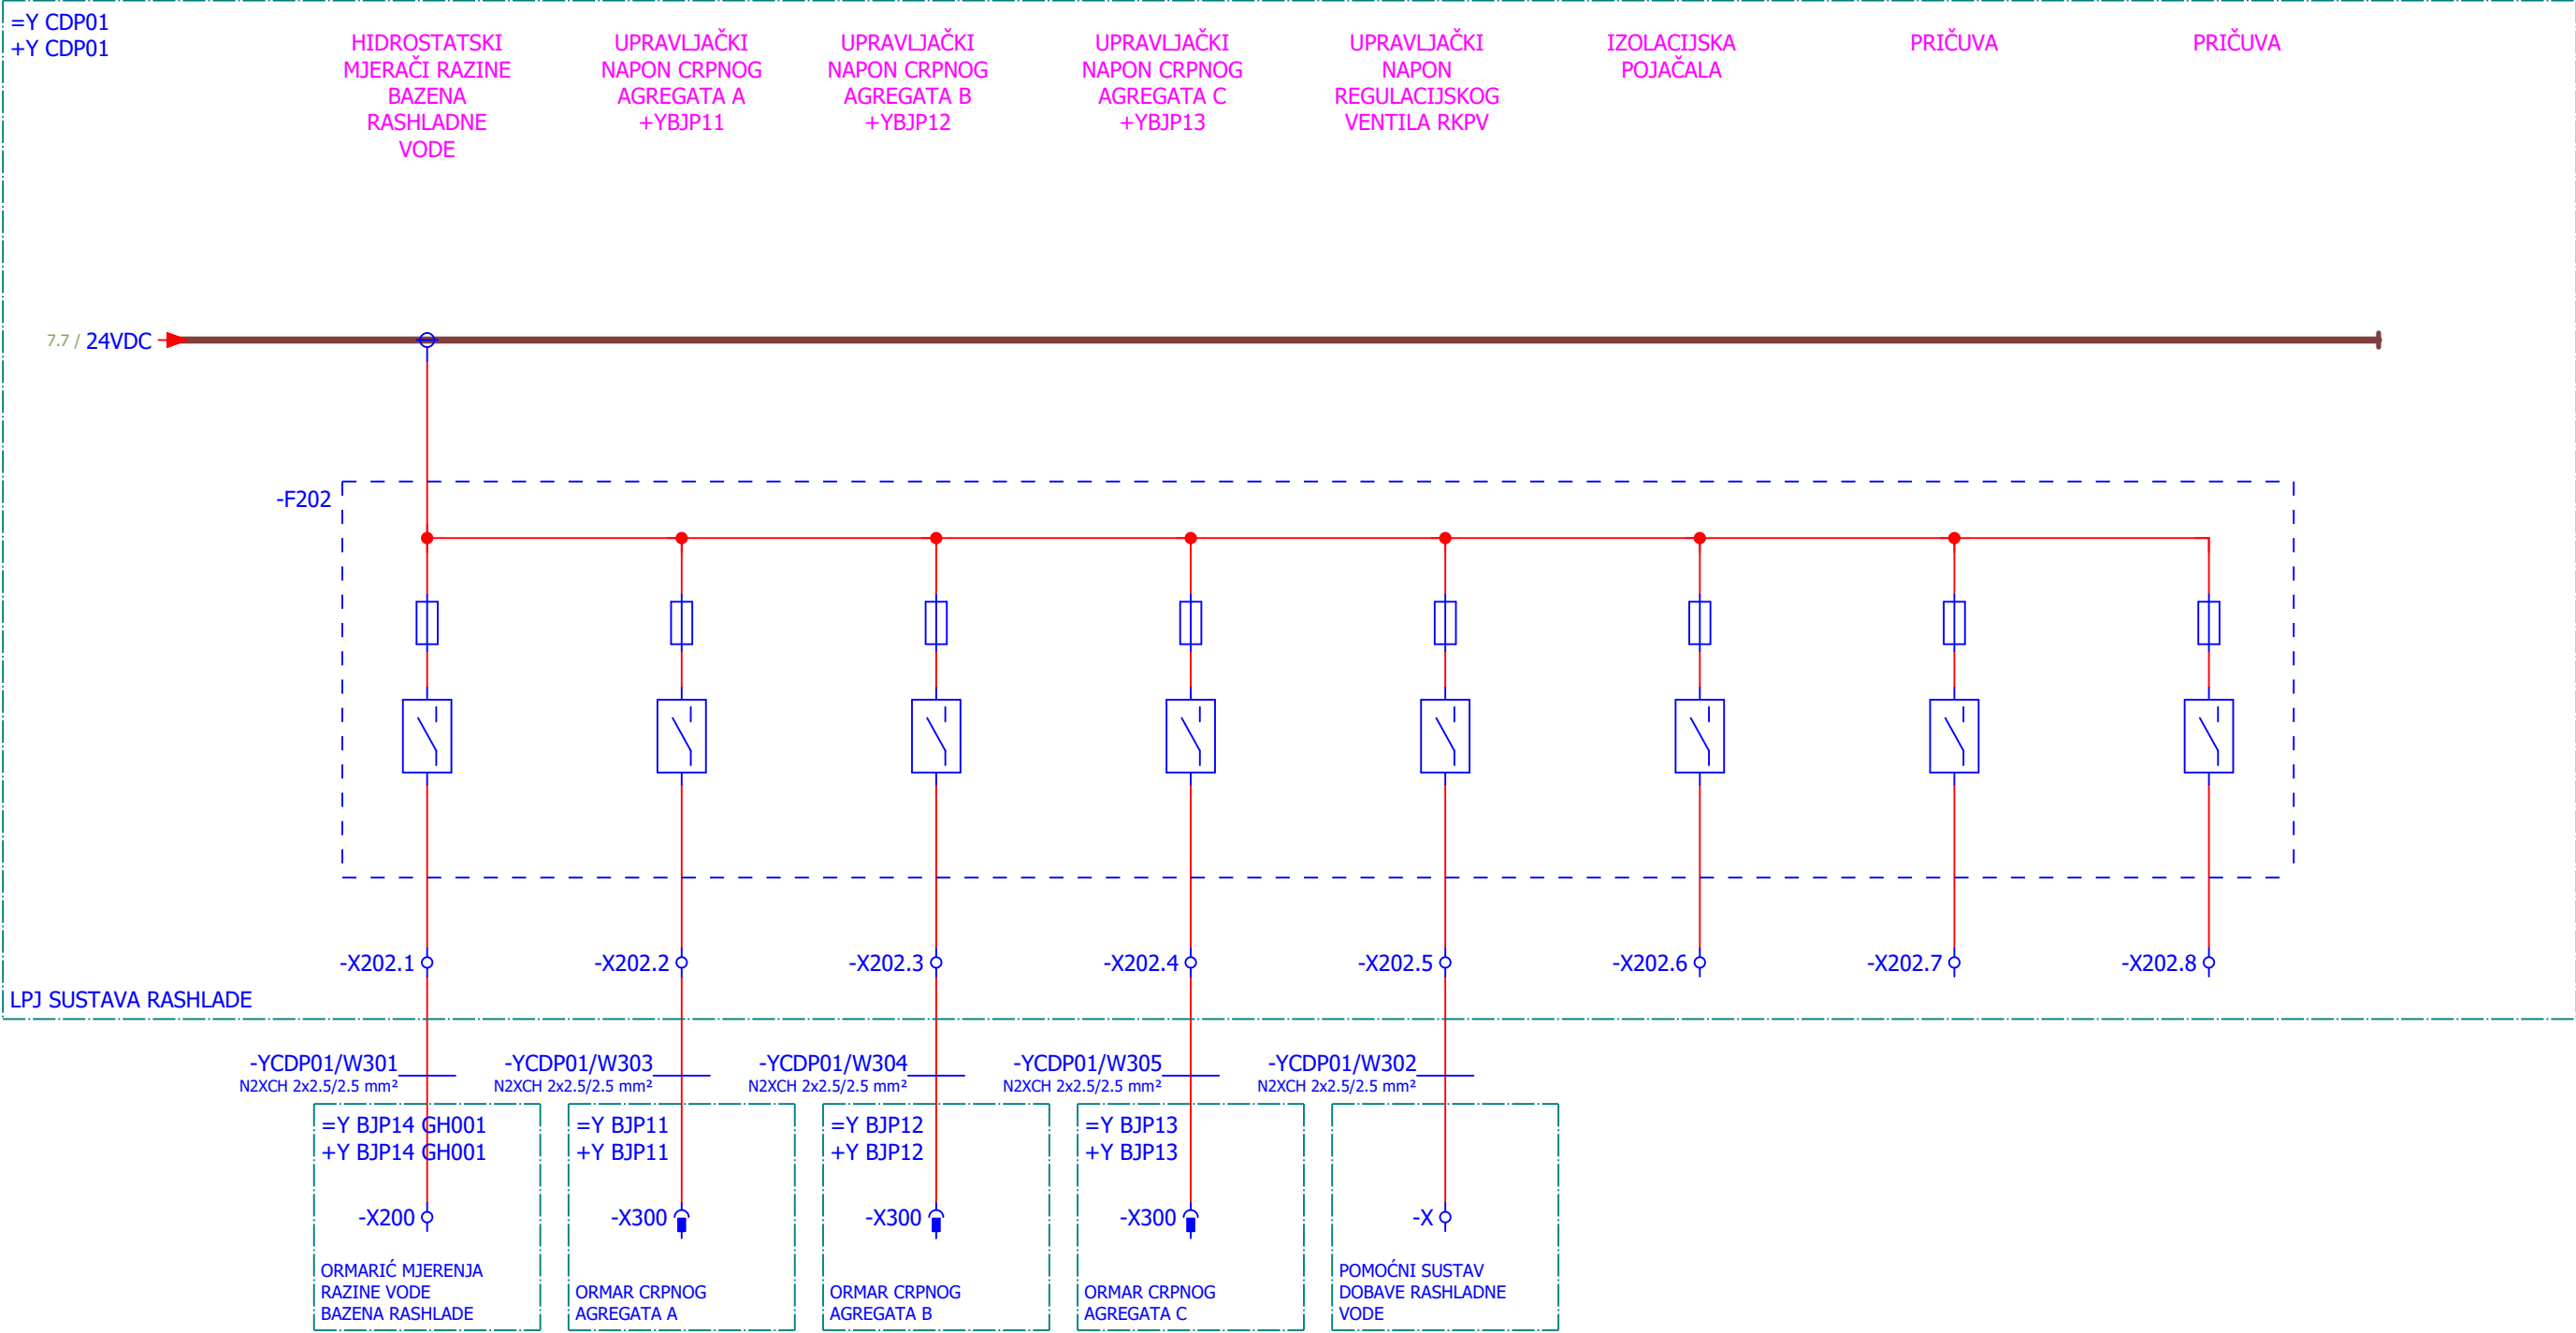

01	Za izradu	2026-08-26	Tamara Trogrić
00	Radna verzija	2026-07-31	Tamara Trogrić
REV. Rev.	NAPOMENA Note	DATUM Date	IZRADIO Drawn

SINTAKSA A Voith Company			Sintaksa d.o.o. Ulica Domovinskog rata 104C, 21 000 Split, Tuškanova 37, 10000 Zagreb T: +385 1 2310 273 info@sintaksa.hr www.sintaksa.hr			NAZIV PROJEKTA / POSLA: <i>Project / job name</i>			REKONSTRUKCIJA HE SENJ - FAZA I.																	
PROJEKTANT: <i>Design engineer</i>			Patrik Kovač, mag. ing. el. techn. inf.			INVESTITOR / PODNOŠITELJ ZAHTEJEVA: <i>Investor</i>			HRVATSKA ELEKTROPRIVREDA d.o.o Ulica grada Vukovara 37, 10000 Zagreb, OIB: 28921978587																	
IZRADIO: <i>Drawn</i>			Tamara Trogrić, mag. ing. el. techn. inf.			GRADJEVINA / ZAHVAT U PROSTORU: <i>Object</i>			HE Senj Na katastarskim česticama k.o. Sveti Juraj, k.o. Melnice i k.o. Brlog																	
KONTROLIRAO: <i>Checked</i>			Patrik Kovač, mag. ing. el. techn. inf.			PROJEKTIRANI DIO: <i>Scope of design</i>			STROJARSKI PROJEKT																	
GLAVNI PROJEKTANT: <i>Design manager</i>			Natko Vučković, dipl.ing.el.			RAZINA-STRUKA: <i>Design type</i>			IZVEDBENI PROJEKT																	
MJESTO I DATUM: <i>Place and date</i>			Zagreb, 2026-07-31			SADRŽAJ: <i>Content</i>			JEDNOPOLNA SHEMA																	
OZNAKA NACRTA <i>Drawing designation</i>			FORMAT <i>Paper size</i>			MJERILO <i>Scale</i>			ZOP <i>Com. pr. des.</i>			PROJEKT <i>Project</i>			MAPA <i>Folder</i>			PRILOG <i>Drawing</i>			REVIZIJA <i>Revision</i>			LIST <i>Page</i>		
26015-DD-EE-01-101-00			A3			1:10			SEN.1273 —			26015 —			1E12-3 —			101 —			00 —			8 / 8		