



VISTA FRONTAL

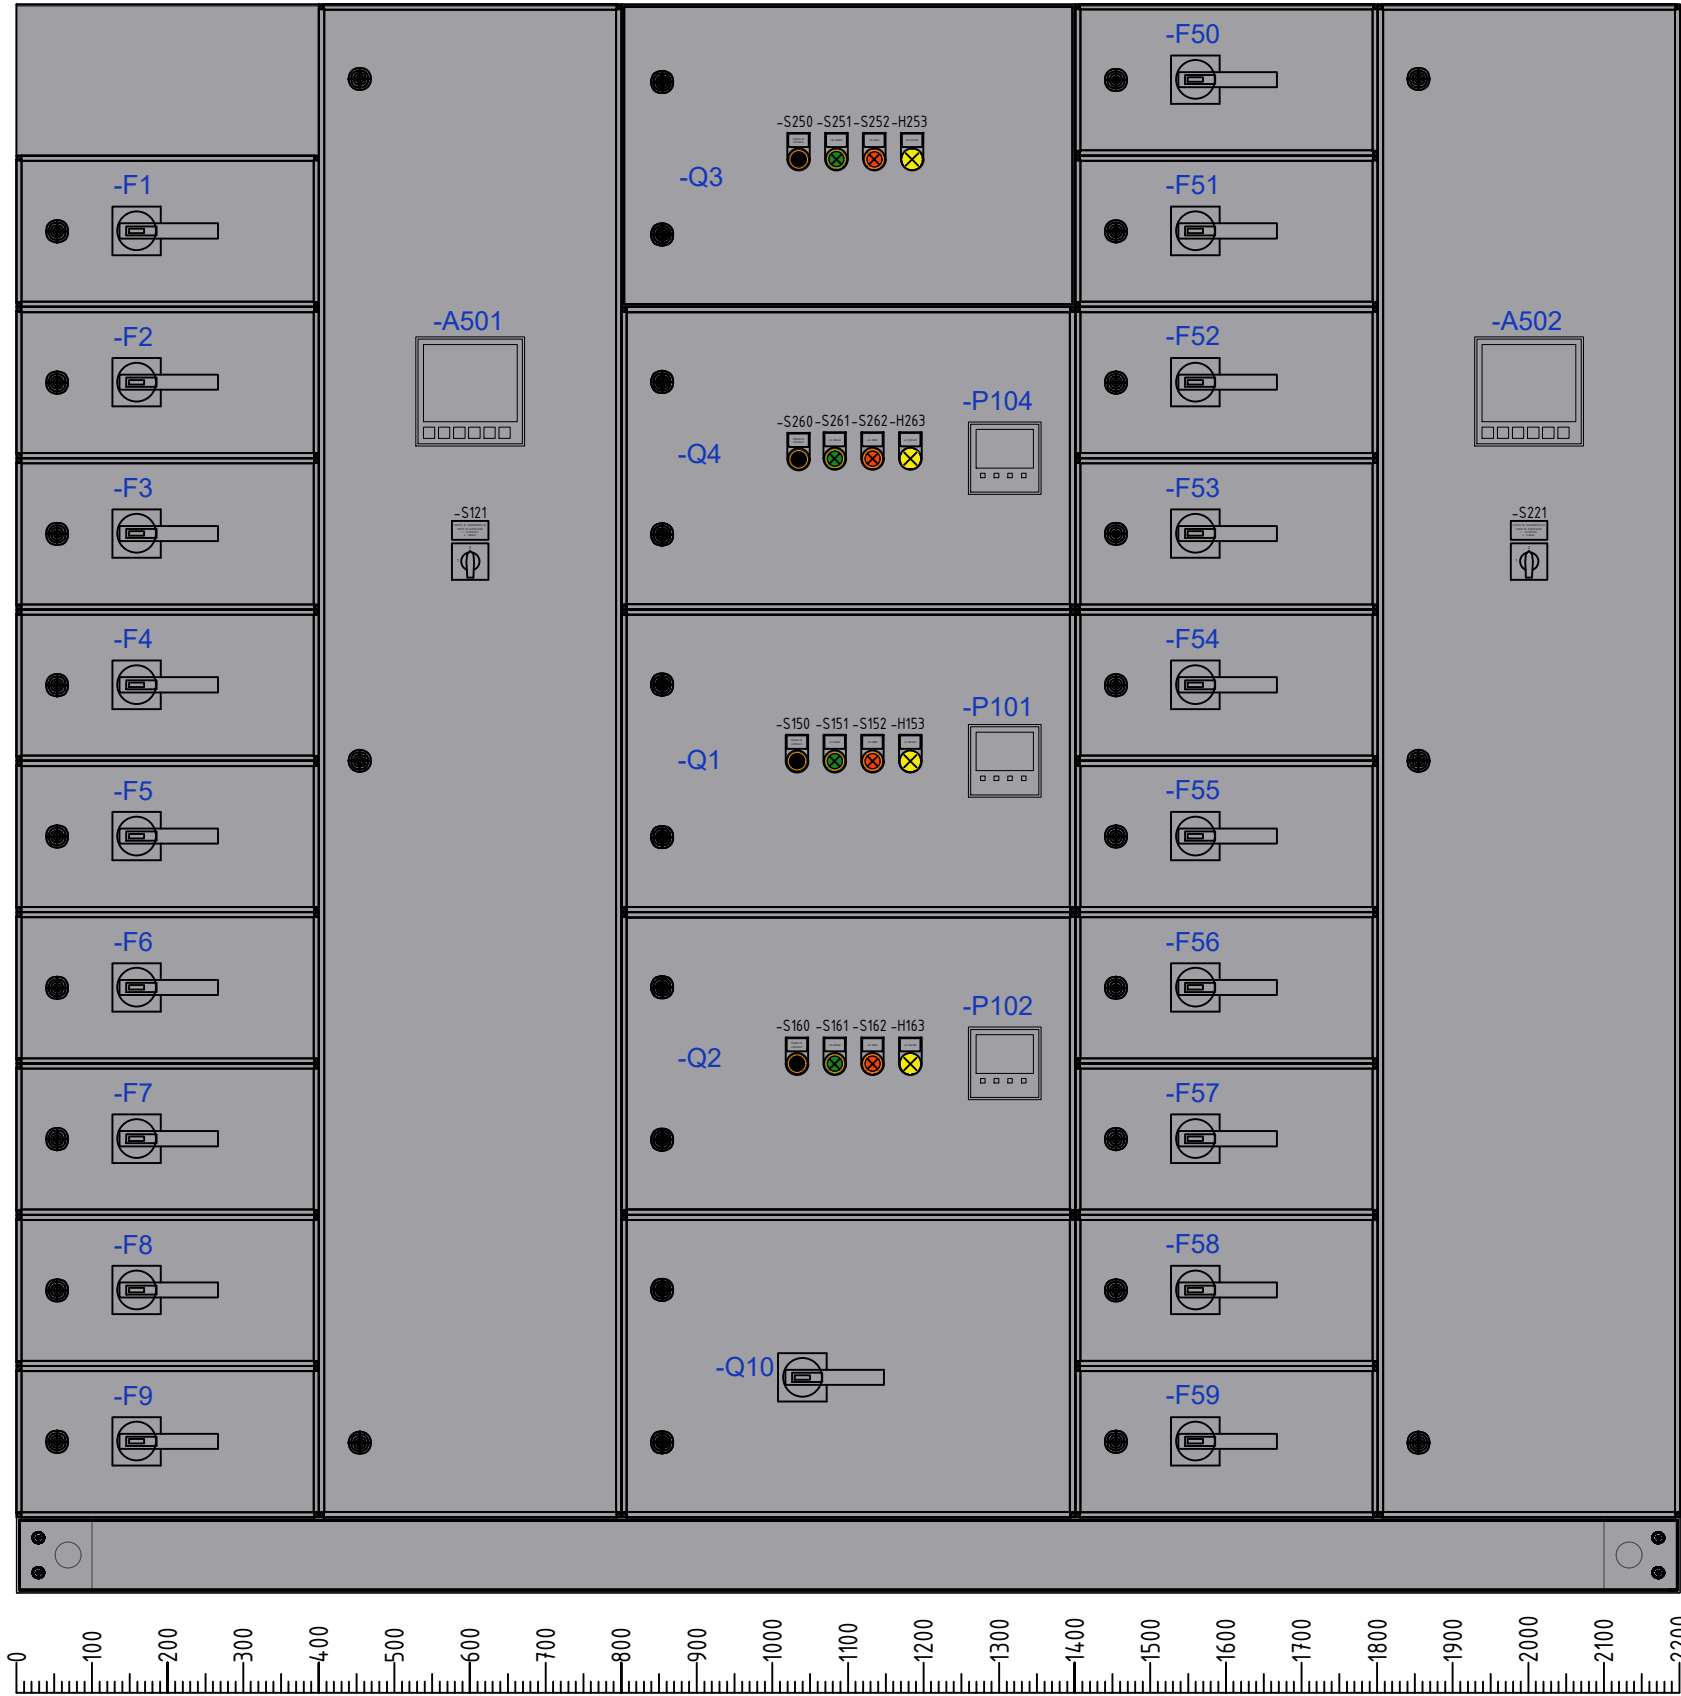

VISTA LATERAL

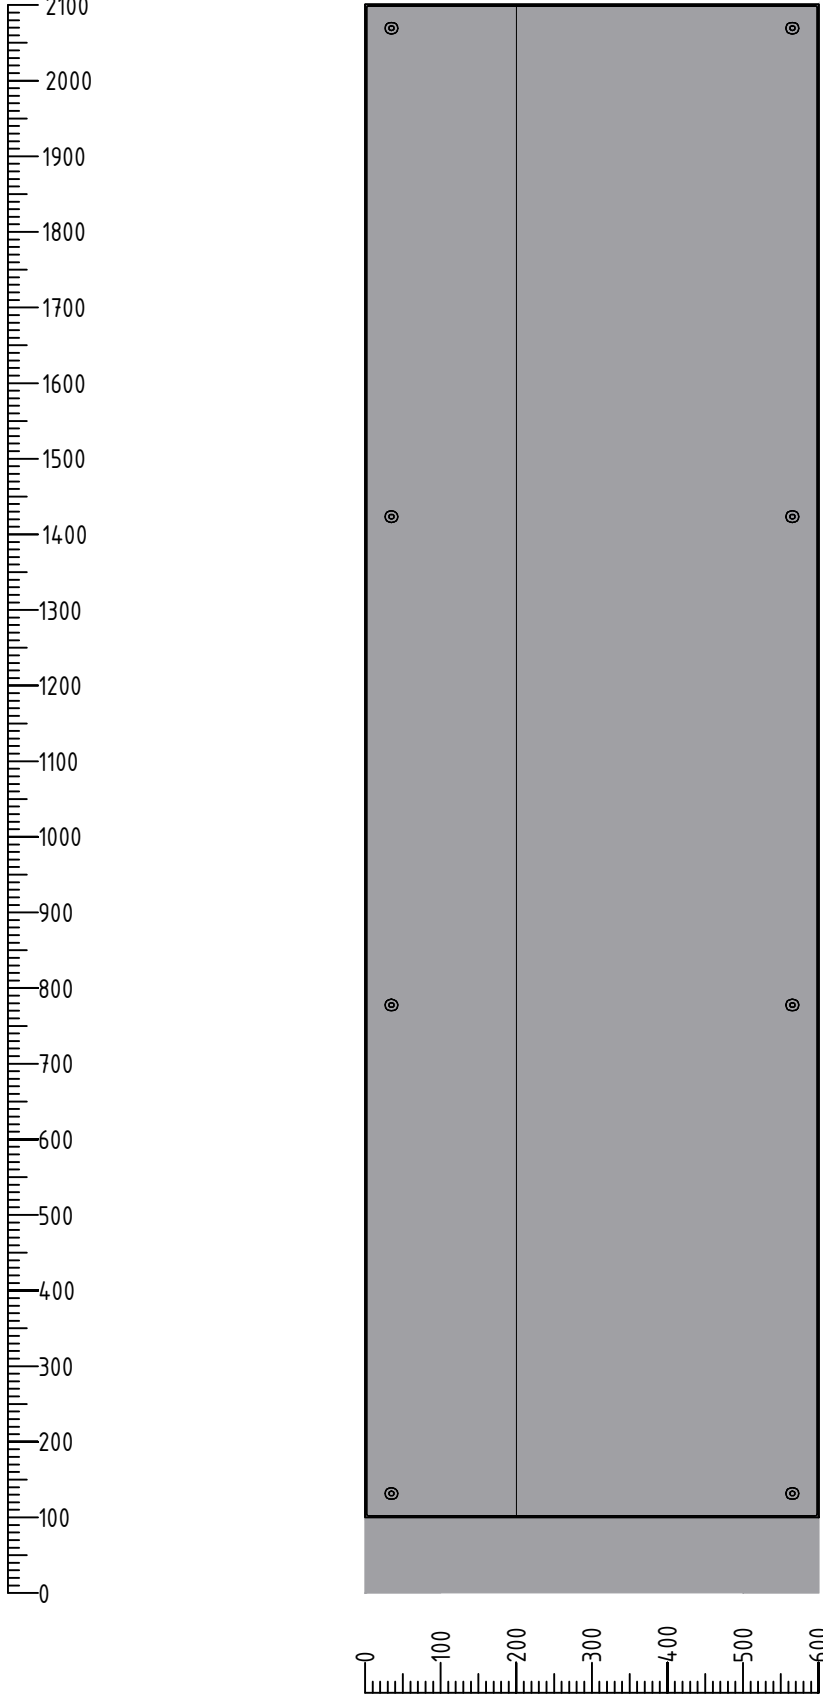

				Dibujado: Bruno Bijelić, mag. ing. el.			 Sintaksa d.o.o. SPLIT: Brza cesta 4, 21210 Mravince ZAGREB: Tuškanova 37, 10000 Zagreb T: +385 1 2310 273 info@sintaksa.hr www.sintaksa.hr					Objeto: PCH NARE Colombia
01	Propuesta revisada	2025-10-14	Bruno Bijelić	Aprobado: Dražen Plavčić, dipl. ing. el.								Alcance del dir.: Sistema de suministro de CA auxiliar
00	La primera versión	2025-03-19	Bruno Bijelić	Lugar y fecha: Zagreb, 2025-03-19			Cliente: VOITH HYDRO S. L. Poligono Apatta Baratzondo 1, Ibarra, Spain					Tipo de diseño: Diseño de detalle
Rev.	Nota	Fecha	Dibujado	Designación del dibujo 24028-DD-EE-03-222-01	Formato A3	Escala 1:10	Proyecto 24028-DD	Directorio EE-03	Dibujo 222	Revisión 01	Hoja 1 / 2	Contenido: DISTRIBUCIÓN DE CA PRINCIPAL +0BFA01 y +0BFA02 - PLANO DEL CUADRO DEL CUBÍCULOS

VISTA INTERIOR - SECCIÓN DE BARRAS COLECTORAS ESENCIALES Y NO ESENCIALES



Leyenda

Sección no esencial

Sección esencial

Barras colectoras de Cu

				Dibujado: Bruno Bijelić, mag. ing. el.			 SINTAKSA A Voith Company Sintaksa d.o.o. SPLIT: Brza cesta 4, 21210 Mravince ZAGREB: Tuškanova 37, 10000 Zagreb T: +385 1 2310 273 info@sintaksa.hr www.sintaksa.hr					Objeto: PCH NARE Colombia
01	Propuesta revisada	2025-10-14	Bruno Bijelić	Aprobado: Dražen Plavčić, dipl. ing. el.								Alcance del dir.: Sistema de suministro de CA auxiliar
00	La primera versión	2025-03-19	Bruno Bijelić	Lugar y fecha: Zagreb, 2025-03-19			Cliente: VOITH HYDRO S. L. Poligono Apatta Baratzondo 1, Ibarra, Spain					Tipo de diseño: Diseño de detalle
Rev.	Nota	Fecha	Dibujado	Designación del dibujo 24028-DD-EE-03-222-01	Formato A3	Escala 1:10	Proyecto 24028-DD	Directorio EE-03	Dibujo 222	Revisión 01	Hoja 2 / 2	Contenido: DISTRIBUCIÓN DE CA PRINCIPAL +0BFA01 y +0BFA02 - PLANO DEL CUADRO DEL CUBÍCULOS