1	2	3	4	5	6	7	8

BAZEN RASHLADNE VODE - RAZINA VODE

BAZEN RASHLADNE VODE - RAZINA VODE - REDUNDANTNO MJERENJE

DONJA VODA - VODLJIVOST VODE AGREGATA A

DONJA VODA - VODLJIVOST VODE AGREGATA B

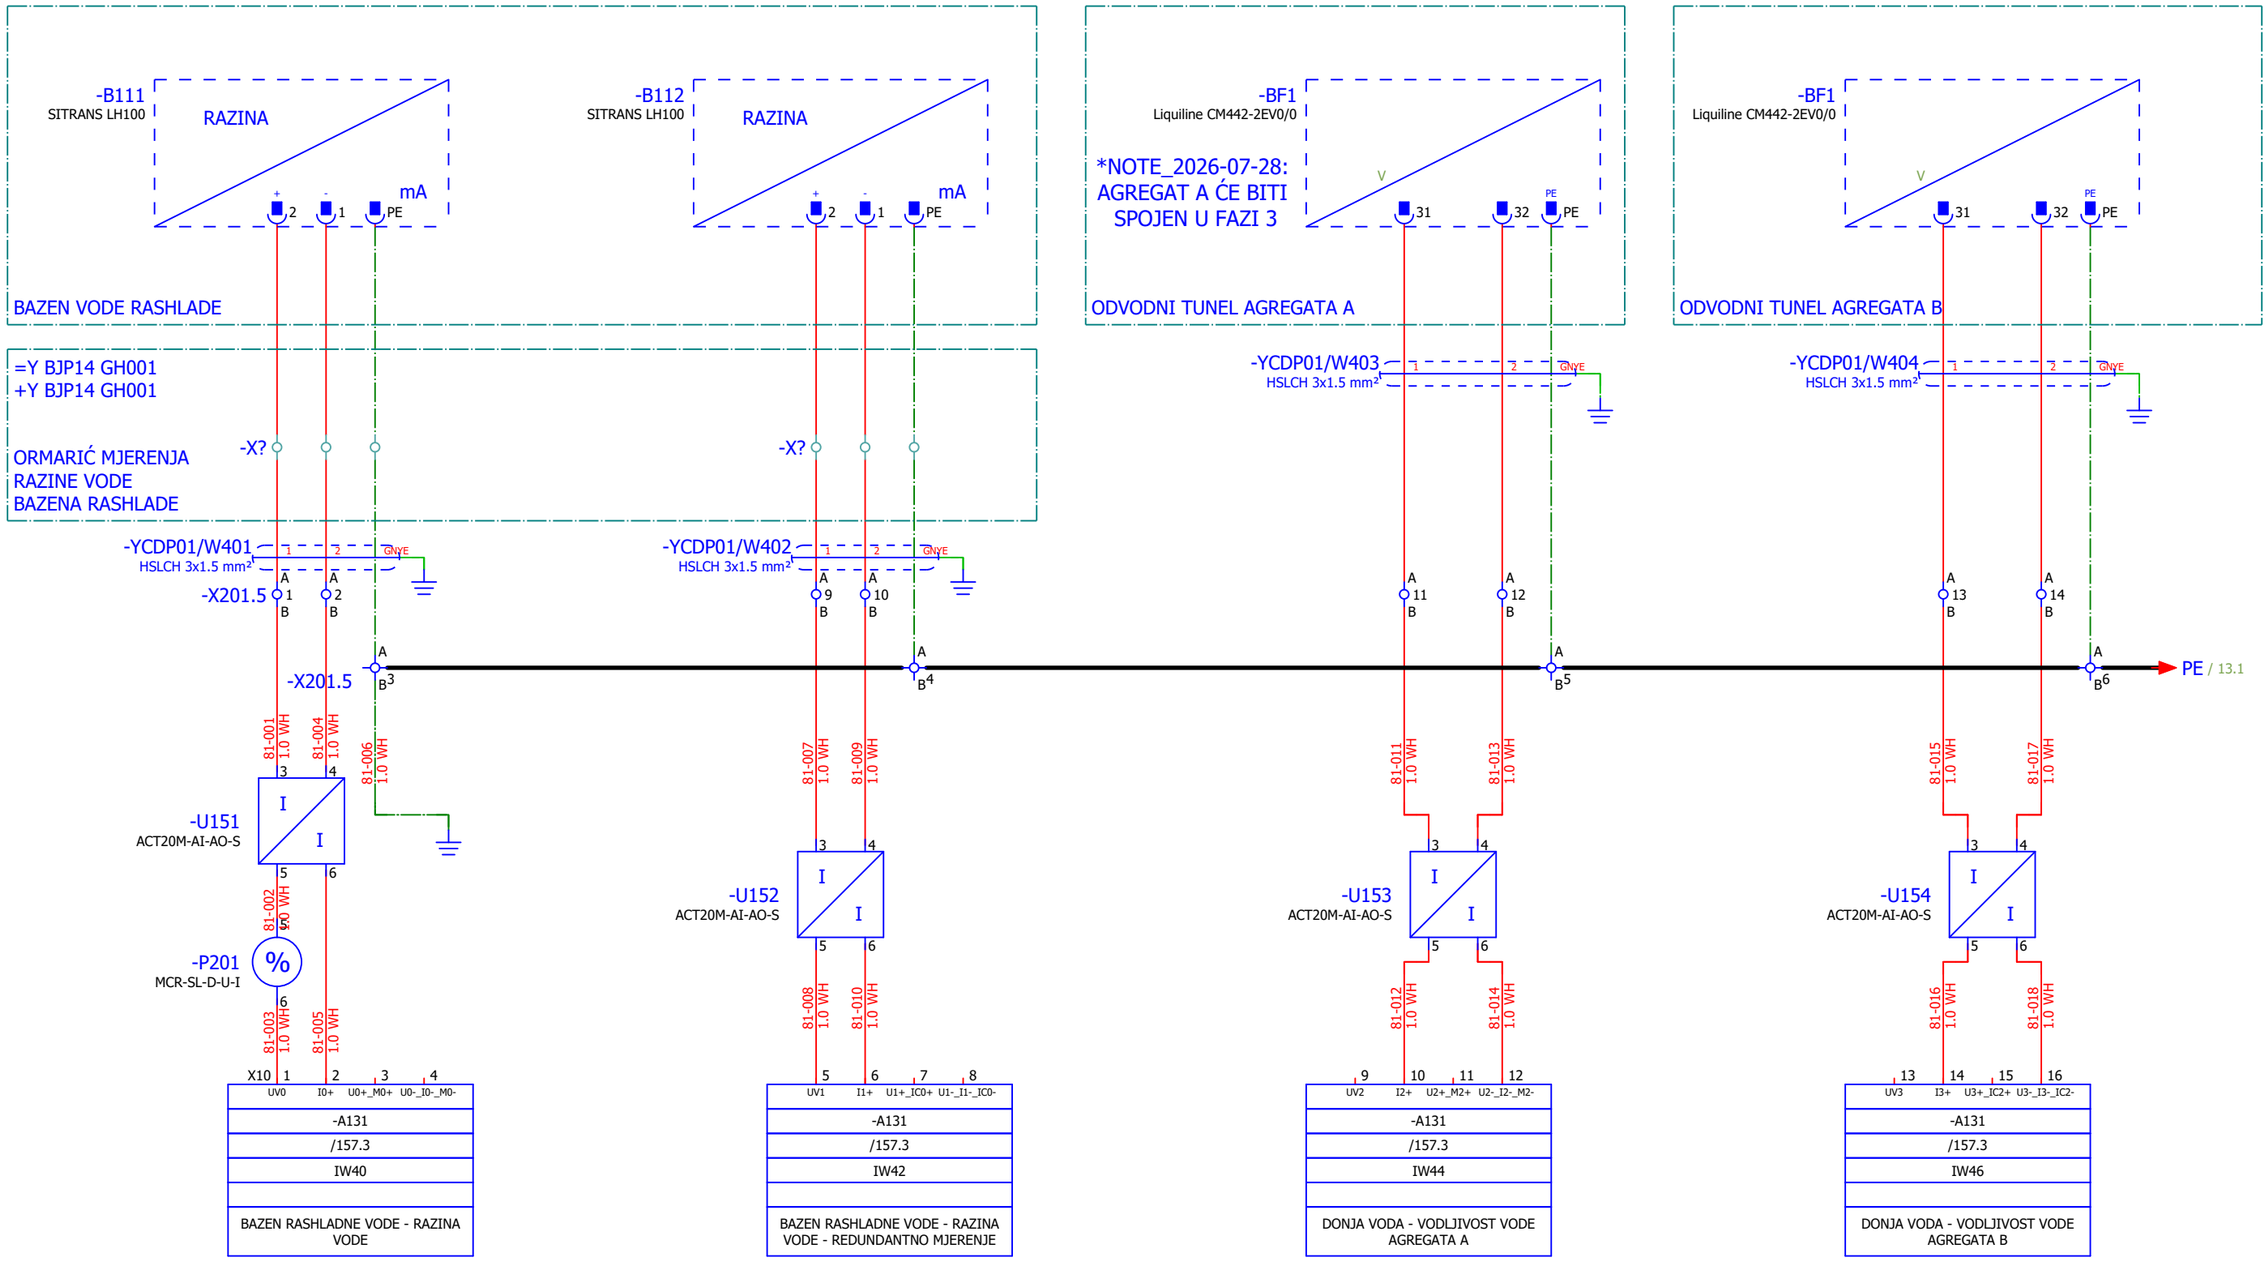

Datum:	31.07.2026.	SINTAKSA A Voith Company	Naručitelj:	HEP - Proizvodnja d.o.o. Ulica grada Vukovara 37, 10000 Zagreb	Investitor:	HRVATSKA ELEKTROPRIVREDA d.d Ulica grada Vukovara 37, 10000 Zagreb	Mapa: 1E12-3 (31)	Prilog: 111	Razina razrade: IZVEDBENI PROJEKT	Projekt: REKONSTRUKCIJA HE SENJ - FAZA I
Gl. projektant:	Natko Vučković									
Projektant:	Patrik Kovač		Građevina:	HE SENJ	Naziv struke projekta:	ELEKTROTEHNIČKI PROJEKT	ZOP: SEN.1273	Naziv mape: Dobava i opskrba rashladnom vodom agregata B		Revizija: 01 / #MB
Izradio:	Luka Božičević									
Odobrio:	Patrik Kovač	Sintaksa d.o.o. HR/21209 Solin, Brza cesta 4 OIB: 32357958120	Lokacija:	Na katastarskim česticama k.o. Sveti Juraj, k.o. Melnice i k.o. Brlog	Sadržaj:	ANALOGNI ULAZI: 1-4	Oznaka nacrta: 26015-DD-EE-01-111-00			=Y BJP14 Y CDP01 / List: 81
Format:	A4									+Y BJP14 Y CDP01 / Slijedi: 82