

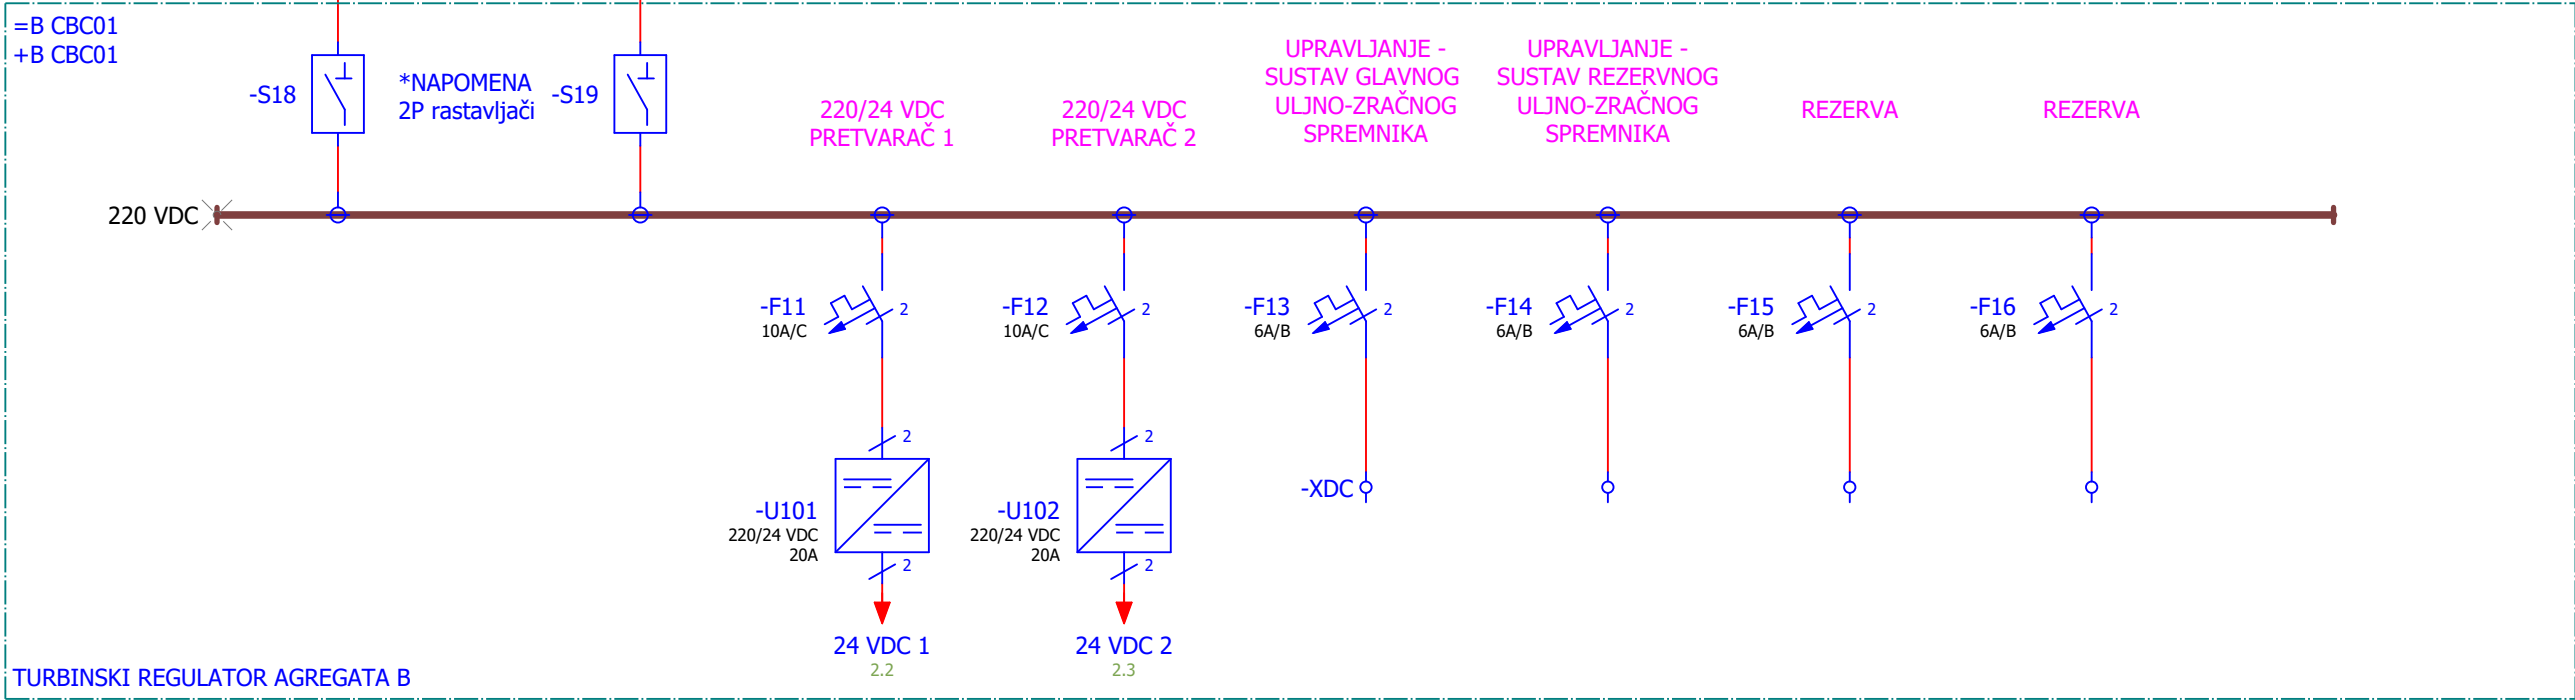


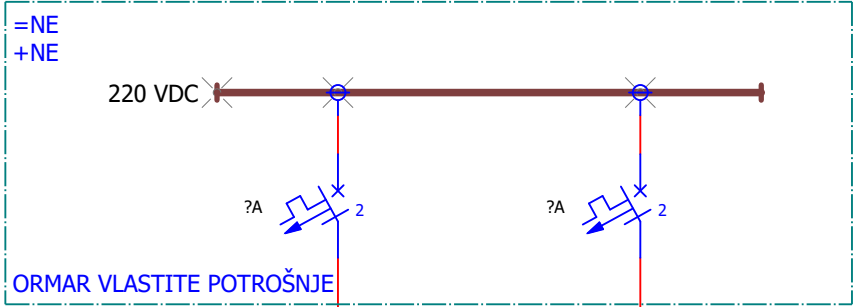

|              |                  |               |                  |
|--------------|------------------|---------------|------------------|
|              |                  |               |                  |
| 00           | Prva verzija     | 2026-05-15    | Tamara Trogrlić  |
| REV.<br>Rev. | NAPOMENA<br>Note | DATUM<br>Date | IZRADIO<br>Drawn |


|   |  |                             |                                                      |  |                                                         |                           |                                                                                              |                          |                             |                     |  |
|---|--|-----------------------------|------------------------------------------------------|--|---------------------------------------------------------|---------------------------|----------------------------------------------------------------------------------------------|--------------------------|-----------------------------|---------------------|--|
| <div><div><div>SINTAKSA</div><div>A Voith Company</div></div><div><div>Sintaksa d.o.o.</div><div>Ulica Domovinskog rata 104C, 21 000 Split,<br/>Tuškanova 37, 10000 Zagreb</div><div>T: +385 1 2310 273<br/>info@sintaksa.hr<br/>www.sintaksa.hr</div></div></div> |  |                             | NAZIV PROJEKTA / POSLA:<br><i>Project / job name</i> |  | REKONSTRUKCIJA HE VARAŽDIN                              |                           |                                                                                              |                          |                             |                     |  |
| PROJEKTANT:<br><i>Design engineer</i>   |  |                             | Patrik Kovač, mag. ing. el. techn. inf.              |  | INVESTITOR /<br>PODNOŠITELJ ZAHTEVA:<br><i>Investor</i> |                           | HRVATSKA ELEKTROPRIVREDA d.o.o<br>Ulica grada Vukovara 37, 10000 Zagreb,<br>OIB: 28921978587 |                          |                             |                     |  |
| IZRADIO:<br><i>Drawn</i>   |  |                             | Tamara Trogrlić, mag. ing. el. techn. inf.           |  | GRAĐEVINA /<br>ZAHVAT U PROSTORU:<br><i>Object</i>      |                           | HE Varaždin<br>Strojarnica i južni aneks strojarnice                                         |                          |                             |                     |  |
| KONTROLIRAO:<br><i>Checked</i>   |  |                             | Patrik Kovač, mag. ing. el. techn. inf.              |  | PROJEKTIRANI DIO:<br><i>Scope of design</i>             |                           | Turbinska regulacija agregat B                                                               |                          |                             |                     |  |
| GLAVNI PROJEKTANT:<br><i>Design manager</i>   |  |                             |                                                      |  | RAZINA-STRUKA:<br><i>Design type</i>                    |                           | Glavni projekt - Elektrotehnički                                                             |                          |                             |                     |  |
| MJESTO I DATUM:<br><i>Place and date</i>   |  |                             | Zagreb, 2026-05-15                                   |  | SADRŽAJ:<br><i>Content</i>                              |                           | JEDNOPOLNA SHEMA 220 VDC I 24 VDC<br>RAZVODA TURBINSKOG REGULATORA<br>AGREGATA B             |                          |                             |                     |  |
| OZNAKA NACRTA<br><i>Drawing designation</i>   |  | FORMAT<br><i>Paper size</i> | MJERILO<br><i>Scale</i>                              |  | ZOP<br><i>Com. pr. des.</i>                             | PROJEKT<br><i>Project</i> | MAPA<br><i>Folder</i>                                                                        | PRILOG<br><i>Drawing</i> | REVIZIJA<br><i>Revision</i> | LIST<br><i>Page</i> |  |
| 18047-MD-EE-04-100   |  | A3                          | -                                                    |  | 14/16                                                   | — 18047-MD —              | EE-04                                                                                        | — 100 —                  | 00 —                        | 1 / 14              |  |

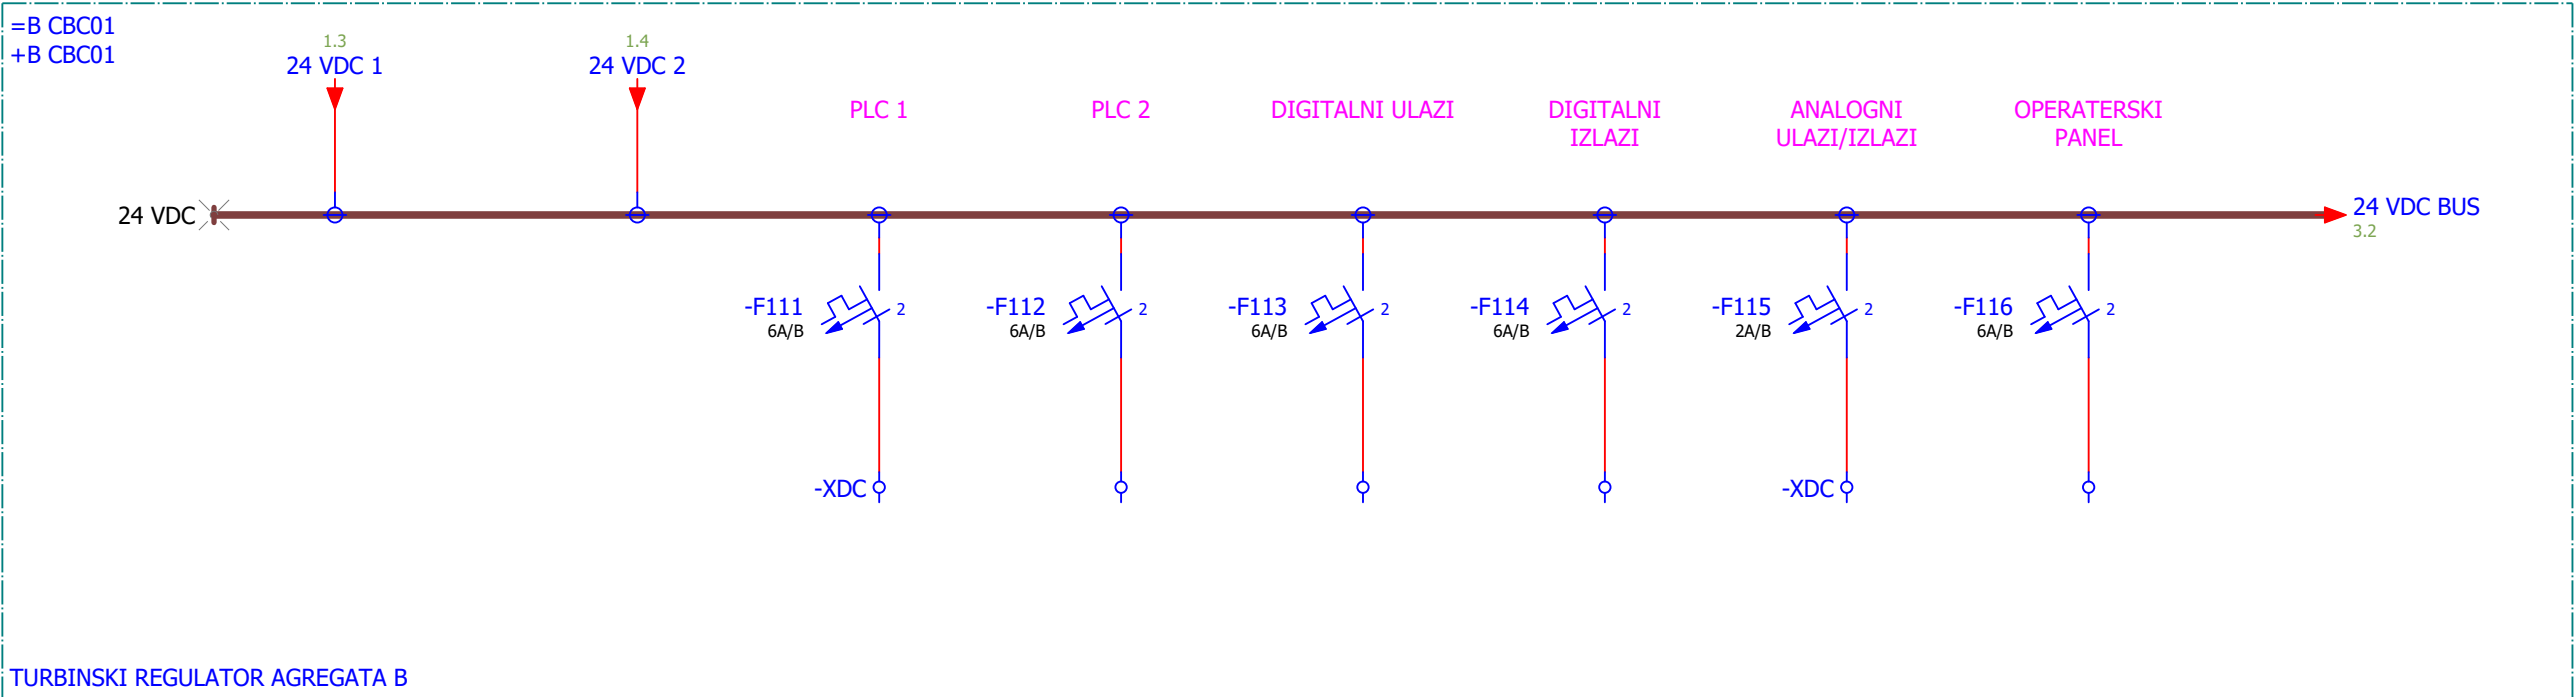

TURBINSKI REGULATOR AGREGATA B

|              |                  |               |                  |
|--------------|------------------|---------------|------------------|
|              |                  |               |                  |
| 00           | Prva verzija     | 2026-05-15    | Tamara Trogrlić  |
| REV.<br>Rev. | NAPOMENA<br>Note | DATUM<br>Date | IZRADIO<br>Drawn |

|   |  
|---|--|--|---|--|--|-------------------------|--|--|-----------------------------|--|--|---------------------------|--|--|-----------------------|--|--|--------------------------|--|--|-----------------------------|--|--|---------------------|--|--|
| <div><div><div><div>SINTAKSA</div><div>A Voith Company</div></div></div><div><div>Sintaksa d.o.o.</div><div>Ulica Domovinskog rata 104C, 21 000 Split,<br/>Tuškanova 37, 10000 Zagreb</div><div>T: +385 1 2310 273<br/>info@sintaksa.hr<br/>www.sintaksa.hr</div></div></div> |  |  | NAZIV PROJEKTA / POSLA:<br><i>Project / job name</i> REKONSTRUKCIJA HE VARAŽDIN                                                                      |  |  
| PROJEKTANT:<br><i>Design engineer</i> Patrik Kovač, mag. ing. el. techn. inf.   |  |  | INVESTITOR /<br>PODNOŠITELJ ZAHTEVA:<br><i>Investor</i> HRVATSKA ELEKTROPRIVREDA d.o.o<br>Ulica grada Vukovara 37, 10000 Zagreb,<br>OIB: 28921978587 |  |  
| IZRADIO:<br><i>Drawn</i> Tamara Trogrlić, mag. ing. el. techn. inf.   |  |  | GRAĐEVINA /<br>ZAHVAT U PROSTORU:<br><i>Object</i> HE Varaždin<br>Strojarnica i južni aneks strojarnice                                              |  |  
| KONTROLIRAO:<br><i>Checked</i> Patrik Kovač, mag. ing. el. techn. inf.   |  |  | PROJEKTIRANI DIO:<br><i>Scope of design</i> Turbinska regulacija agregat B                                                                           |  |  
| GLAVNI PROJEKTANT:<br><i>Design manager</i>   |  |  | RAZINA-STRUKA:<br><i>Design type</i> Glavni projekt - Elektrotehnički                                                                                |  |  
| MJESTO I DATUM:<br><i>Place and date</i> Zagreb, 2026-05-15   |  |  | SADRŽAJ:<br><i>Content</i> JEDNOPOLNA SHEMA 220 VDC I 24 VDC<br>RAZVOĐA TURBINSKOG REGULATORA<br>AGREGATA B                                          |  |  
| OZNAKA NACRTA<br><i>Drawing designation</i>   |  |  | FORMAT<br><i>Paper size</i>   |  |  | MJERILO<br><i>Scale</i> |  |  | ZOP<br><i>Com. pr. des.</i> |  |  | PROJEKT<br><i>Project</i> |  |  | MAPA<br><i>Folder</i> |  |  | PRILOG<br><i>Drawing</i> |  |  | REVIZIJA<br><i>Revision</i> |  |  | LIST<br><i>Page</i> |  |  |
| 18047-MD-EE-04-100   |  |  | A3   |  |  | -                       |  |  | 14/16                       |  |  | — 18047-MD —              |  |  | EE-04                 |  |  | — 100                    |  |  | — 00                        |  |  | — 2 / 14            |  |  |

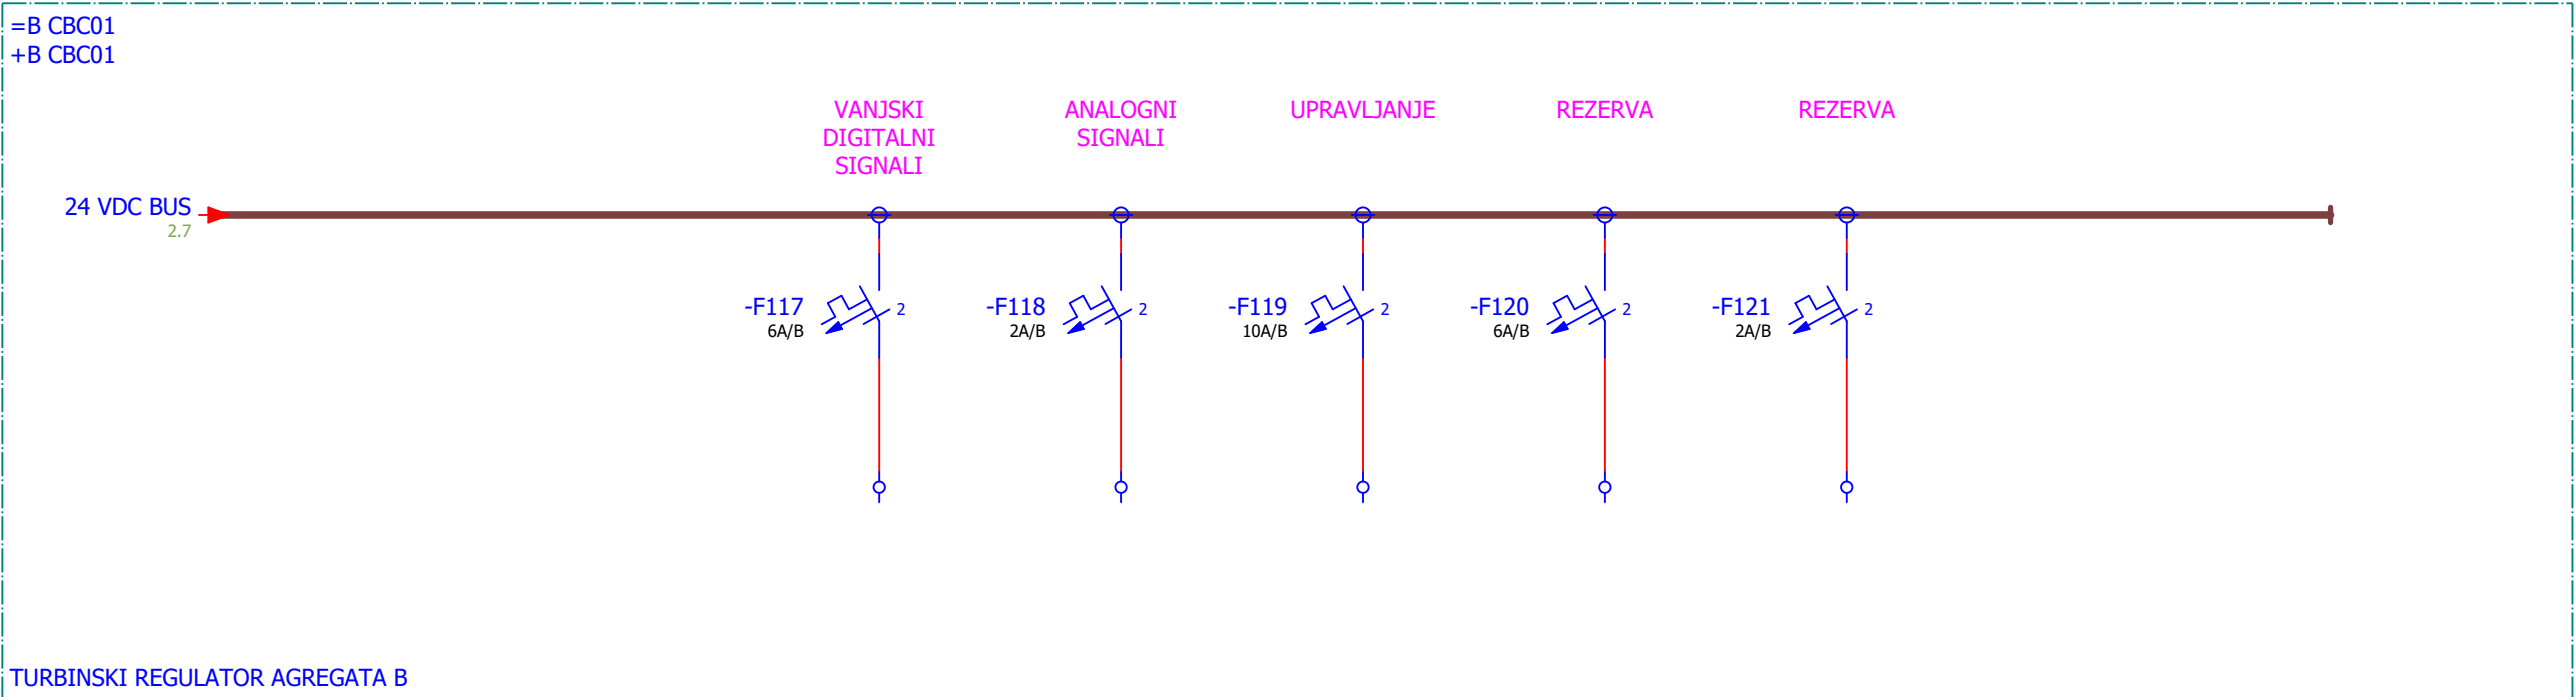

|              |                  |               |                  |
|--------------|------------------|---------------|------------------|
|              |                  |               |                  |
| 00           | Prva verzija     | 2026-05-15    | Tamara Trogrlić  |
| REV.<br>Rev. | NAPOMENA<br>Note | DATUM<br>Date | IZRADIO<br>Drawn |

|   |  
|---|--|--|---|--|--|-------------------|--|--|---------------------------|--|--|----------------------------|--|--|---------------------|--|--|----------------------|--|--|------------------------|--|--|--------------------|--|--|
| <div><div><div><div>SINTAKSA</div><div>A Voith Company</div></div></div><div><div>Sintaksa d.o.o.</div><div>Ulica Domovinskog rata 104C, 21 000 Split,<br/>Tuškanova 37, 10000 Zagreb</div><div>T: +385 1 2310 273<br/>info@sintaksa.hr<br/>www.sintaksa.hr</div></div></div> |  |  | NAZIV PROJEKTA / POSLA:<br>Project / job nameREKONSTRUKCIJA HE VARAŽDIN                                                                       |  |  
| PROJEKTANT:<br>Design engineerPatrik Kovač, mag. ing. el. techn. inf.   |  |  | INVESTITOR /<br>PODNOŠITELJ ZAHTJEVA:<br>InvestorHRVATSKA ELEKTROPRIVREDA d.o.o<br>Ulica grada Vukovara 37, 10000 Zagreb,<br>OIB: 28921978587 |  |  
| IZRADIO:<br>DrawnTamara Trogrlić, mag. ing. el. techn. inf.   |  |  | GRAĐEVINA /<br>ZAHVAT U PROSTORU:<br>ObjectHE Varaždin<br>Strojarnica i južni aneks strojarnice                                               |  |  
| KONTROLIRAO:<br>CheckedPatrik Kovač, mag. ing. el. techn. inf.   |  |  | PROJEKTIRANI DIO:<br>Scope of designTurbinska regulacija agregat B                                                                            |  |  
| GLAVNI PROJEKTANT:<br>Design manager   |  |  | RAZINA-STRUKA:<br>Design typeGlavni projekt - Elektrotehnički                                                                                 |  |  
| MJESTO I DATUM:<br>Place and dateZagreb, 2026-05-15   |  |  | SADRŽAJ:<br>ContentJEDNOPOLNA SHEMA 220 VDC I 24 VDC<br>RAZVODA TURBINSKOG REGULATORA<br>AGREGATA B                                           |  |  
| OZNAKA NACRTA<br>Drawing designation18047-MD-EE-04-100   |  |  | FORMAT<br>Paper sizeA3   |  |  | MJERILO<br>Scale- |  |  | ZOP<br>Com. pr. des.14/16 |  |  | PROJEKT<br>Project18047-MD |  |  | MAPA<br>FolderEE-04 |  |  | PRILOG<br>Drawing100 |  |  | REVIZIJA<br>Revision00 |  |  | LIST<br>Page3 / 14 |  |  |