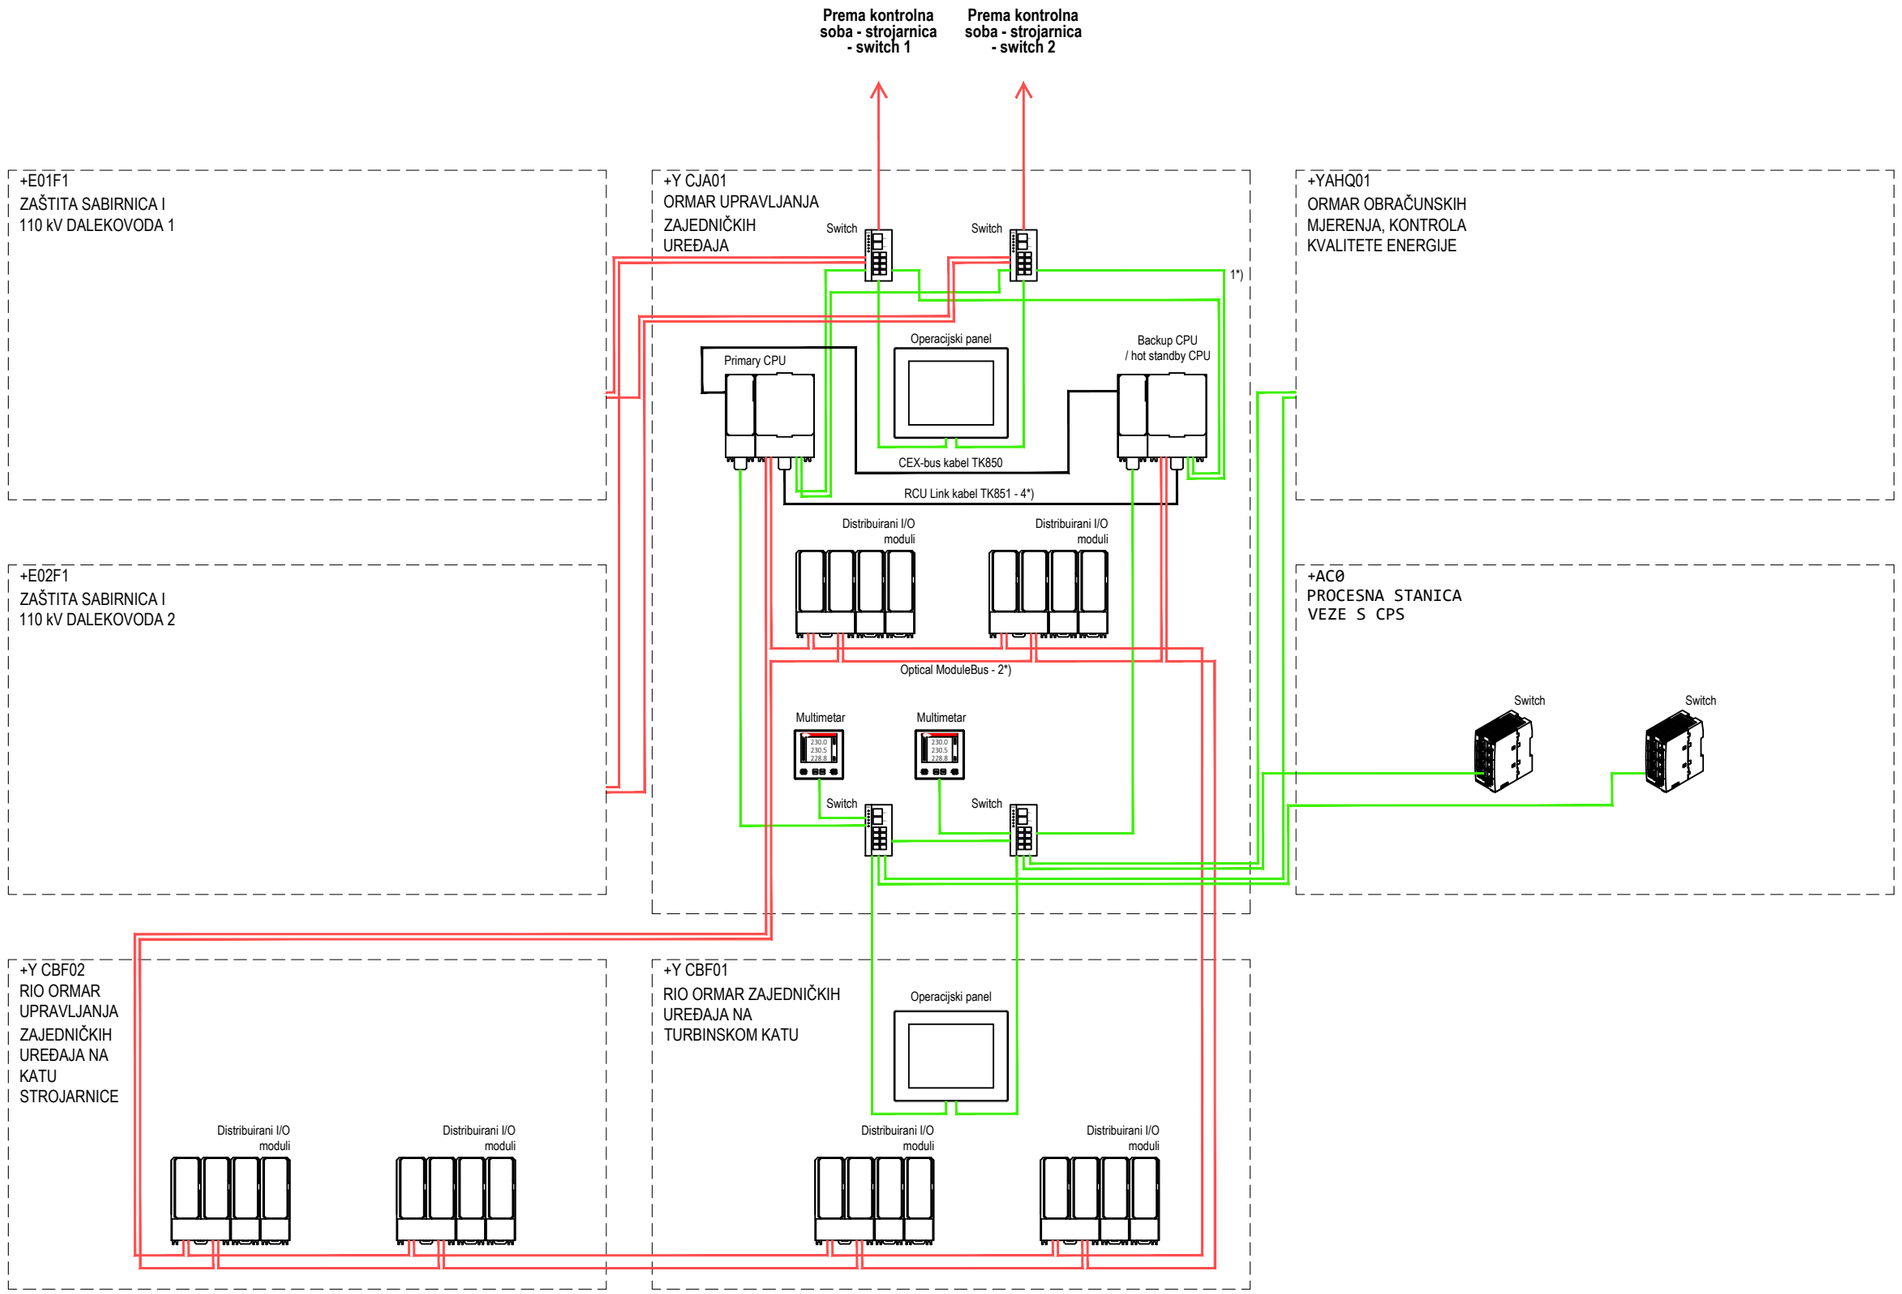

LEGEND:

- Ethernet / Profinet / Modbus TCP-IP/ IEC60870-5-104
- Cu (Hard-wired)
- FO
- Profibus

REV. *Rev.*	NAPOMENA *Note*	DATUM *Date*	IZRADIO *Drawn*
00	Prva verzija	2026-04-17	Patrik Kovač

SINTAKSA
A Voith Company

Sintaksa d.o.o.
Ulica Domovinskog rata 104C, 21 000 Split,
Tuškanova 37, 10000 Zagreb
T: +385 1 2310 273
info@sintaksa.hr
www.sintaksa.hr

PROJEKTANT: *Design engineer*	Patrik Kovač, mag.ing.el.techn.inf
IZRADIO: *Drawn*	Patrik Kovač, mag.ing.el.techn.inf
KONTROLIRAO: *Checked*	Patrik Kovač, mag.ing.el.techn.inf
GLAVNI PROJEKTANT: *Design manager*	-
MJESTO I DATUM: *Place and date*	Zagreb, 2026-04-17

NAZIV PROJEKTA / POSLA: *Project / job name*	**REKONSTRUKCIJA HE VARAŽDIN**
INVESTITOR / PODNOSITELJ ZAHTJEVA: *Investor*	HRVATSKA ELEKTROPRIVREDA d.o.o Ulica grada Vukovara 37, 10000 Zagreb, OIB: 28921978587
GRAĐEVINA / ZAHVAT U PROSTORU: *Object*	**HE Varaždin** Strojarnica i južni aneks strojarnice
PROJEKTIRANI DIO: *Scope of design*	Sustav automatizacija, upravljanja, signalizacije, zaštite i mjerenja
RAZINA-STRUKA: *Design type*	Glavni projekt - elektrotehnički
SADRŽAJ: *Content*	**KOMUNIKACIJSKA TOPOLOGIJA - ORMAR UPRAVLJANJA ZAJEDNIČKIH UREĐAJA**

OZNAKA NACRTA *Drawing designation*	FORMAT *Paper size*	MJERILO *Scale*
18047-MD-EE-01	A3	-

ZOP *Common pr. des.*	PROJEKT *Project*	MAPA *Folder*	PRILOG *Drawing*	REVIZIJA *Revision*	LIST *Page*
14/16	18047	EE-01	102	00	3/3